


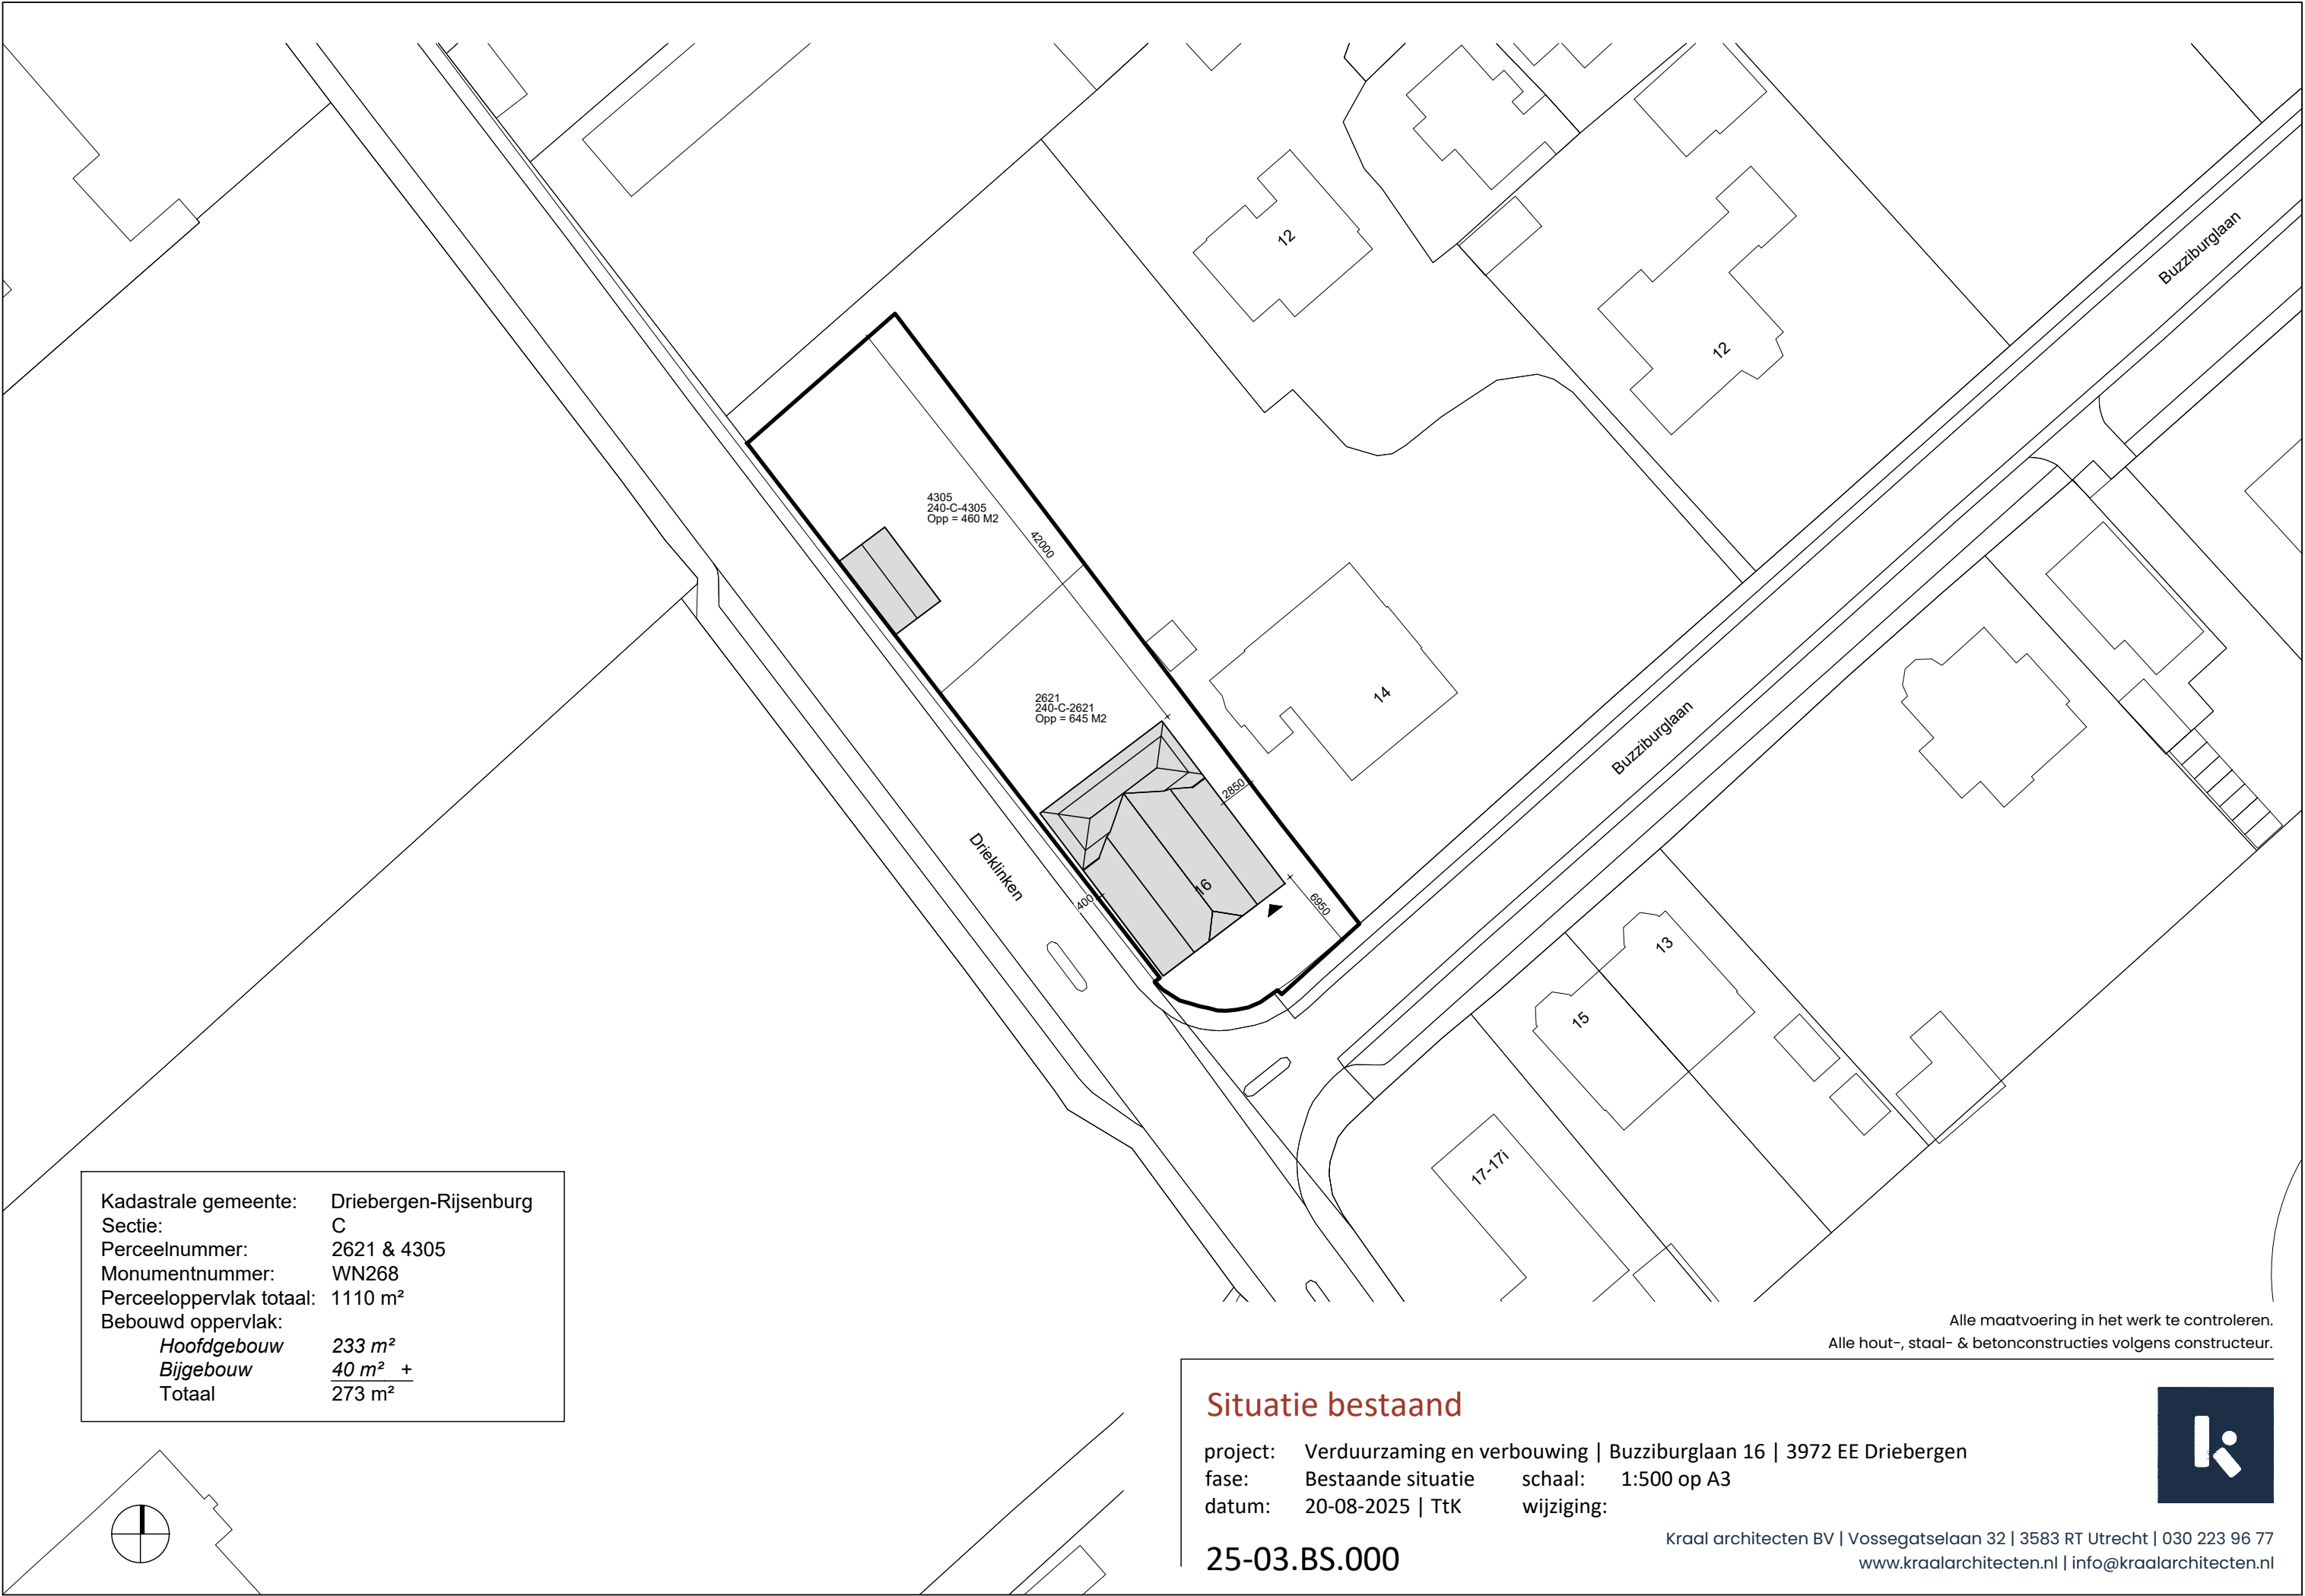

Kadastrale gemeente:	Driebergen-Rijsenburg
Sectie:	C
Perceelnummer:	2621 & 4305
Monumentnummer:	WN268
Perceeloppervlak totaal:	1110 m²
Bebouwd oppervlak:	
Hoofdgebouw	233 m²
Bijgebouw	40 m² +
Totaal	273 m²

Alle maatvoering in het werk te controleren.
Alle hout-, staal- & betonconstructies volgens constructeur.


Situatie bestaand

project: Verduurzaming en verbouwing | Buzziburglaan 16 | 3972 EE Driebergen
fase: Bestaande situatie schaal: 1:500 op A3
datum: 20-08-2025 | TtK wijziging:

25-03.BS.000

Kraal architecten BV | Vossegatselaan 32 | 3583 RT Utrecht | 030 223 96 77
www.kraalarchitecten.nl | info@kraalarchitecten.nl



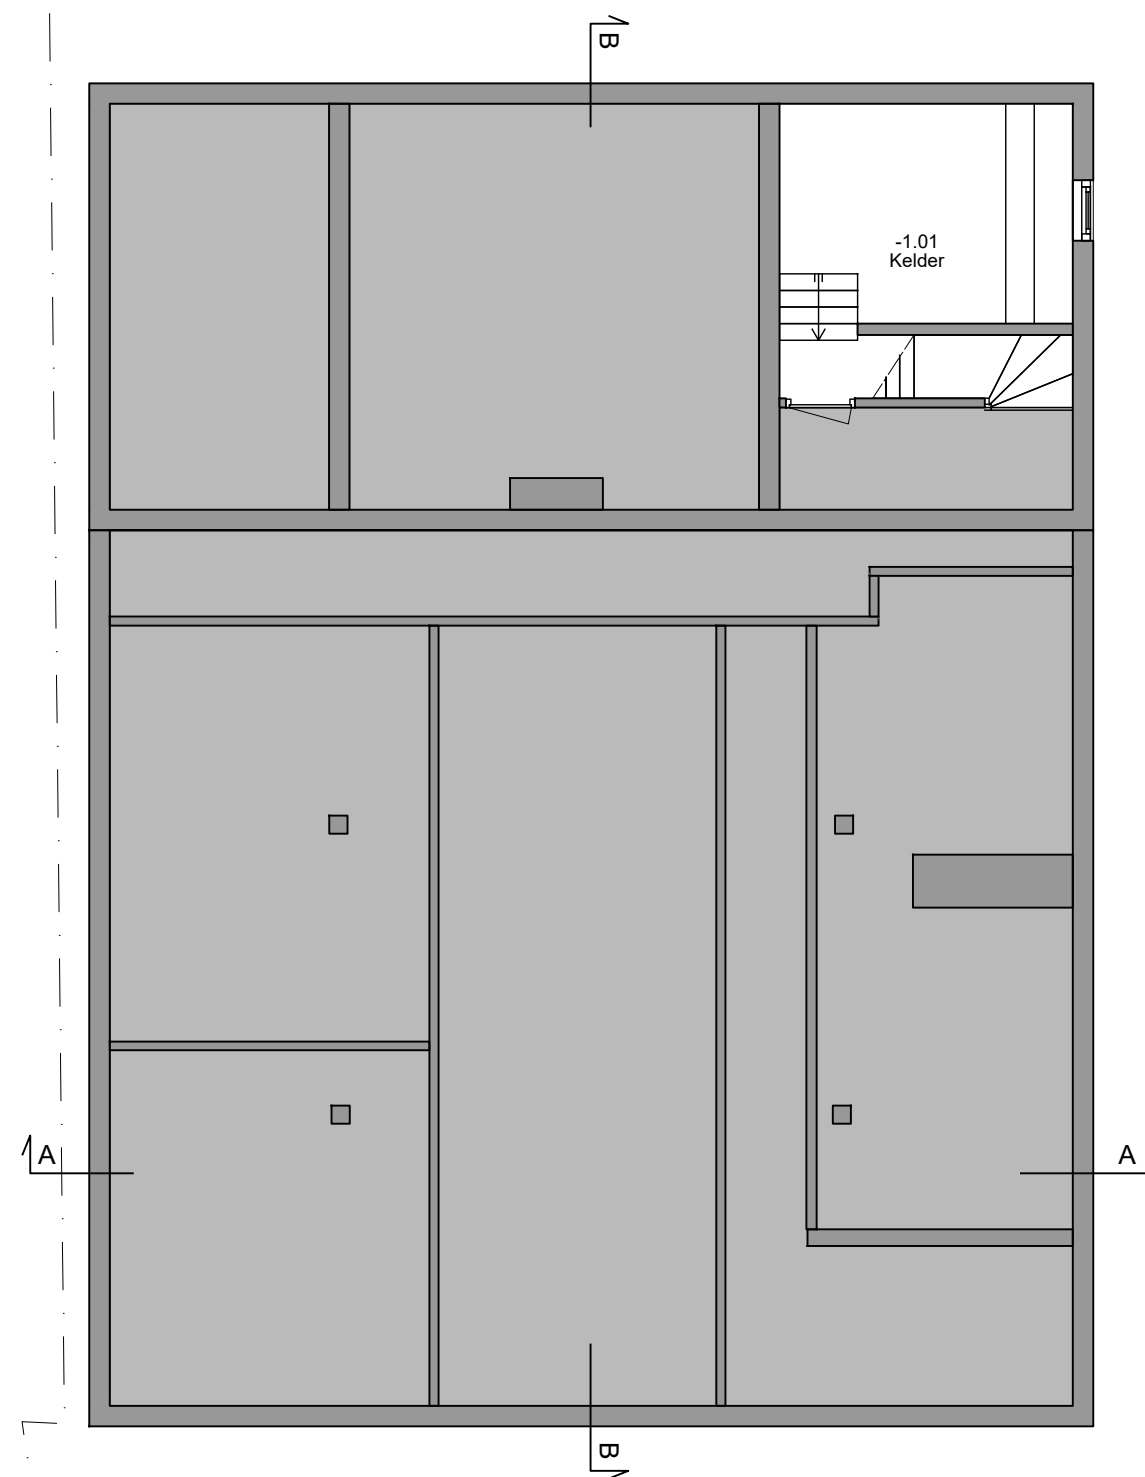

Alle maatvoering in het werk te controleren.
Alle hout-, staal- & betonconstructies volgens constructeur.


Plattegrond kelder & fundering bestaand

project: Verduurzaming en verbouwing | Buzziburglaan 16 | 3972 EE Driebergen
fase: Bestaande situatie schaal: 1:100 op A3
datum: 20-08-2025 | TtK wijziging:

25-03.BS.10-1

Kraal architecten BV | Vossegatselaan 32 | 3583 RT Utrecht | 030 223 96 77
www.kraalarchitecten.nl | info@kraalarchitecten.nl



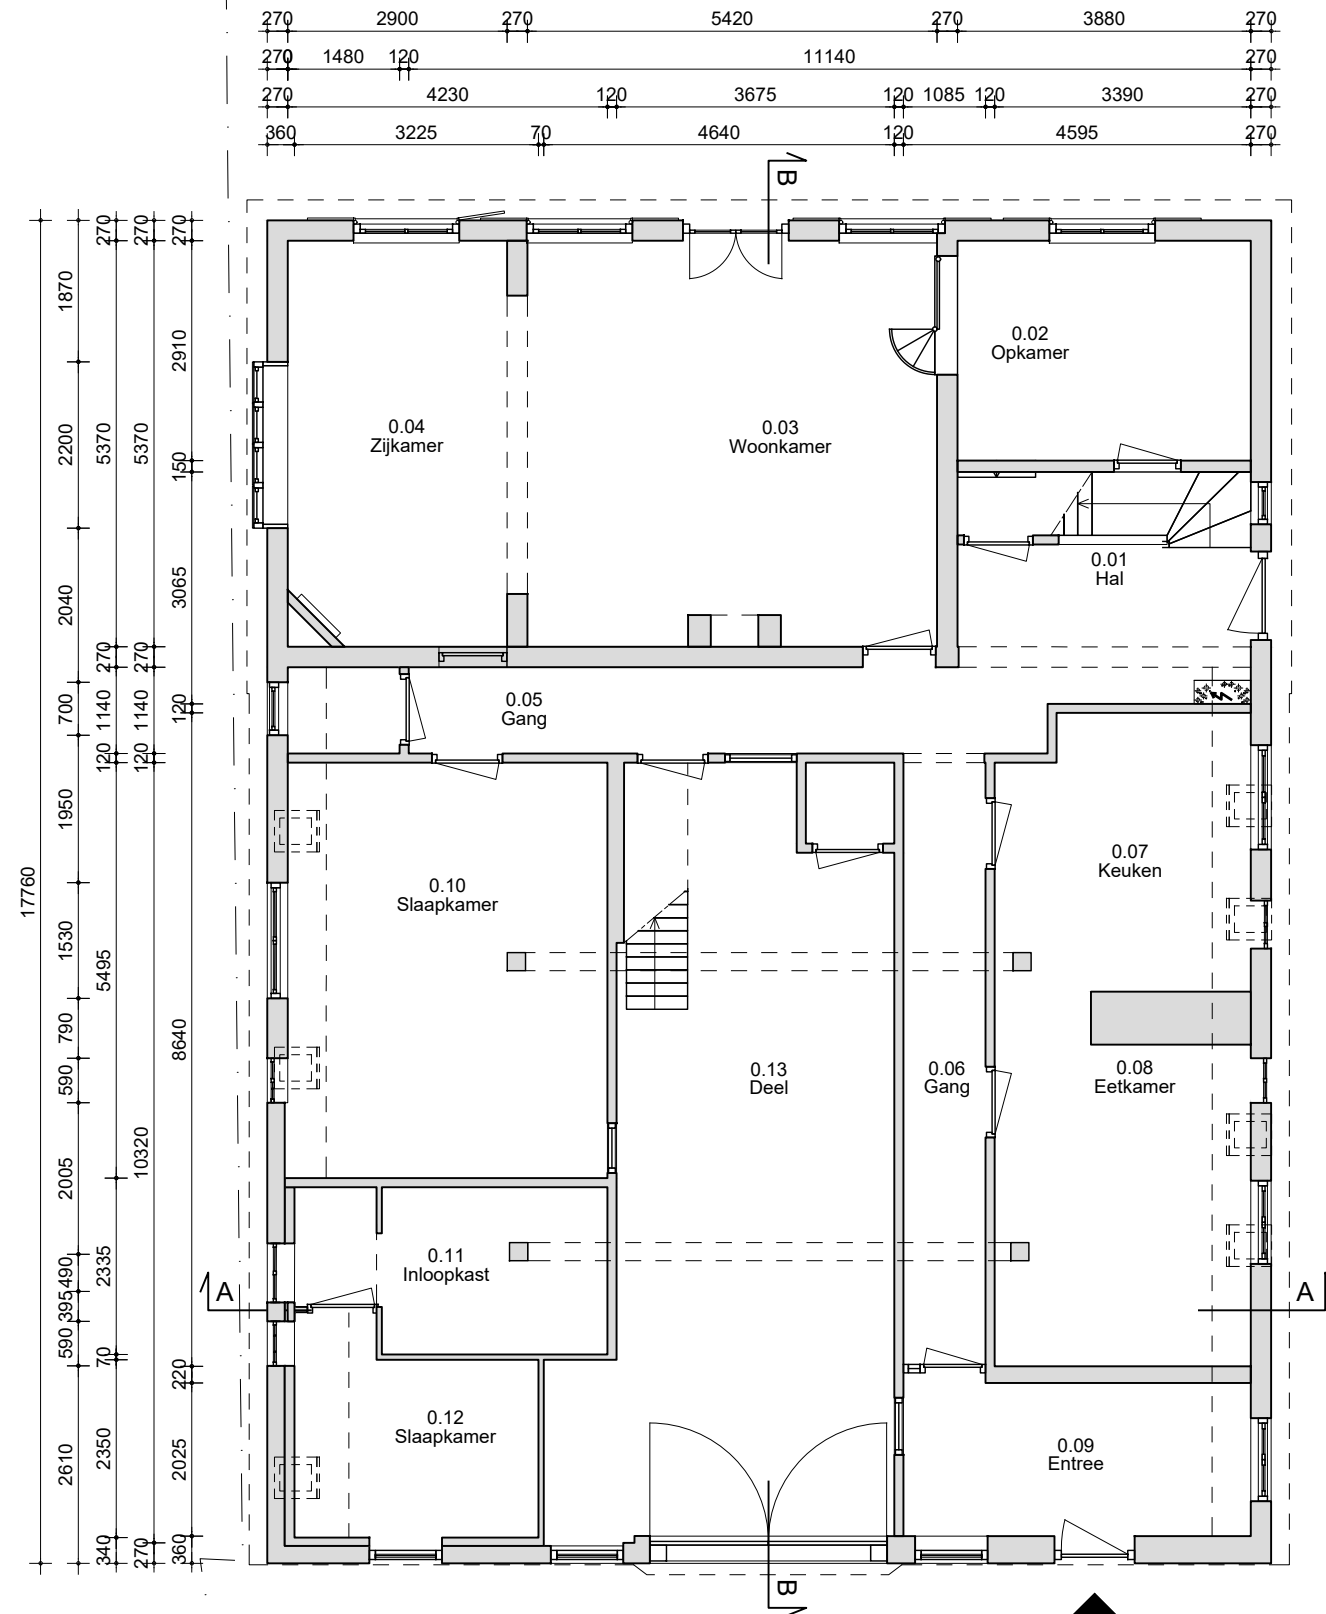

Alle maatvoering in het werk te controleren.
Alle hout-, staal- & betonconstructies volgens constructeur.


Plattegrond begane grond bestaand

project: Verduurzaming en verbouwing | Buzziburglaan 16 | 3972 EE Driebergen
fase: Bestaande situatie schaal: 1:100 op A3
datum: 20-08-2025 | TtK wijziging:

25-03.BS.100

Kraal architecten BV | Vossegatselaan 32 | 3583 RT Utrecht | 030 223 96 77
www.kraalarchitecten.nl | info@kraalarchitecten.nl



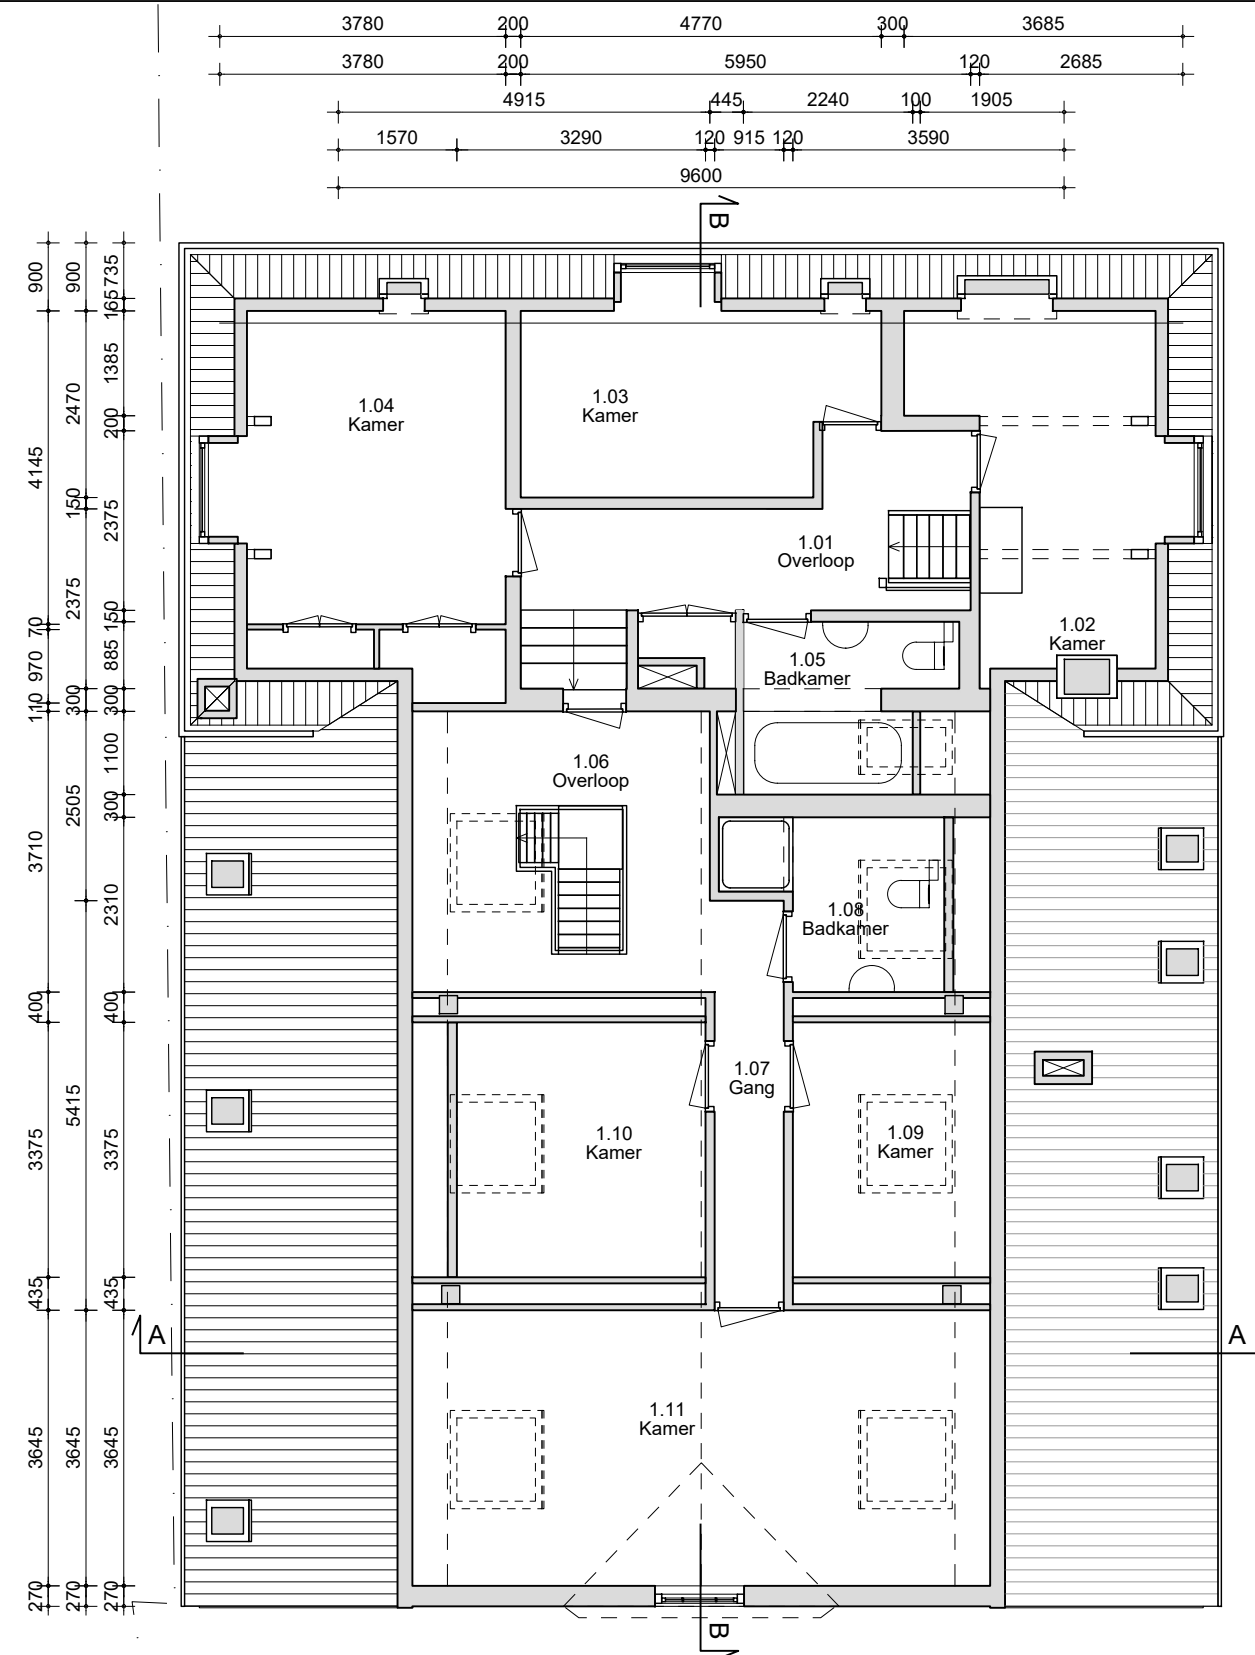

Alle maatvoering in het werk te controleren.
Alle hout-, staal- & betonconstructies volgens constructeur.


Plattegrond 1e verdieping bestand

project: Verduurzaming en verbouwing | Buzziburglaan 16 | 3972 EE Driebergen
fase: Bestaande situatie schaal: 1:100 op A3
datum: 20-08-2025 | TtK wijziging:

25-03.BS.101

Kraal architecten BV | Vossegatselaan 32 | 3583 RT Utrecht | 030 223 96 77
www.kraalarchitecten.nl | info@kraalarchitecten.nl



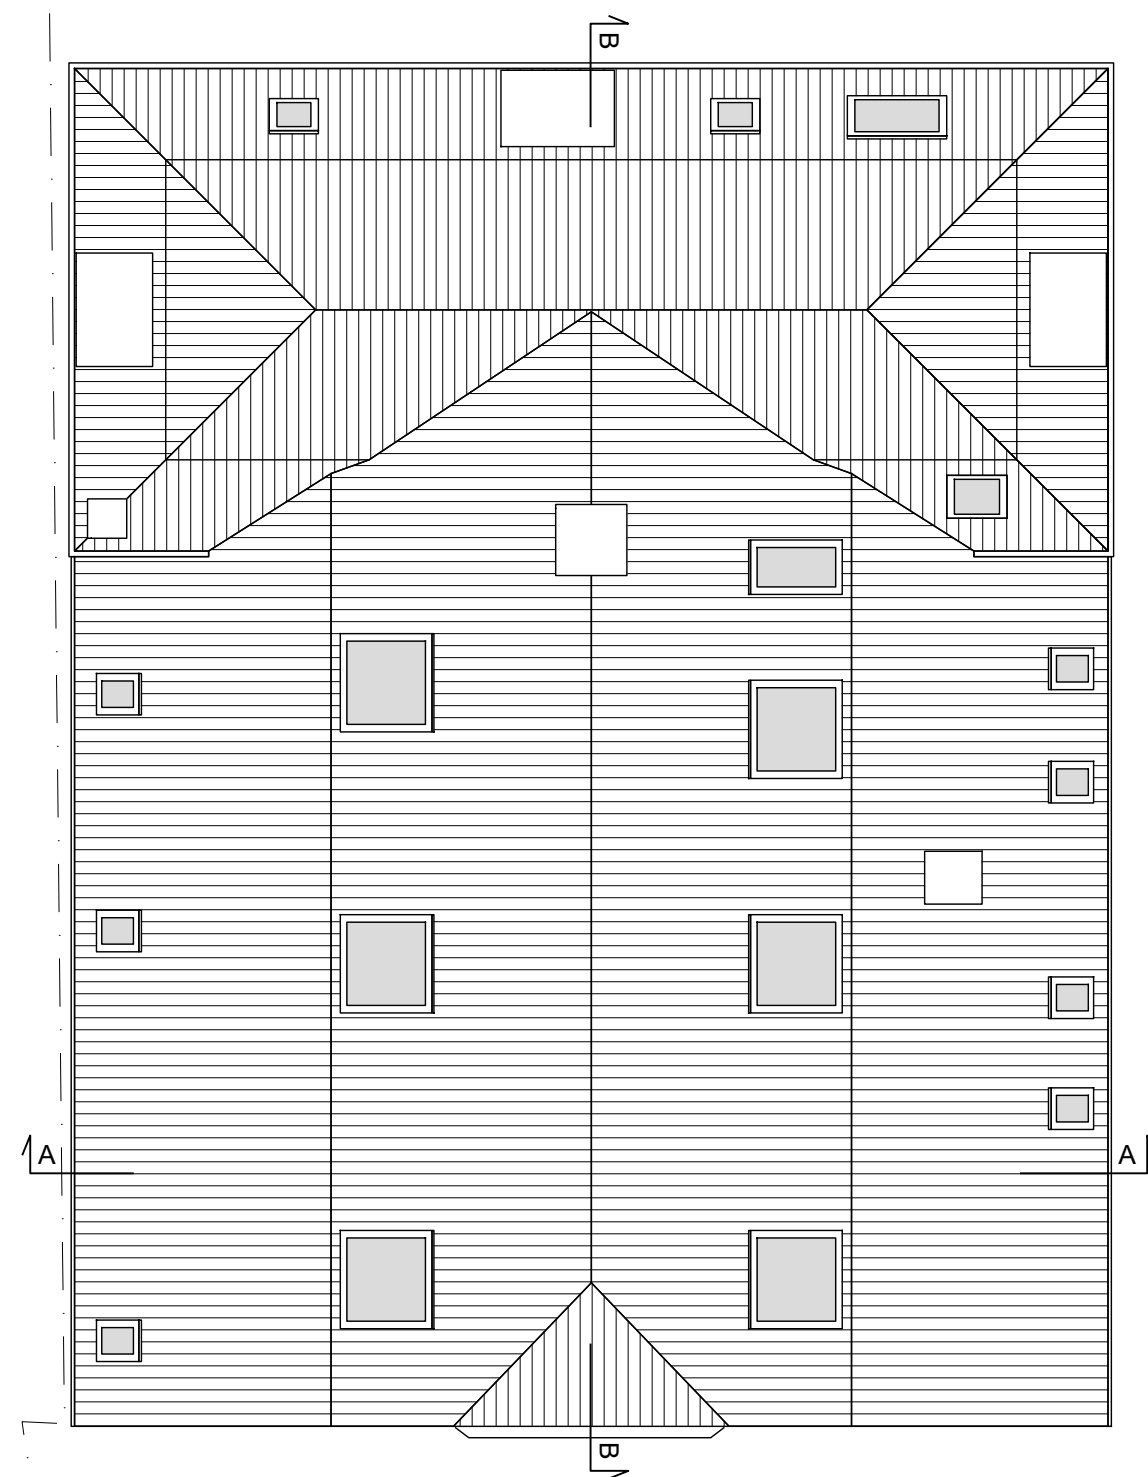

Alle maatvoering in het werk te controleren.
Alle hout-, staal- & betonconstructies volgens constructeur.

Plattegrond dak bestaand

project: Verduurzaming en verbouwing | Buzziburglaan 16 | 3972 EE Driebergen
fase: Bestaande situatie schaal: 1:100 op A3
datum: 20-08-2025 | TtK wijziging:

25-03.BS.102

Kraal architecten BV | Vossegatselaan 32 | 3583 RT Utrecht | 030 223 96 77
www.kraalarchitecten.nl | info@kraalarchitecten.nl





Alle maatvoering in het werk te controleren.
Alle hout-, staal- & betonconstructies volgens constructeur.


Gevelaanzichten bestand

project: Verduurzaming en verbouwing | Buzziburglaan 16 | 3972 EE Driebergen
fase: Bestaande situatie schaal: 1:100 op A3
datum: 20-08-2025 | TtK wijziging:


25-03.BS.200

Kraal architecten BV | Vossegatselaan 32 | 3583 RT Utrecht | 030 223 96 77
www.kraalarchitecten.nl | info@kraalarchitecten.nl



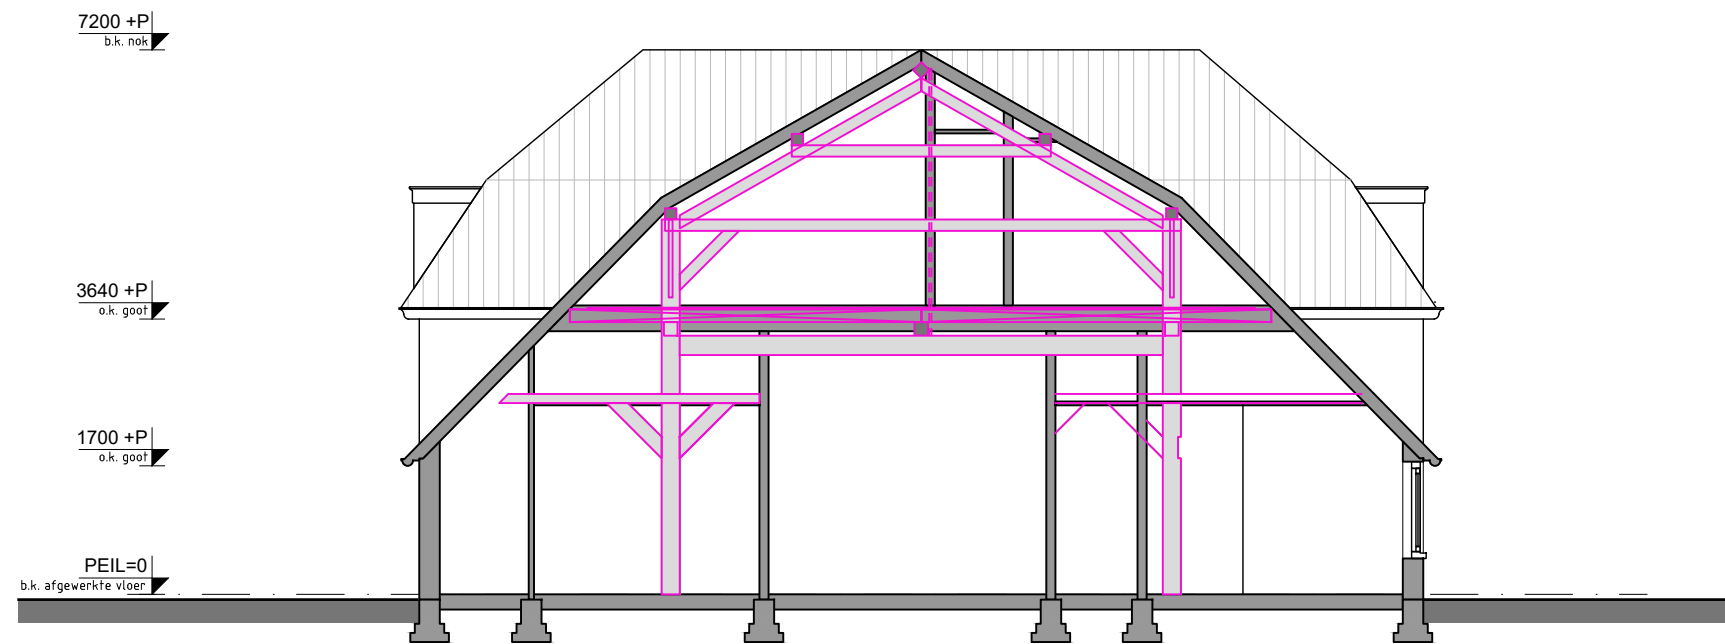

DOORSNEDE A-A

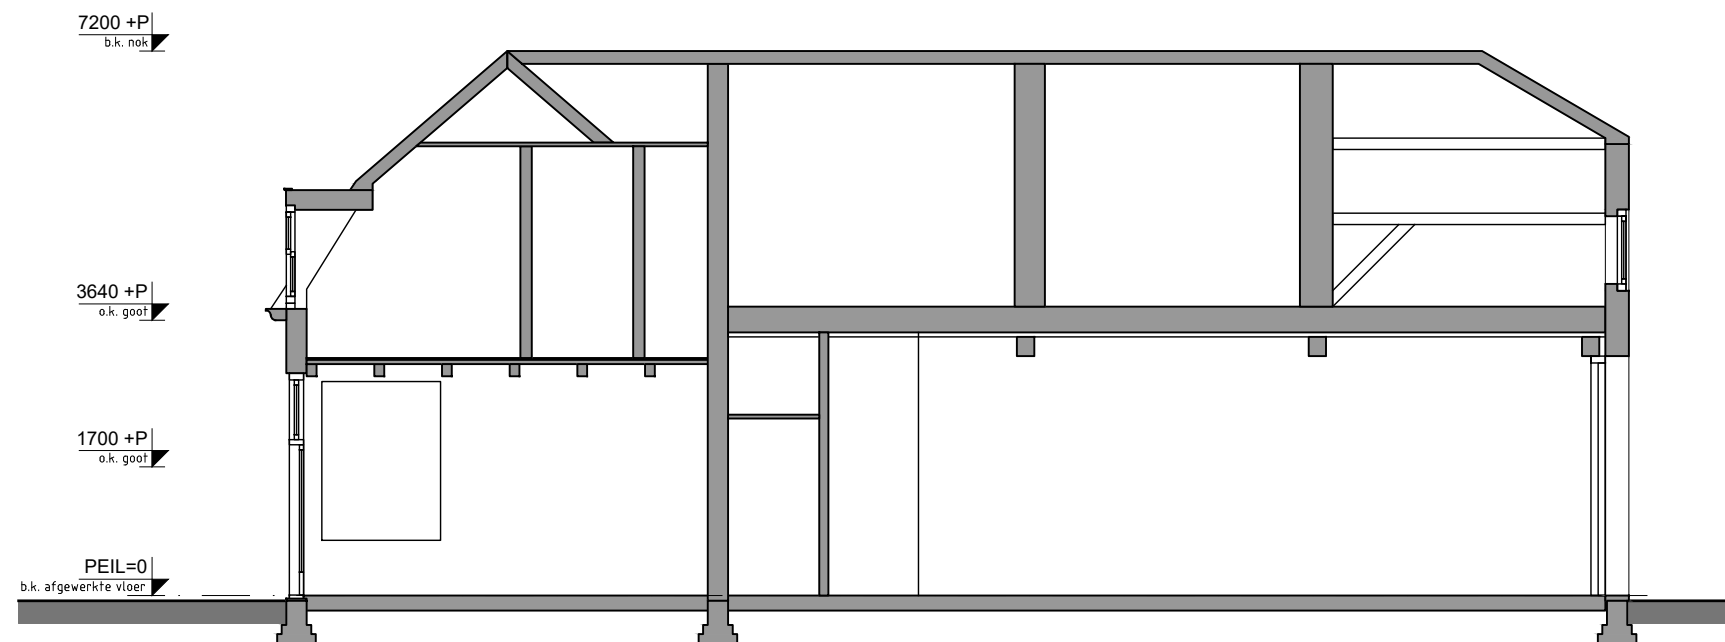

DOORSNEDE B-B

Alle maatvoering in het werk te controleren.
Alle hout-, staal- & betonconstructies volgens constructeur.


Doorsneden bestand

project: Verduurzaming en verbouwing | Buzziburglaan 16 | 3972 EE Driebergen
fase: Bestaande situatie schaal: 1:100 op A3
datum: 20-08-2025 | TtK wijziging:


25-03.BS.300

Kraal architecten BV | Vossegatselaan 32 | 3583 RT Utrecht | 030 223 96 77
www.kraalarchitecten.nl | info@kraalarchitecten.nl



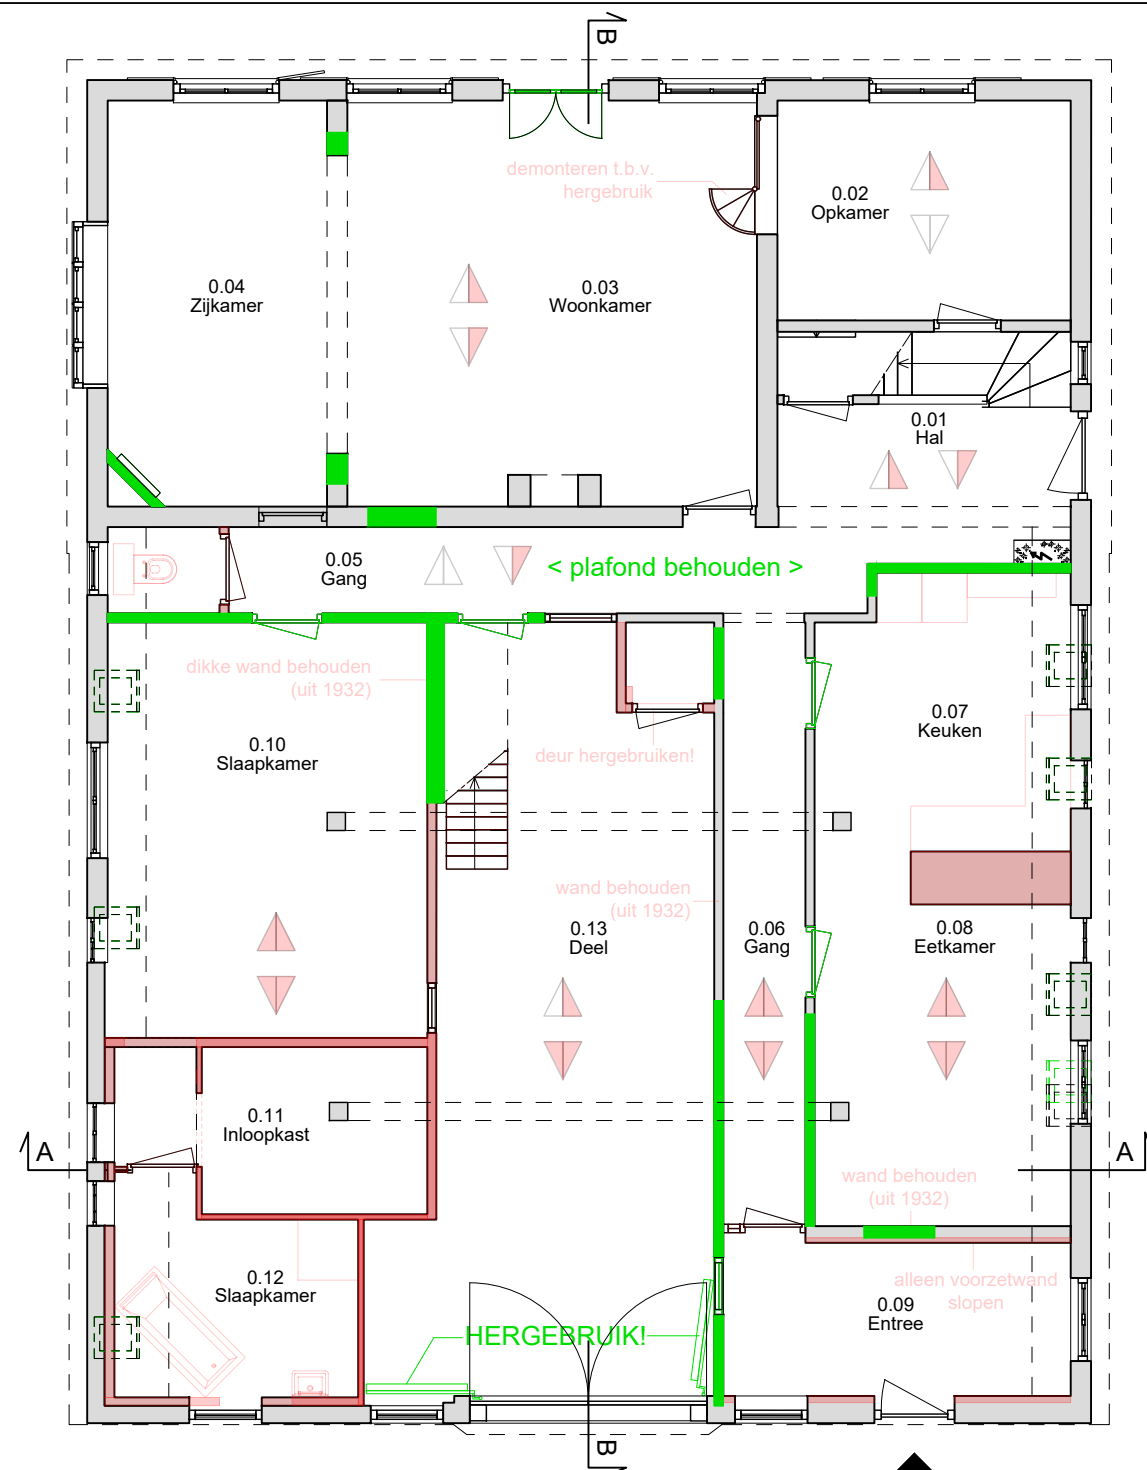

Legenda slopen Begane grond			
	= slopen FASE 1 (reeds vergund)		= slopen FASE 2
	slopen		NIET slopen
	links = plafond- of balkconstructie		rechts = onderplafond of gips tussen balken
	links = ondervloer		rechts = dekvloer

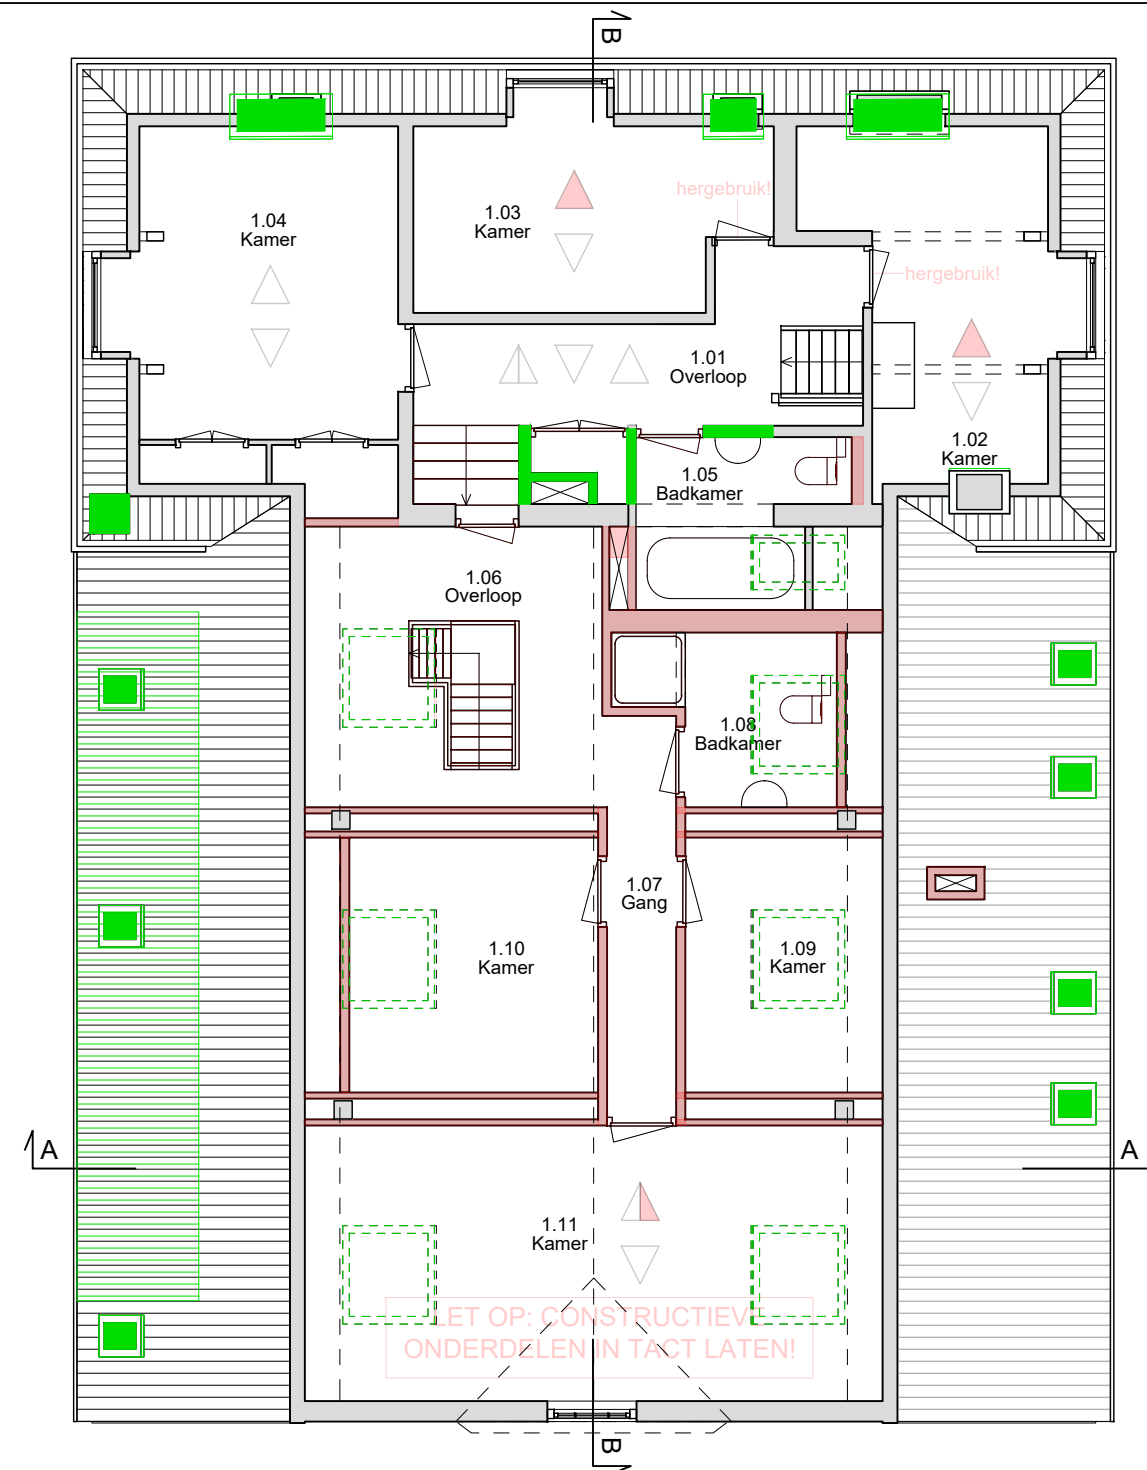

Legenda slopen 1e verdieping			
	= slopen FASE 1 (reeds vergund)		= slopen FASE 2
	slopen		NIET slopen
	links = kapconstructie		rechts = dakbeschothoutwolcementplaten
			= plafond
			= vloer

Alle maatvoering in het werk te controleren.
Alle hout-, staal- & betonconstructies volgens constructeur.


Slooptekening FASE 2

project: Verduurzaming en verbouwing | Buzziburglaan 16 | 3972 EE Driebergen
fase: Bestaande situatie schaal: 1:100 op A3
datum: 03-07-2026 | TtK wijziging:

25-03.BS.010 sloop FASE 2

Kraal architecten BV | Vossegatselaan 32 | 3583 RT Utrecht | 030 223 96 77
www.kraalarchitecten.nl | info@kraalarchitecten.nl



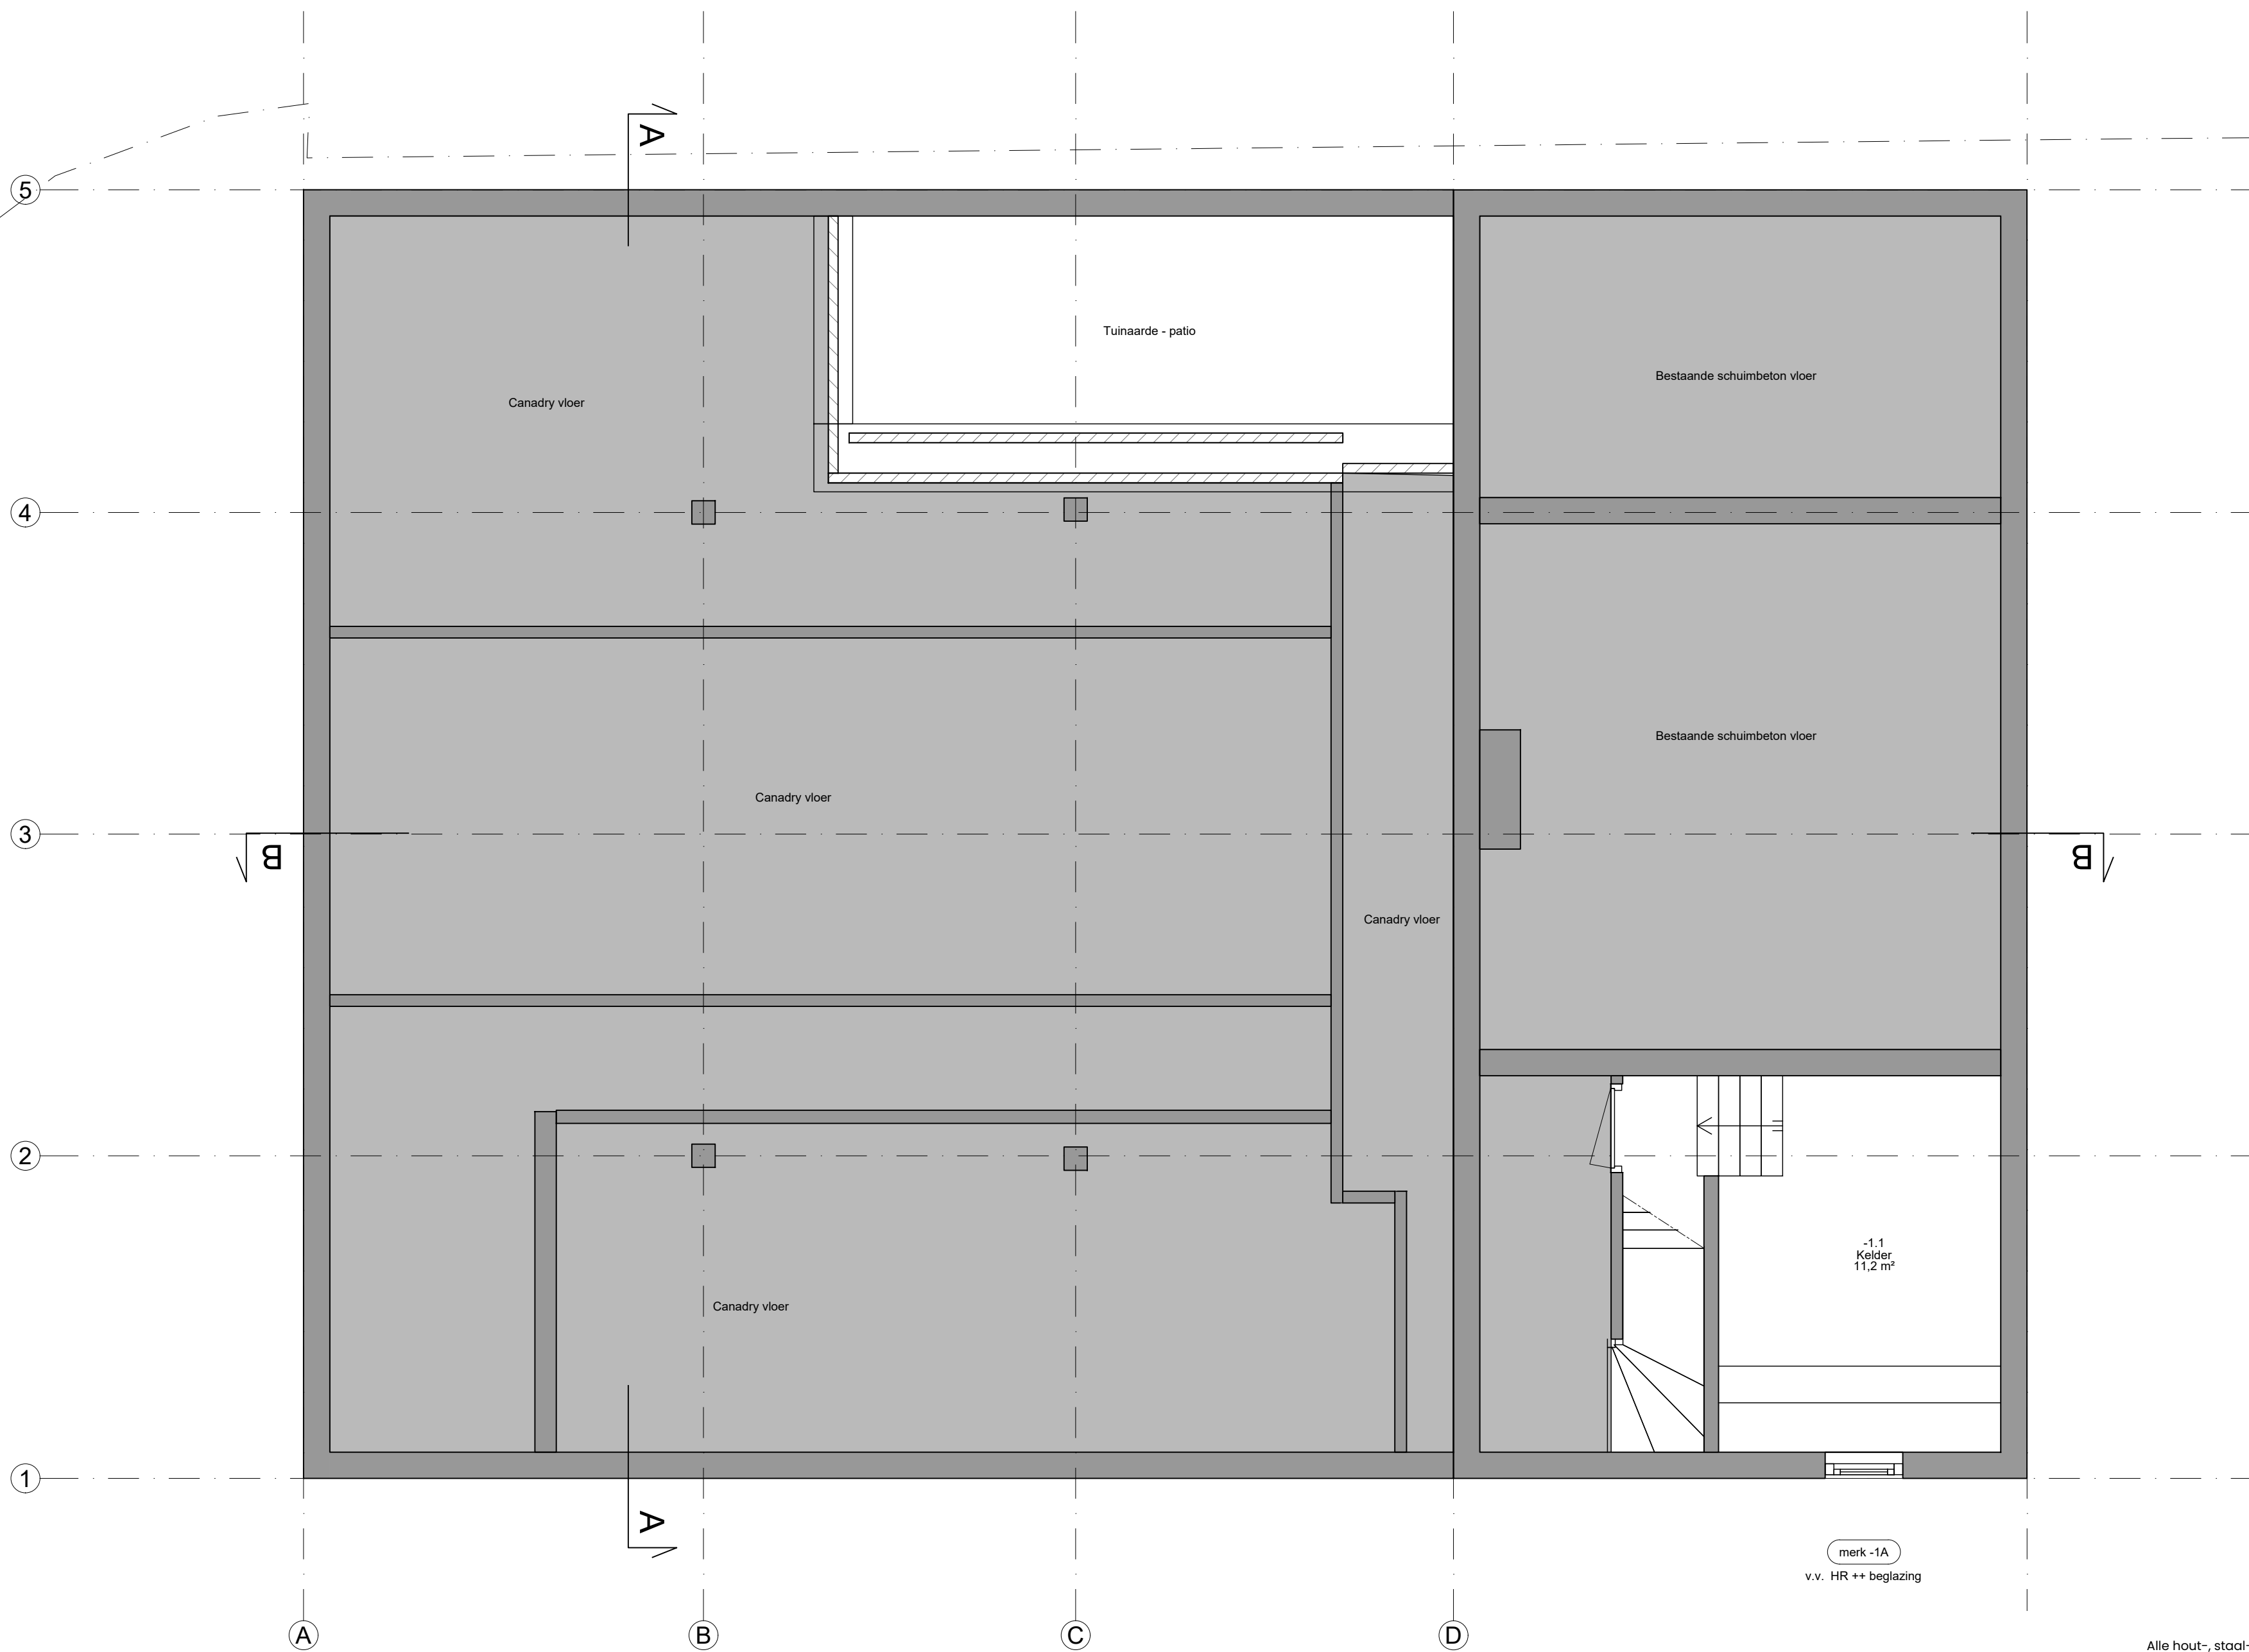

Alle maatvoering in het werk te controleren.
Alle hout-, staal- & betonconstructies volgens constructeur.


Plattegrond Kelder en fundering

project: Verduurzaming en verbouwing | Buzziburglaan 16 | 3972 EE Driebergen
fase: Definitief ontwerp schaal: 1:50 op A2
datum: 03-07-2026 | TtK wijziging:

25-03.DO.11-1

Kraal architecten BV | Vossegatselaan 32 | 3583 RT Utrecht | 030 223 96 77
www.kraalarchitecten.nl | info@kraalarchitecten.nl



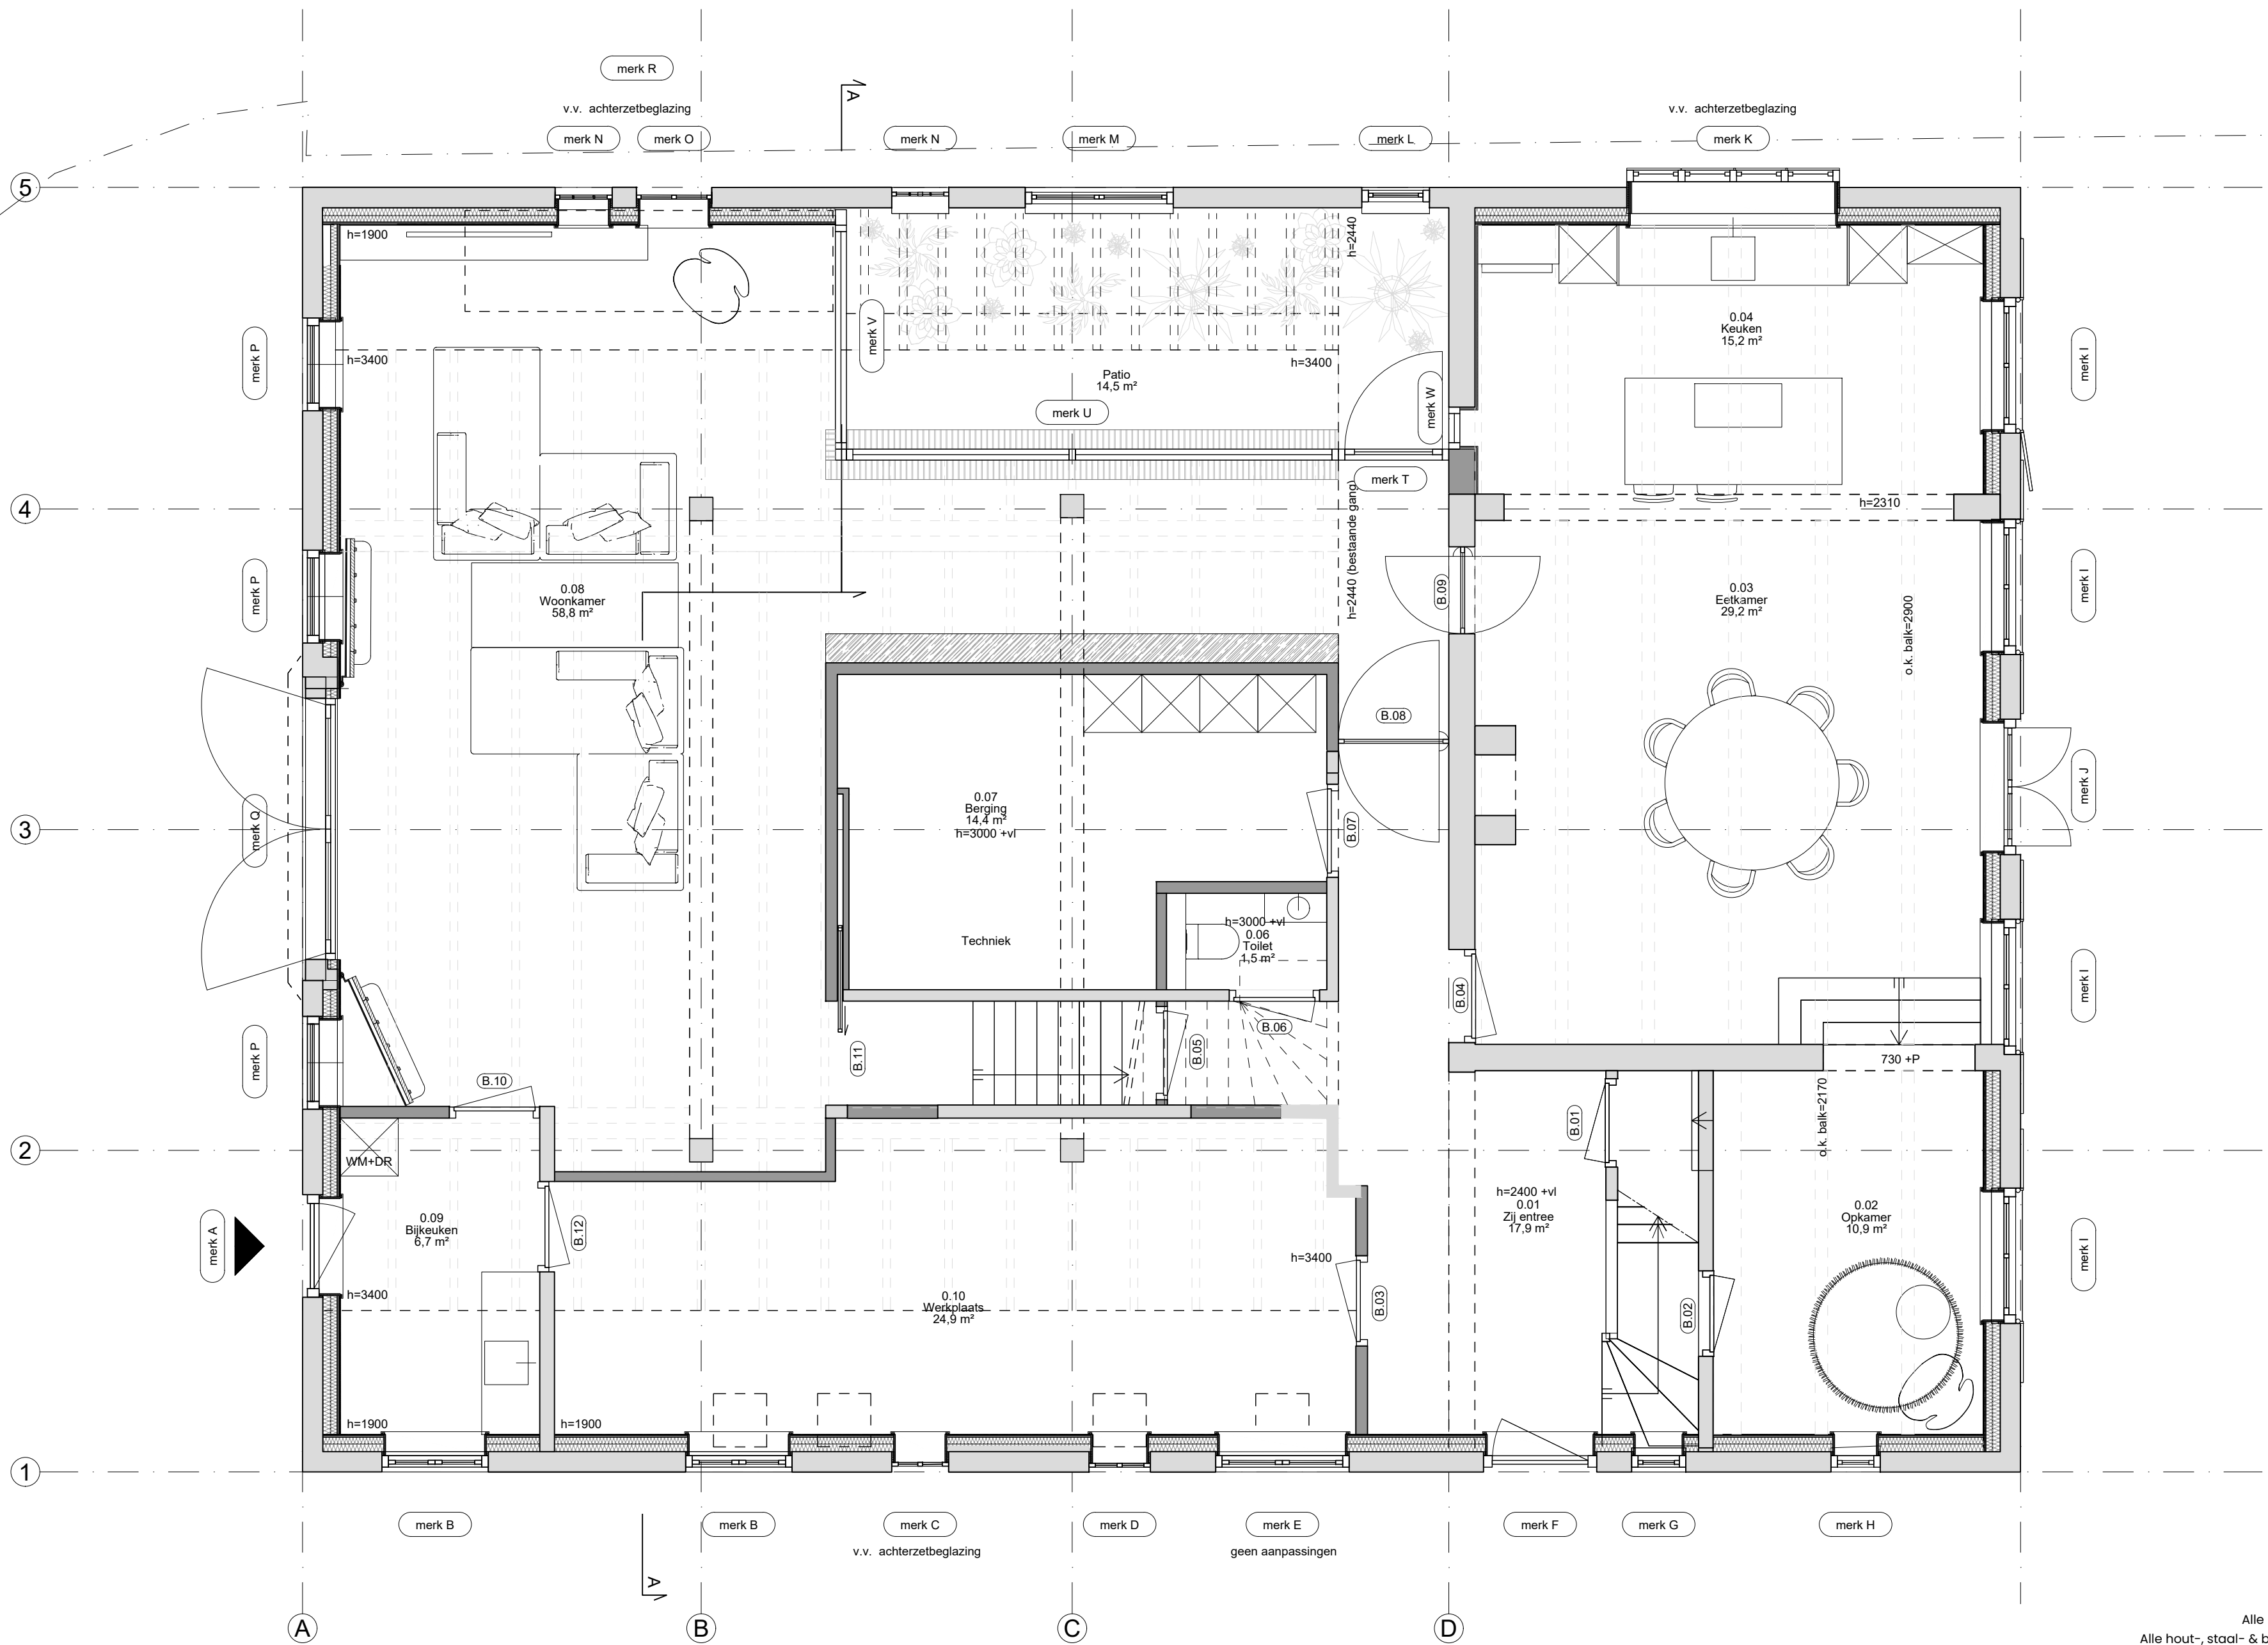

Alle maatvoering in het werk te controleren.
Alle hout-, staal- & betonconstructies volgens constructeur.


Plattegrond begane grond

project: Verduurzaming en verbouwing | Buzziburglaan 16 | 3972 EE Driebergen
fase: Definitief ontwerp schaal: 1:50 op A2
datum: 03-07-2026 | TtK wijziging:

25-03.DO.110

Kraal architecten BV | Vossegatselaan 32 | 3583 RT Utrecht | 030 223 96 77
www.kraalarchitecten.nl | info@kraalarchitecten.nl



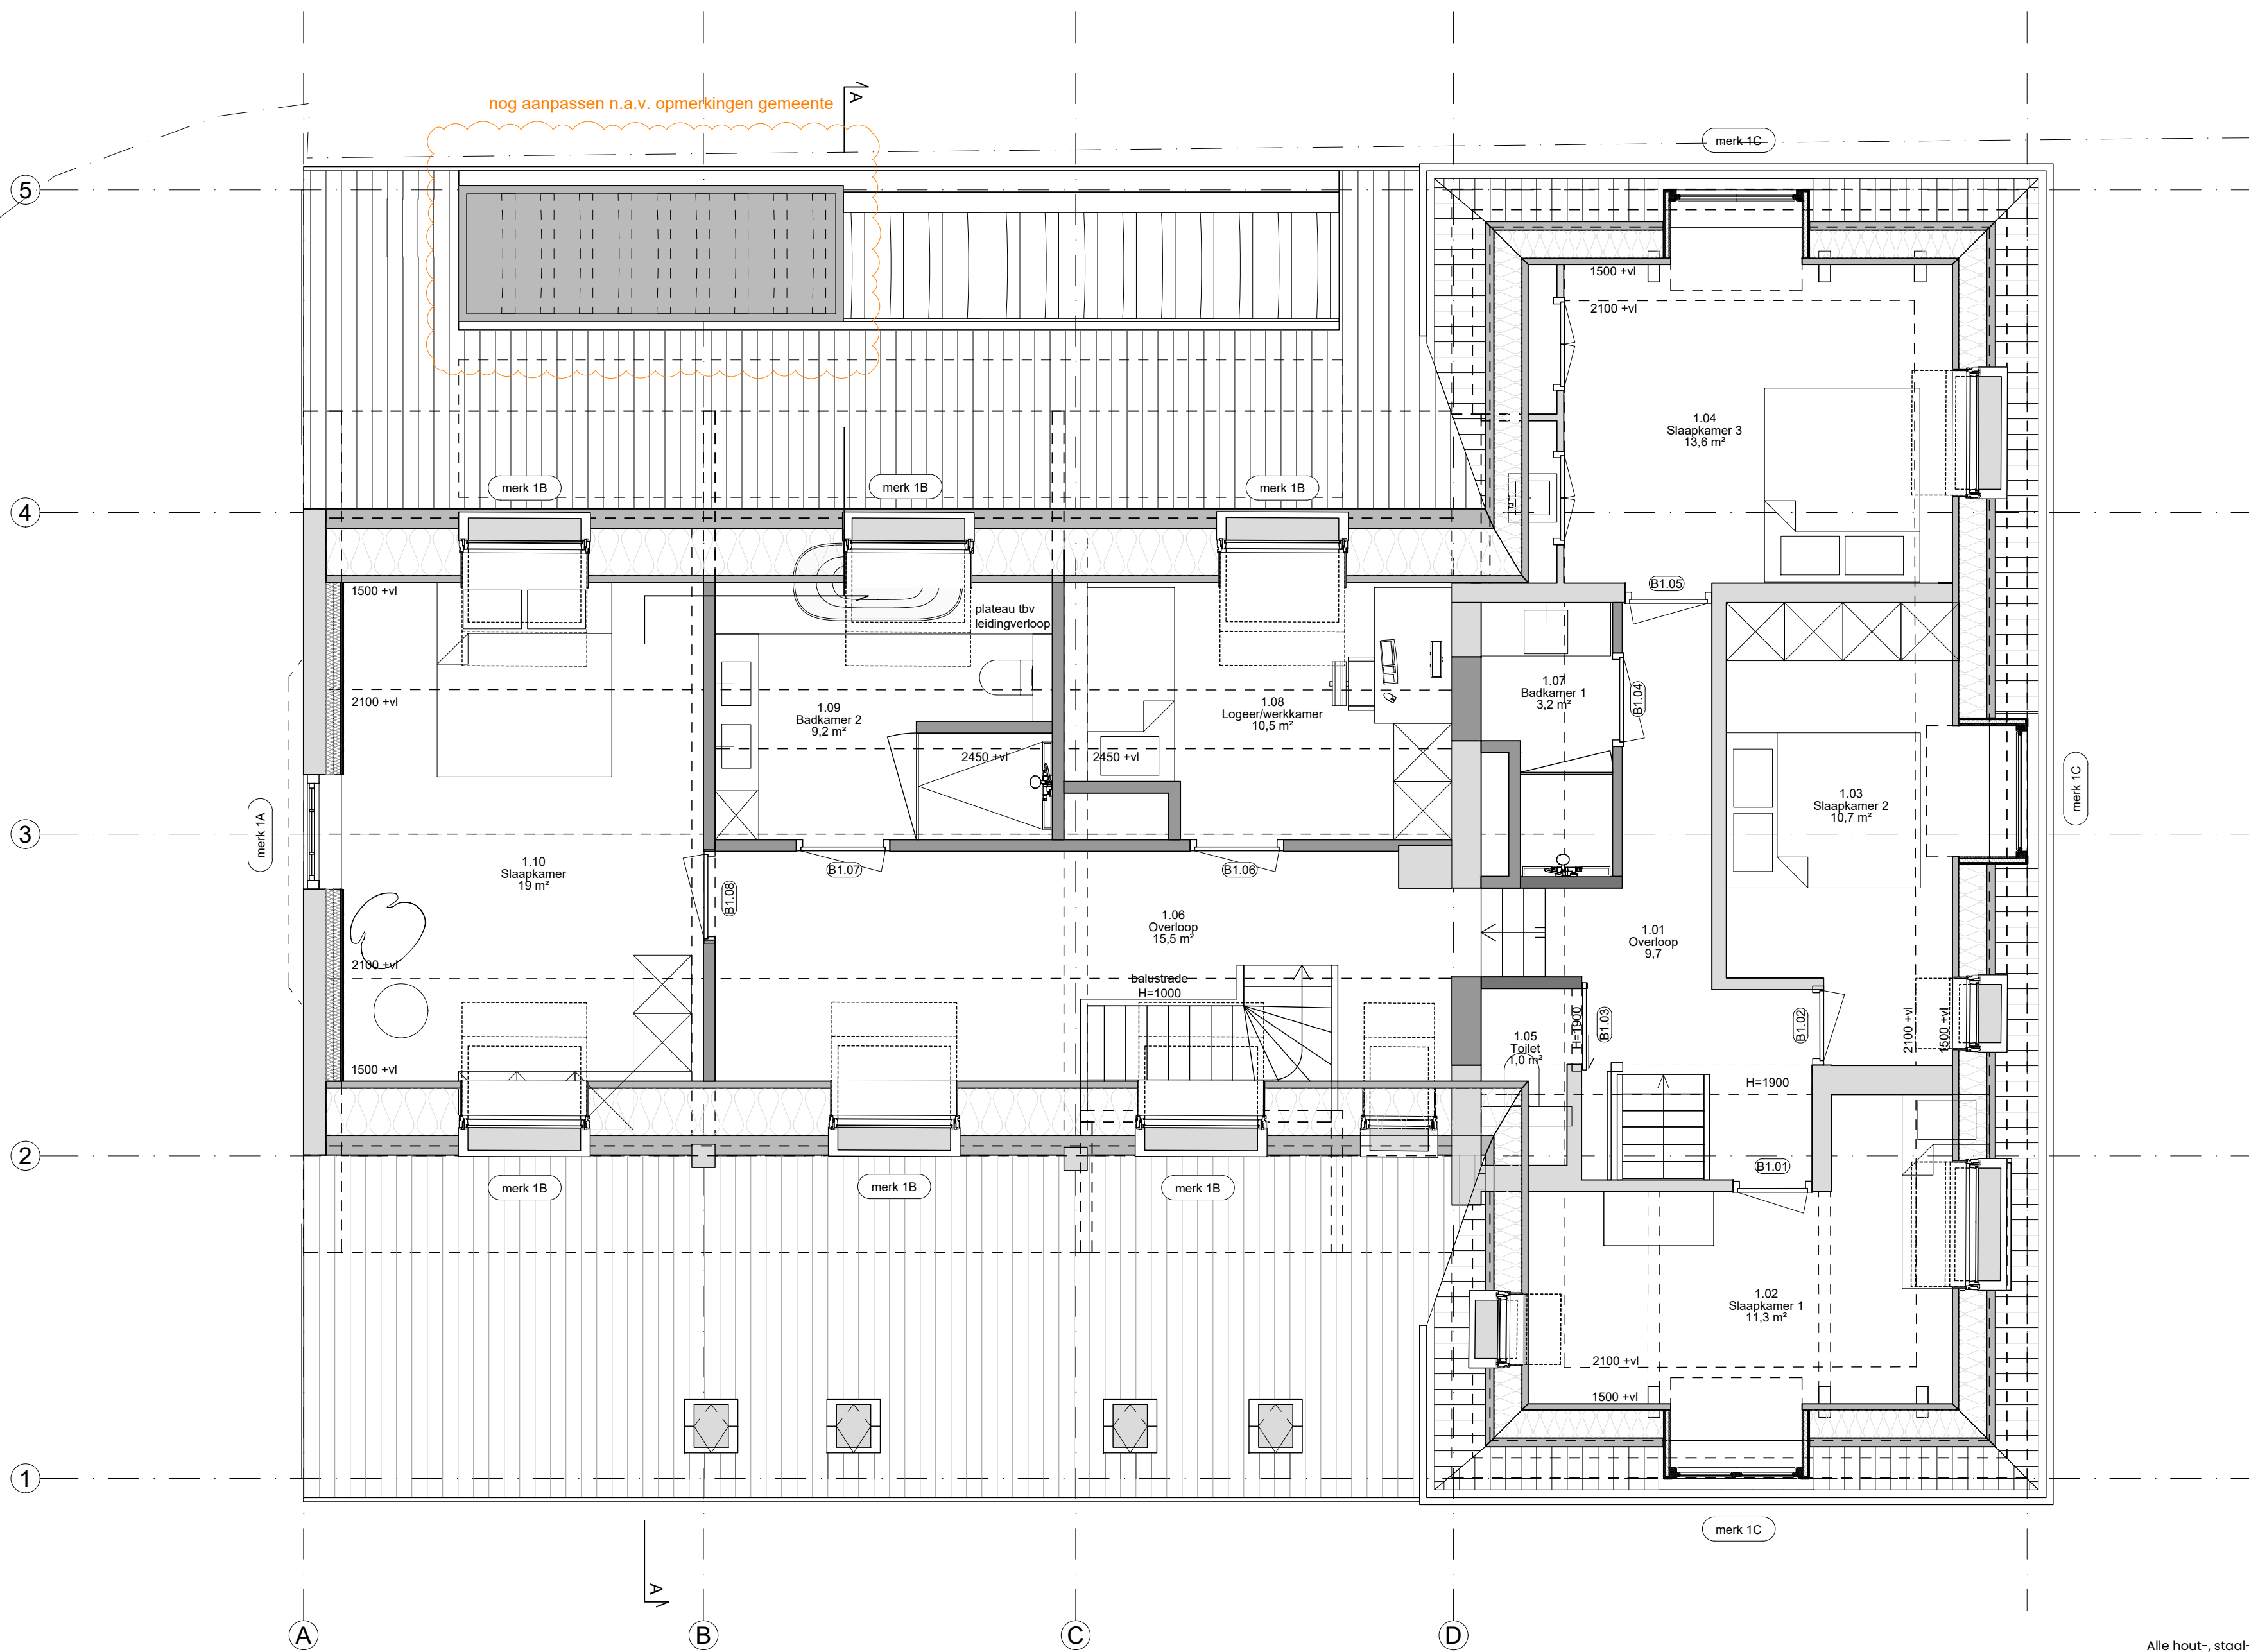

Alle maatvoering in het werk te controleren.
Alle hout-, staal- & betonconstructies volgens constructeur.


Plattegrond 1e verdieping

project: Verduurzaming en verbouwing | Buzziburglaan 16 | 3972 EE Driebergen
fase: Definitief ontwerp schaal: 1:50 op A2
datum: 03-07-2026 | TtK wijziging:

25-03.DO.111

Kraal architecten BV | Vossegatselaan 32 | 3583 RT Utrecht | 030 223 96 77
www.kraalarchitecten.nl | info@kraalarchitecten.nl



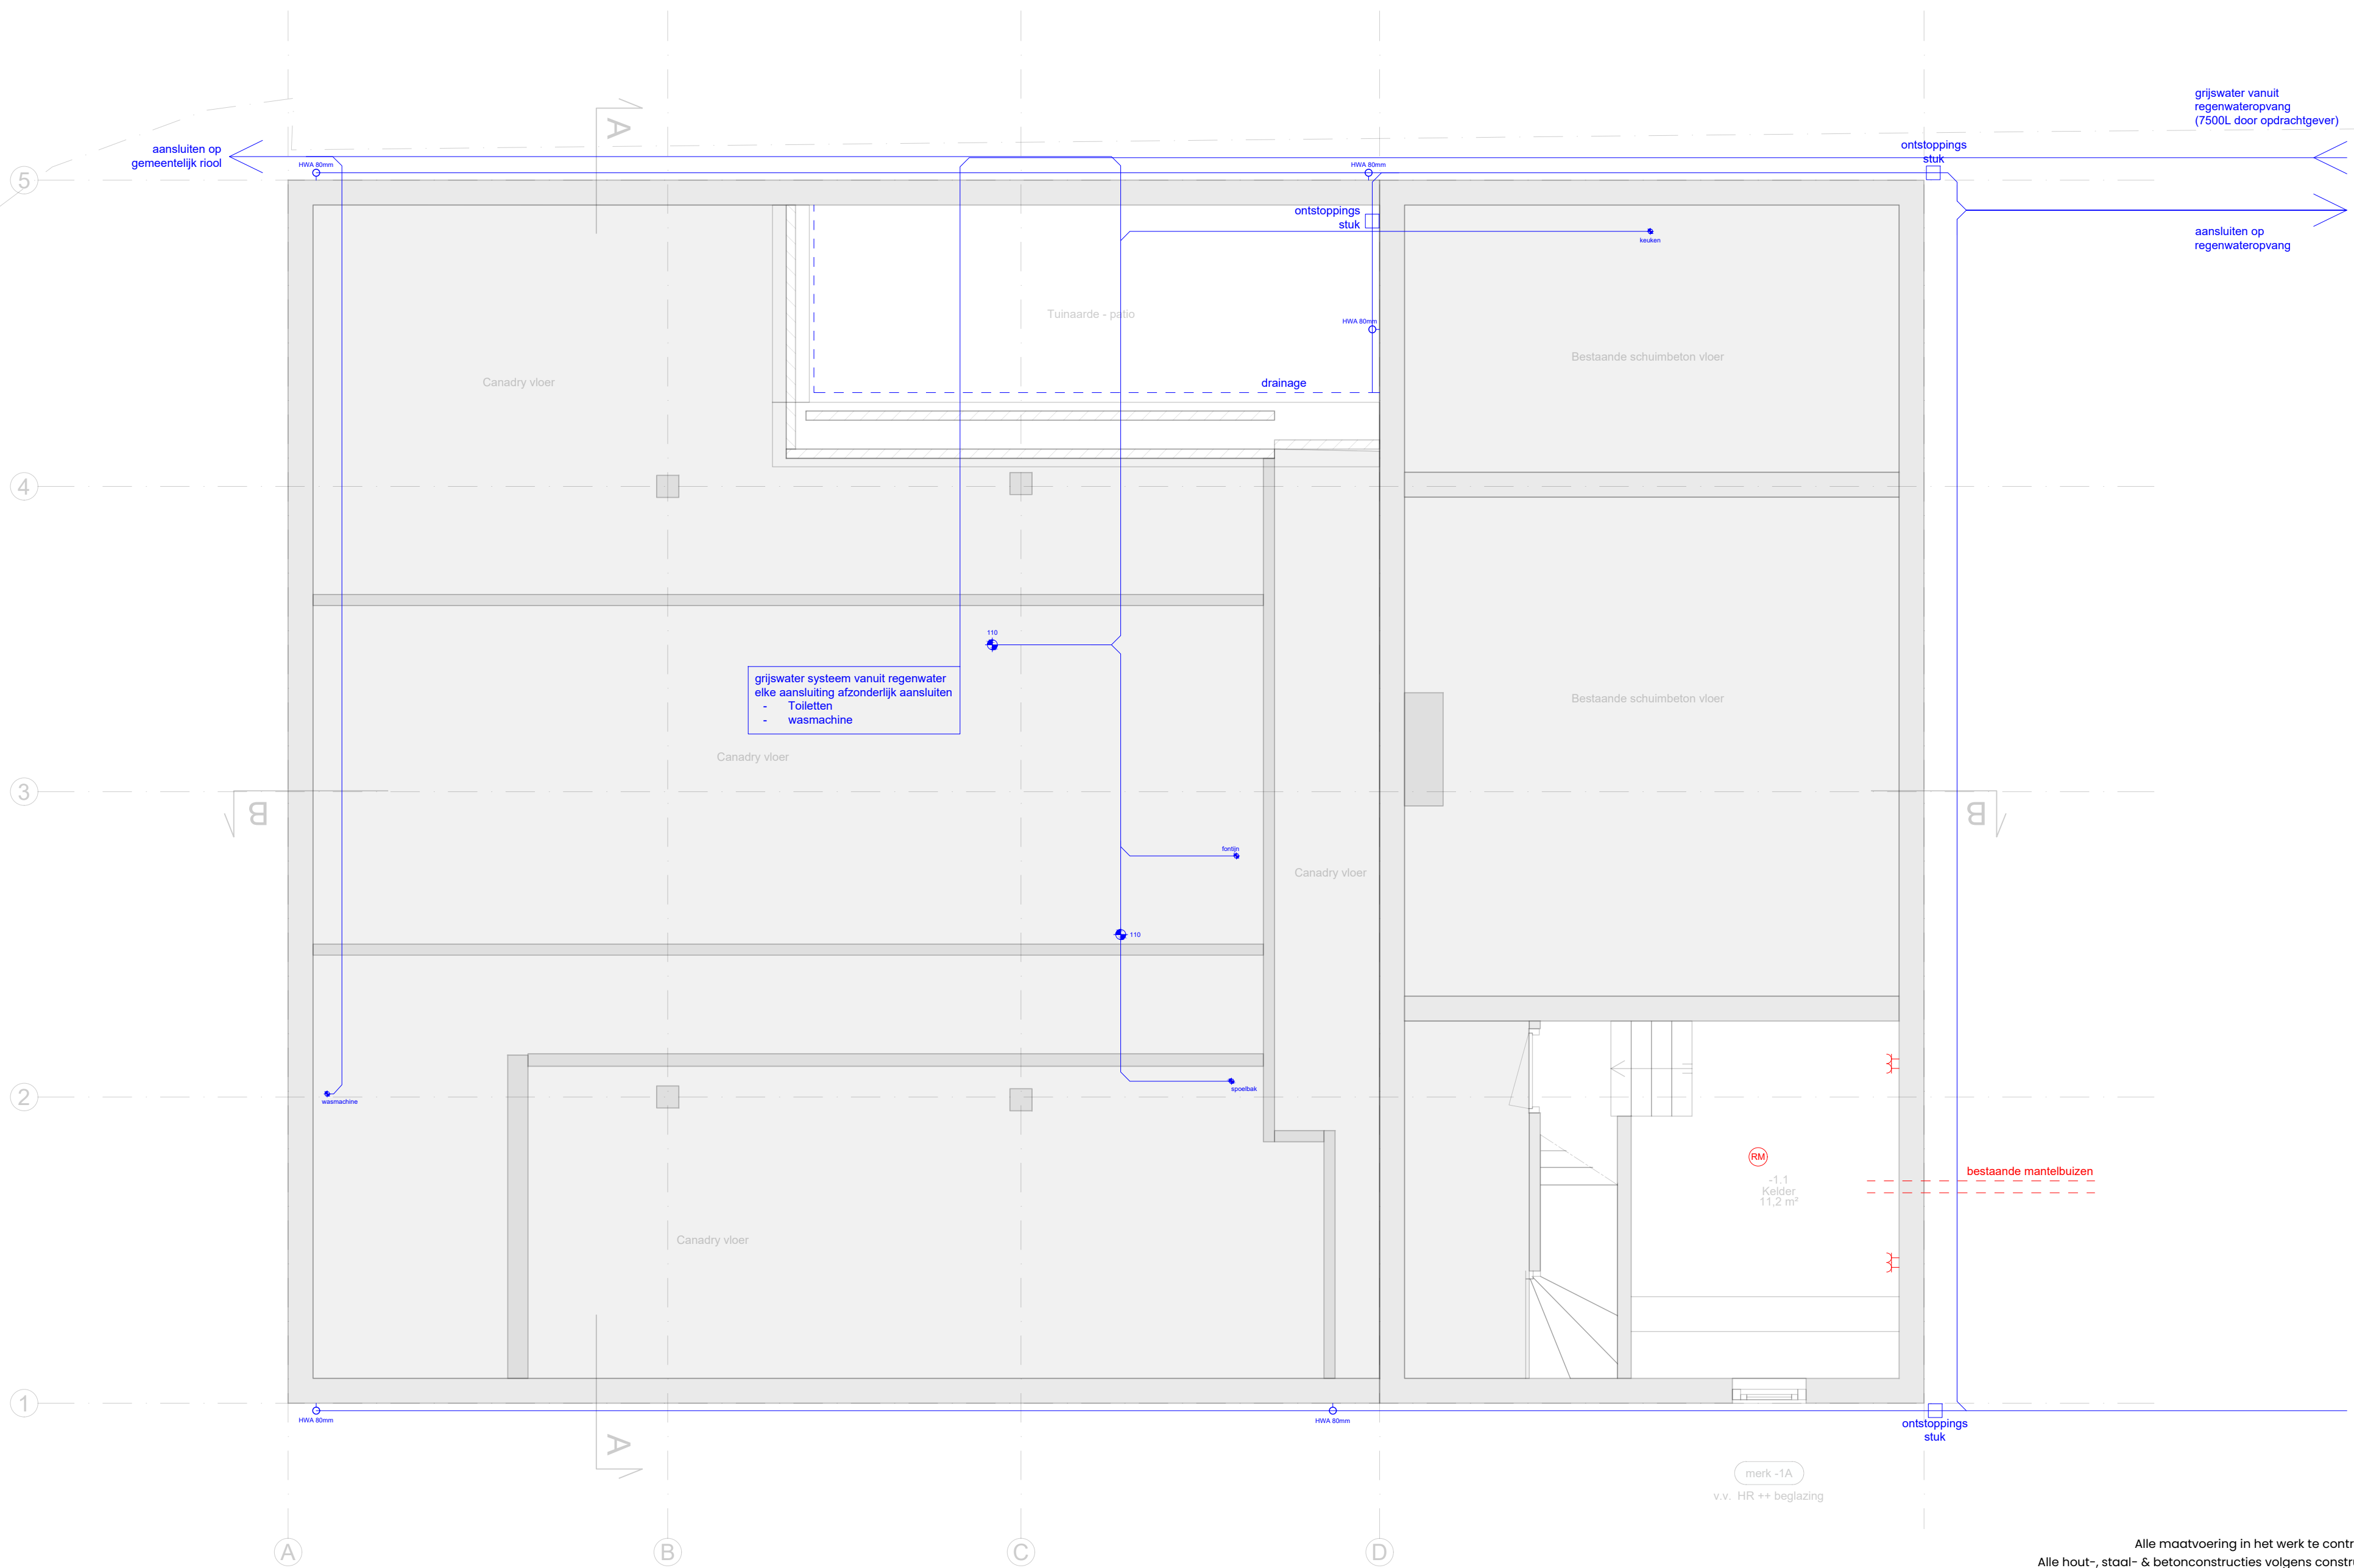

Alle maatvoering in het werk te controleren.
Alle hout-, staal- & betonconstructies volgens constructeur.


Plattegrond installaties | Kelder en fundering

project: Verduurzaming en verbouwing | Buzziburglaan 16 | 3972 EE Driebergen
fase: Definitief ontwerp schaal: 1:50 op A2
datum: 03-07-2026 | TtK wijziging:

25-03.DO.81-1

Kraal architecten BV | Vossegatselaan 32 | 3583 RT Utrecht | 030 223 96 77
www.kraalarchitecten.nl | info@kraalarchitecten.nl



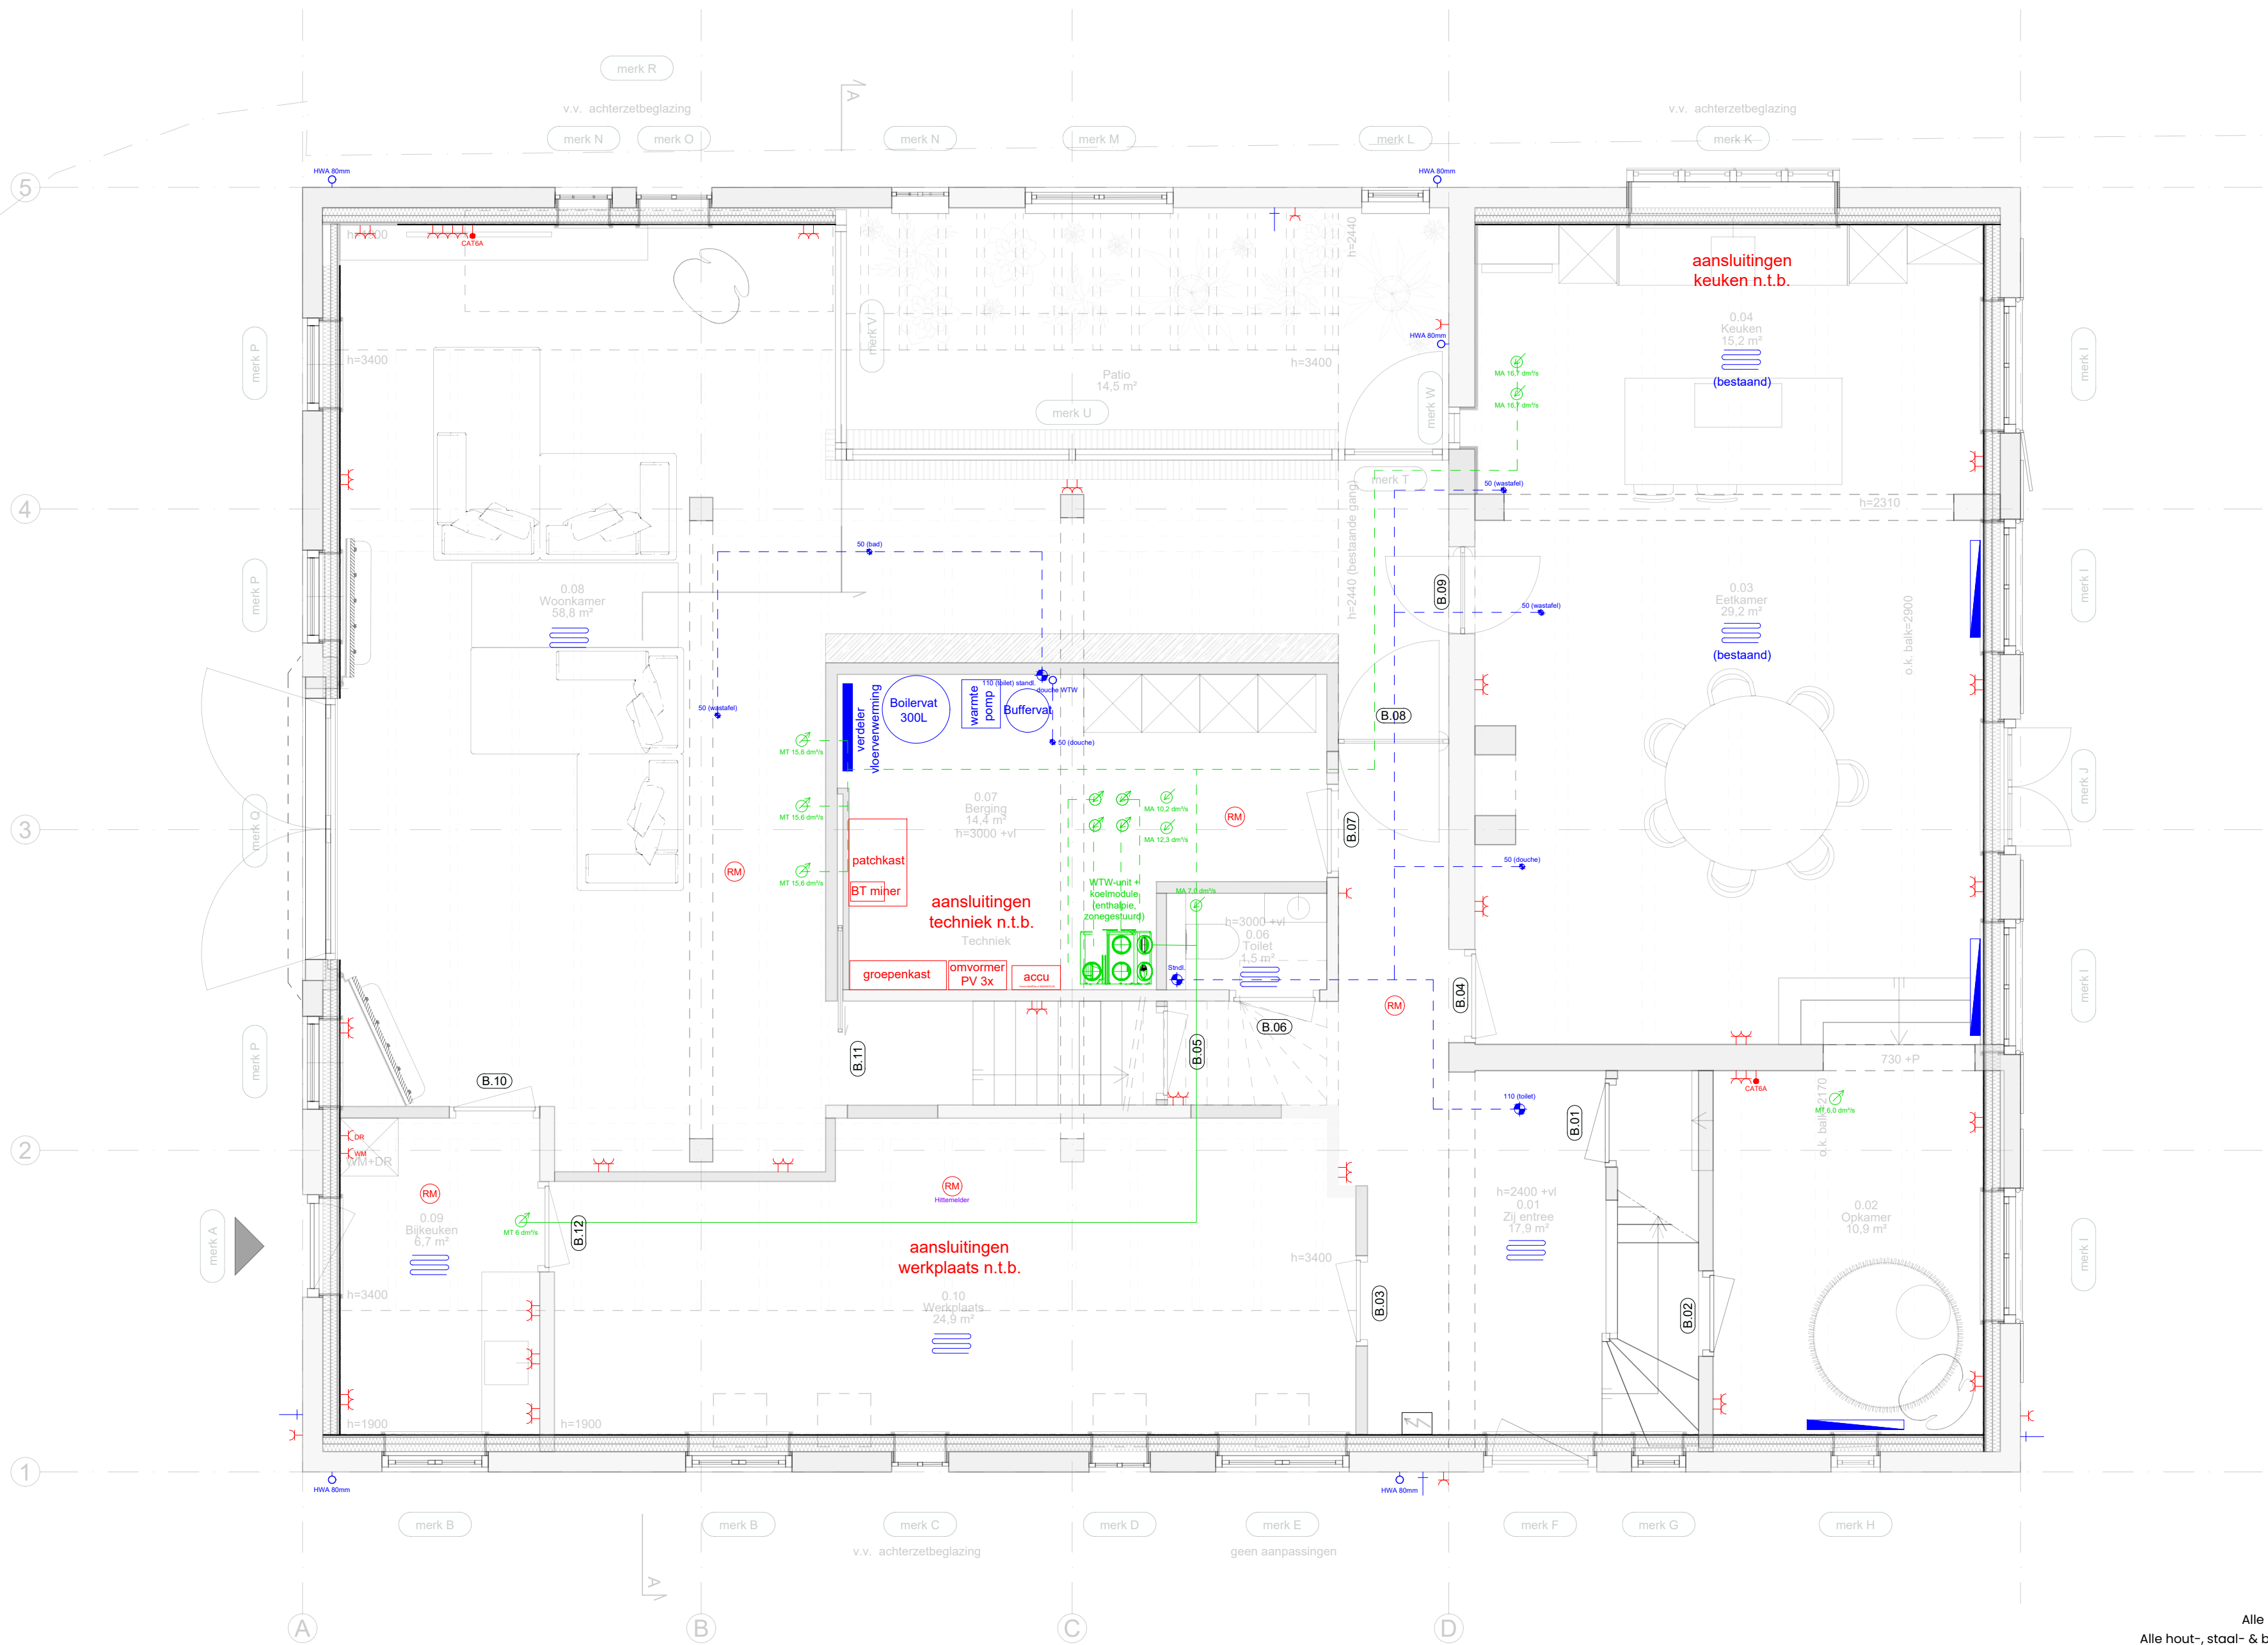

Alle maatvoering in het werk te controleren.
Alle hout-, staal- & betonconstructies volgens constructeur.


Plattegrond installaties | begane grond

project: Verduurzaming en verbouwing | Buzziburglaan 16 | 3972 EE Driebergen
fase: Definitief ontwerp schaal: 1:50 op A2
datum: 03-07-2026 | TtK wijziging:

25-03.DO.810

Kraal architecten BV | Vossegatselaan 32 | 3583 RT Utrecht | 030 223 96 77
www.kraalarchitecten.nl | info@kraalarchitecten.nl



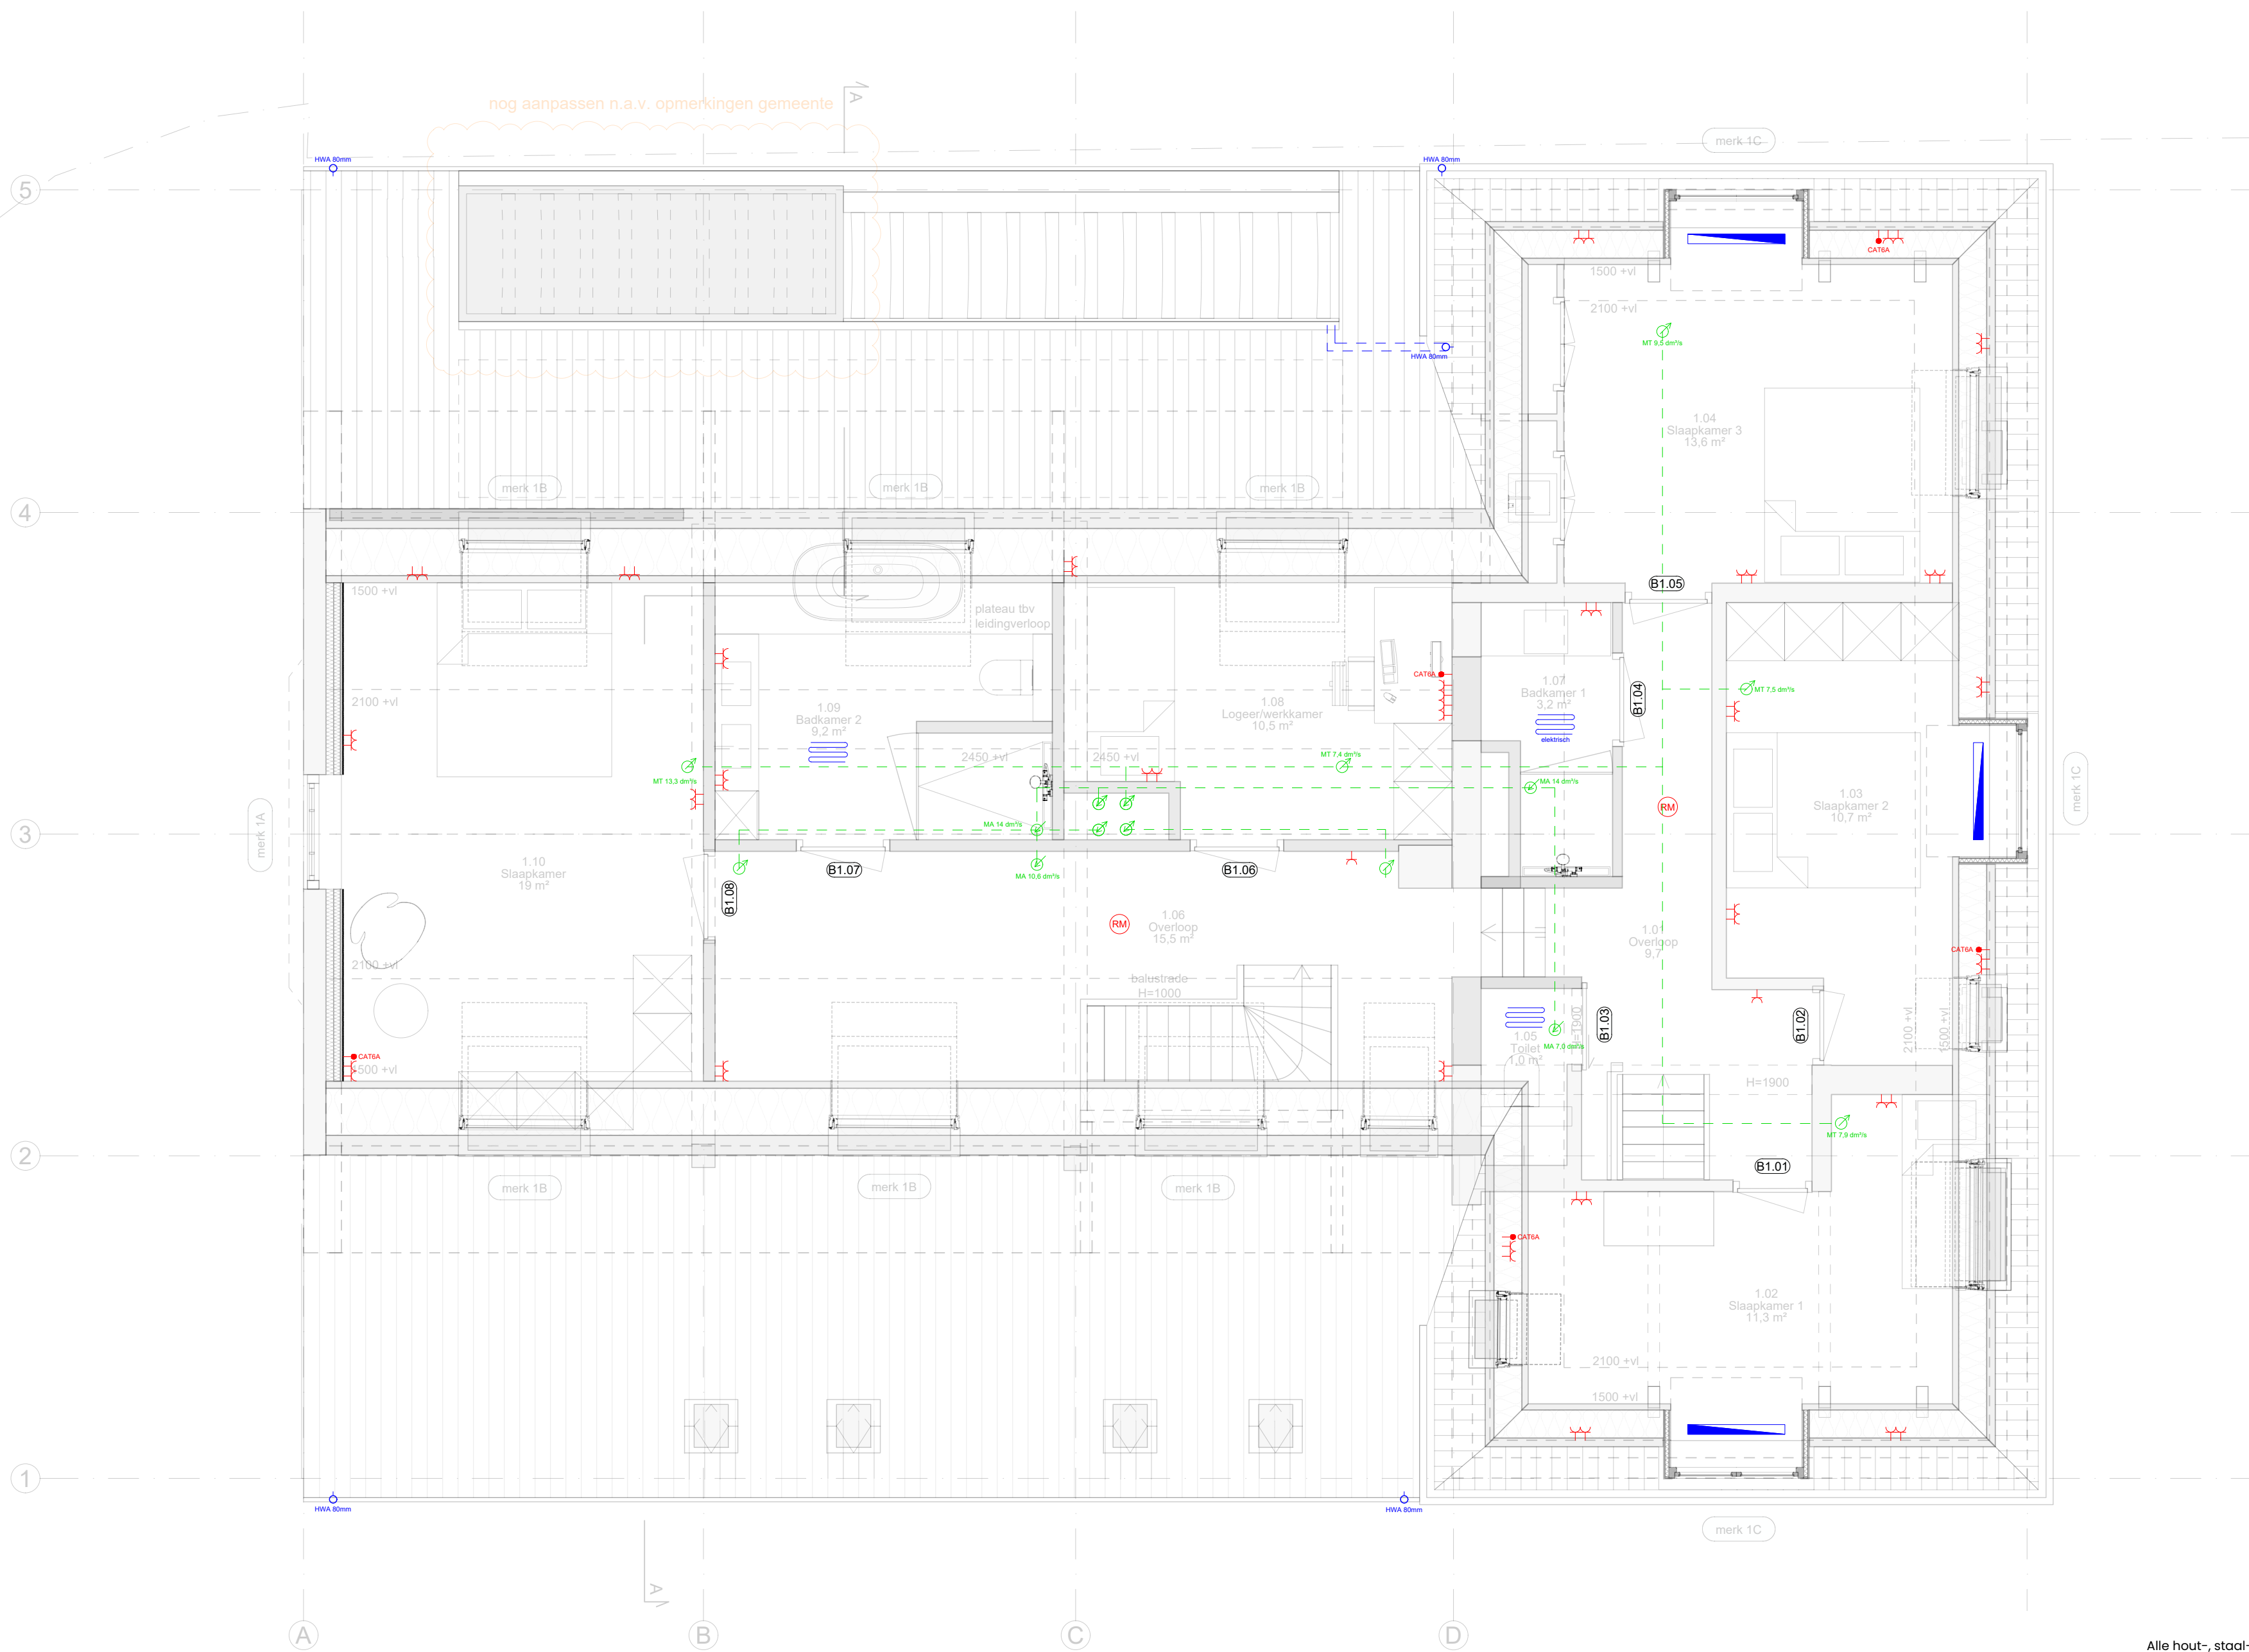

Alle maatvoering in het werk te controleren.
Alle hout-, staal- & betonconstructies volgens constructeur.


Plattegrond installaties | 1e verdieping

project: Verduurzaming en verbouwing | Buzziburglaan 16 | 3972 EE Driebergen
fase: Definitief ontwerp schaal: 1:50 op A2
datum: 03-07-2026 | TtK wijziging:

25-03.DO.811

Kraal architecten BV | Vossegatselaan 32 | 3583 RT Utrecht | 030 223 96 77
www.kraalarchitecten.nl | info@kraalarchitecten.nl



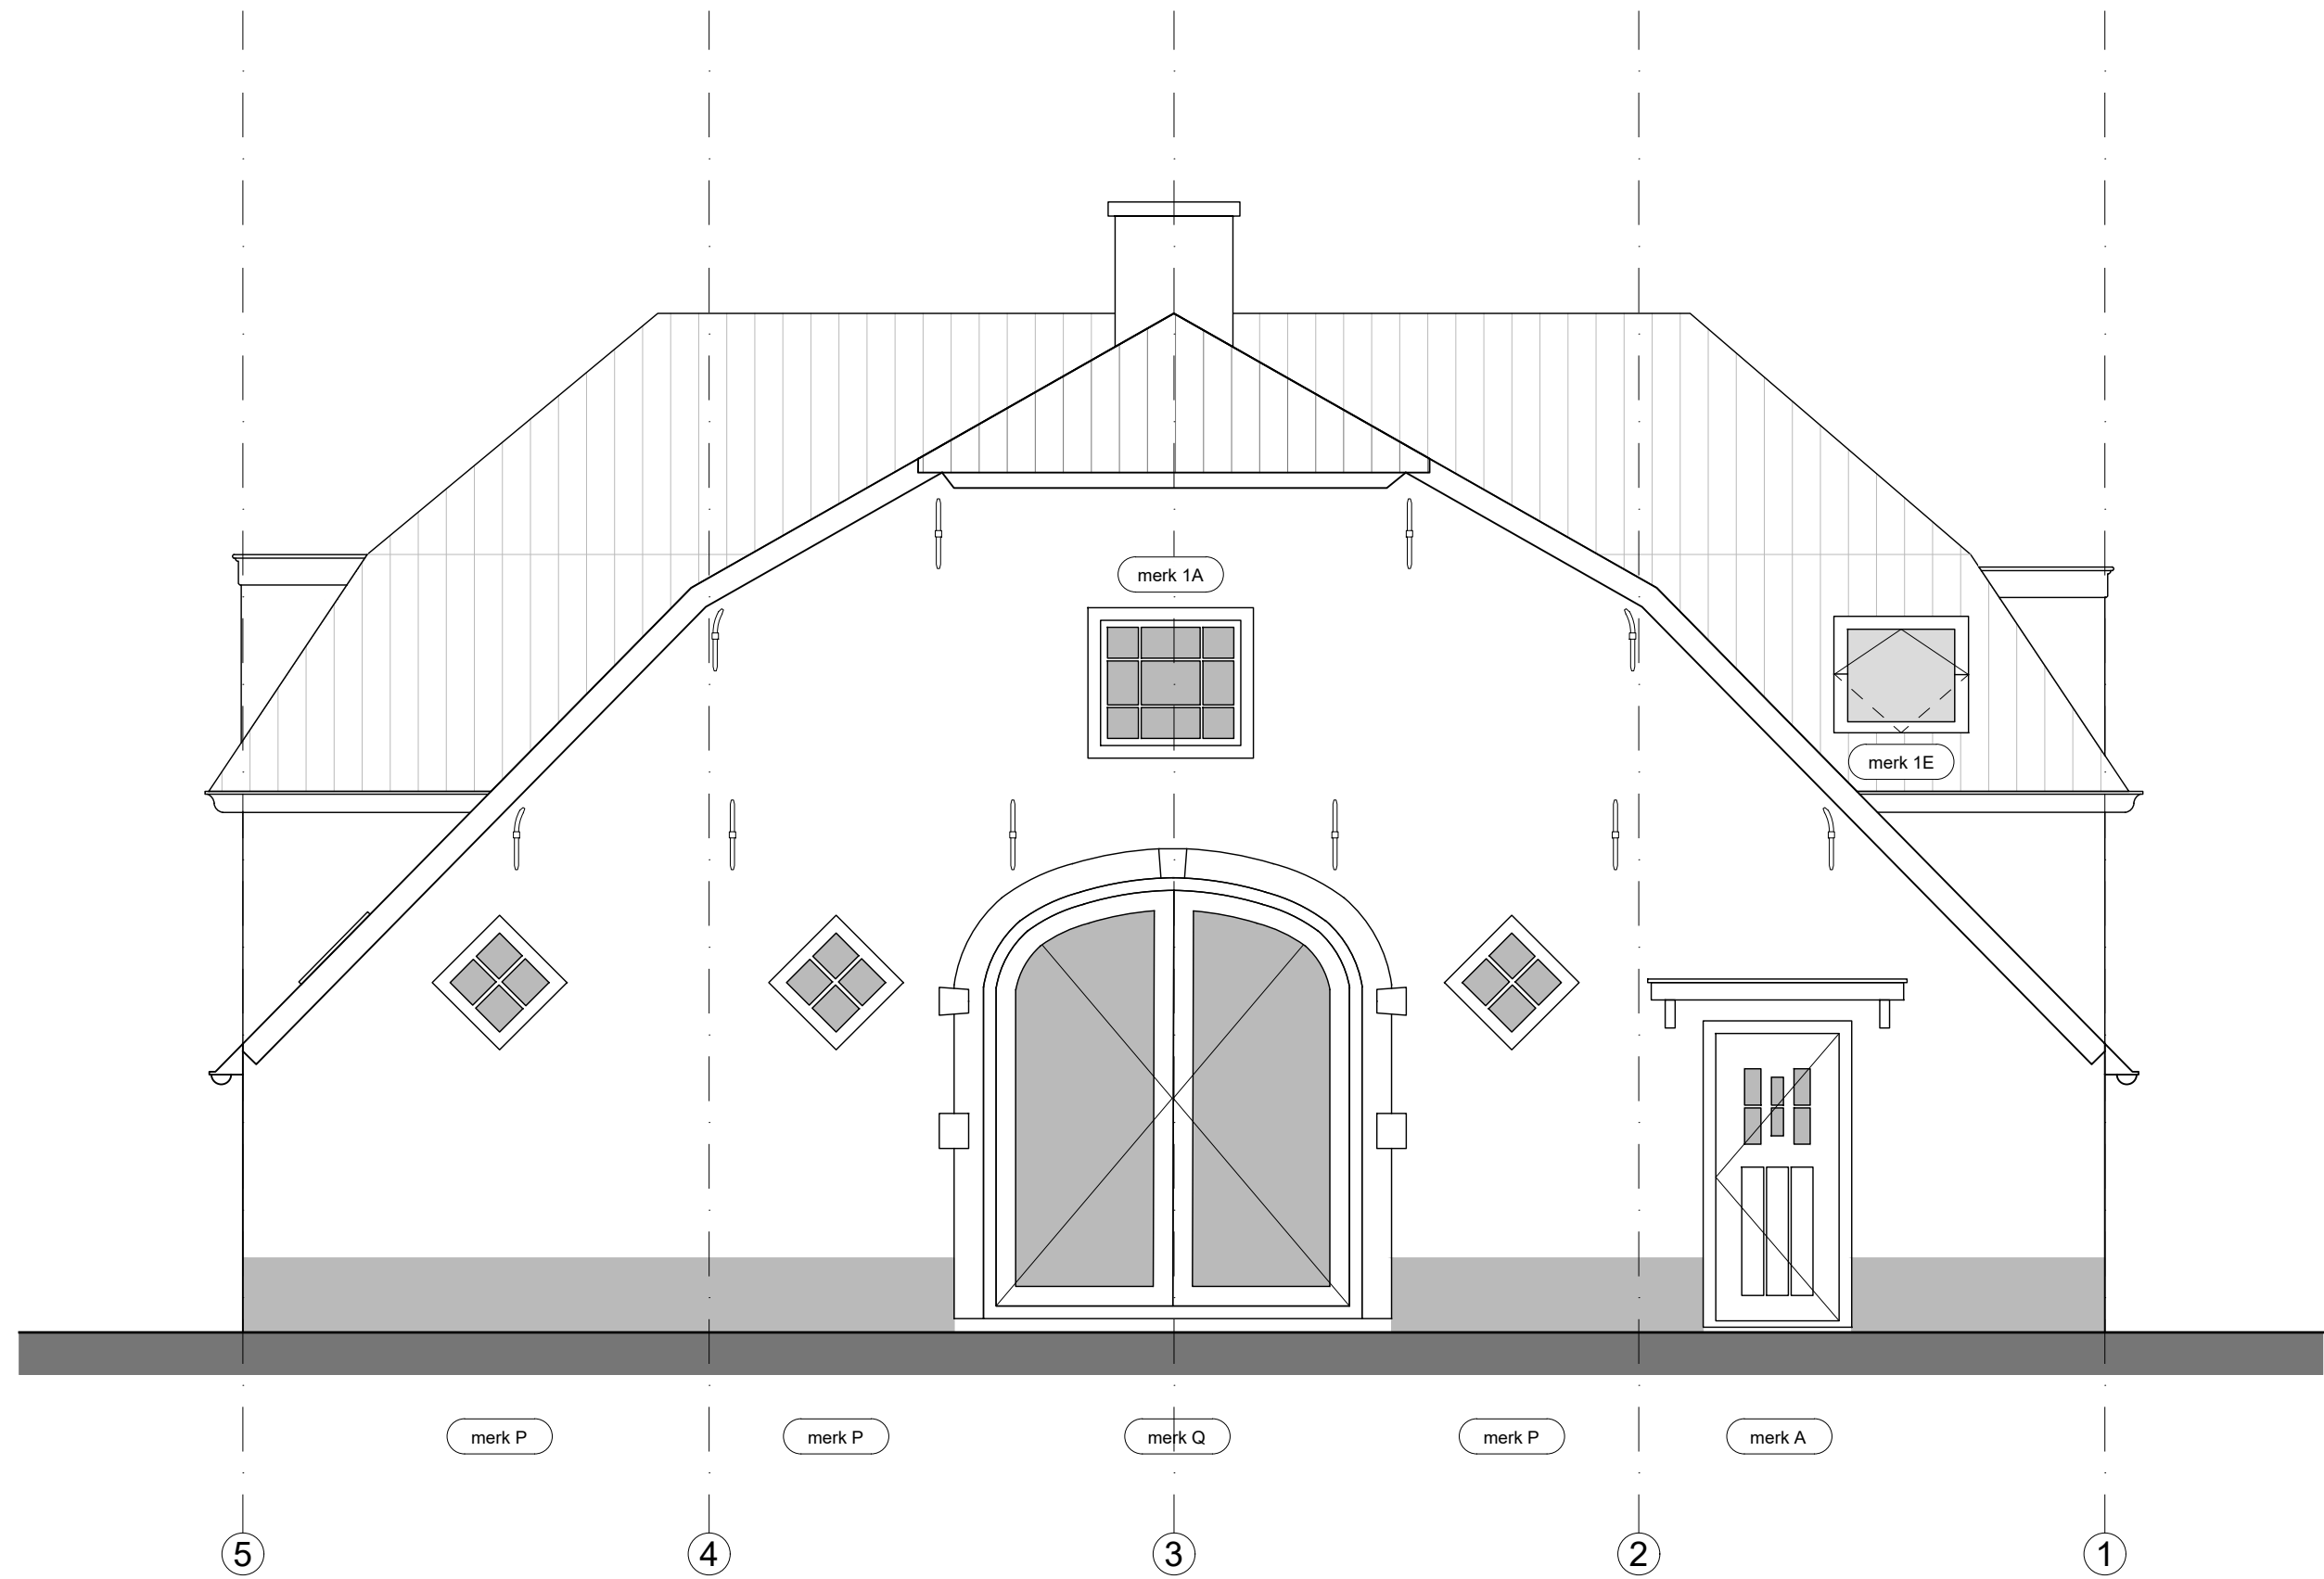

VOORGEVEL

Alle maatvoering in het werk te controleren.
Alle hout-, staal- & betonconstructies volgens constructeur.


Aanzicht voorgevel

project: Verduurzaming en verbouwing | Buzziburglaan 16 | 3972 EE Driebergen
fase: Definitief ontwerp schaal: 1:50 op A2
datum: 03-07-2026 | TtK wijziging:

25-03.DO.210

Kraal architecten BV | Vossegatselaan 32 | 3583 RT Utrecht | 030 223 96 77
www.kraalarchitecten.nl | info@kraalarchitecten.nl



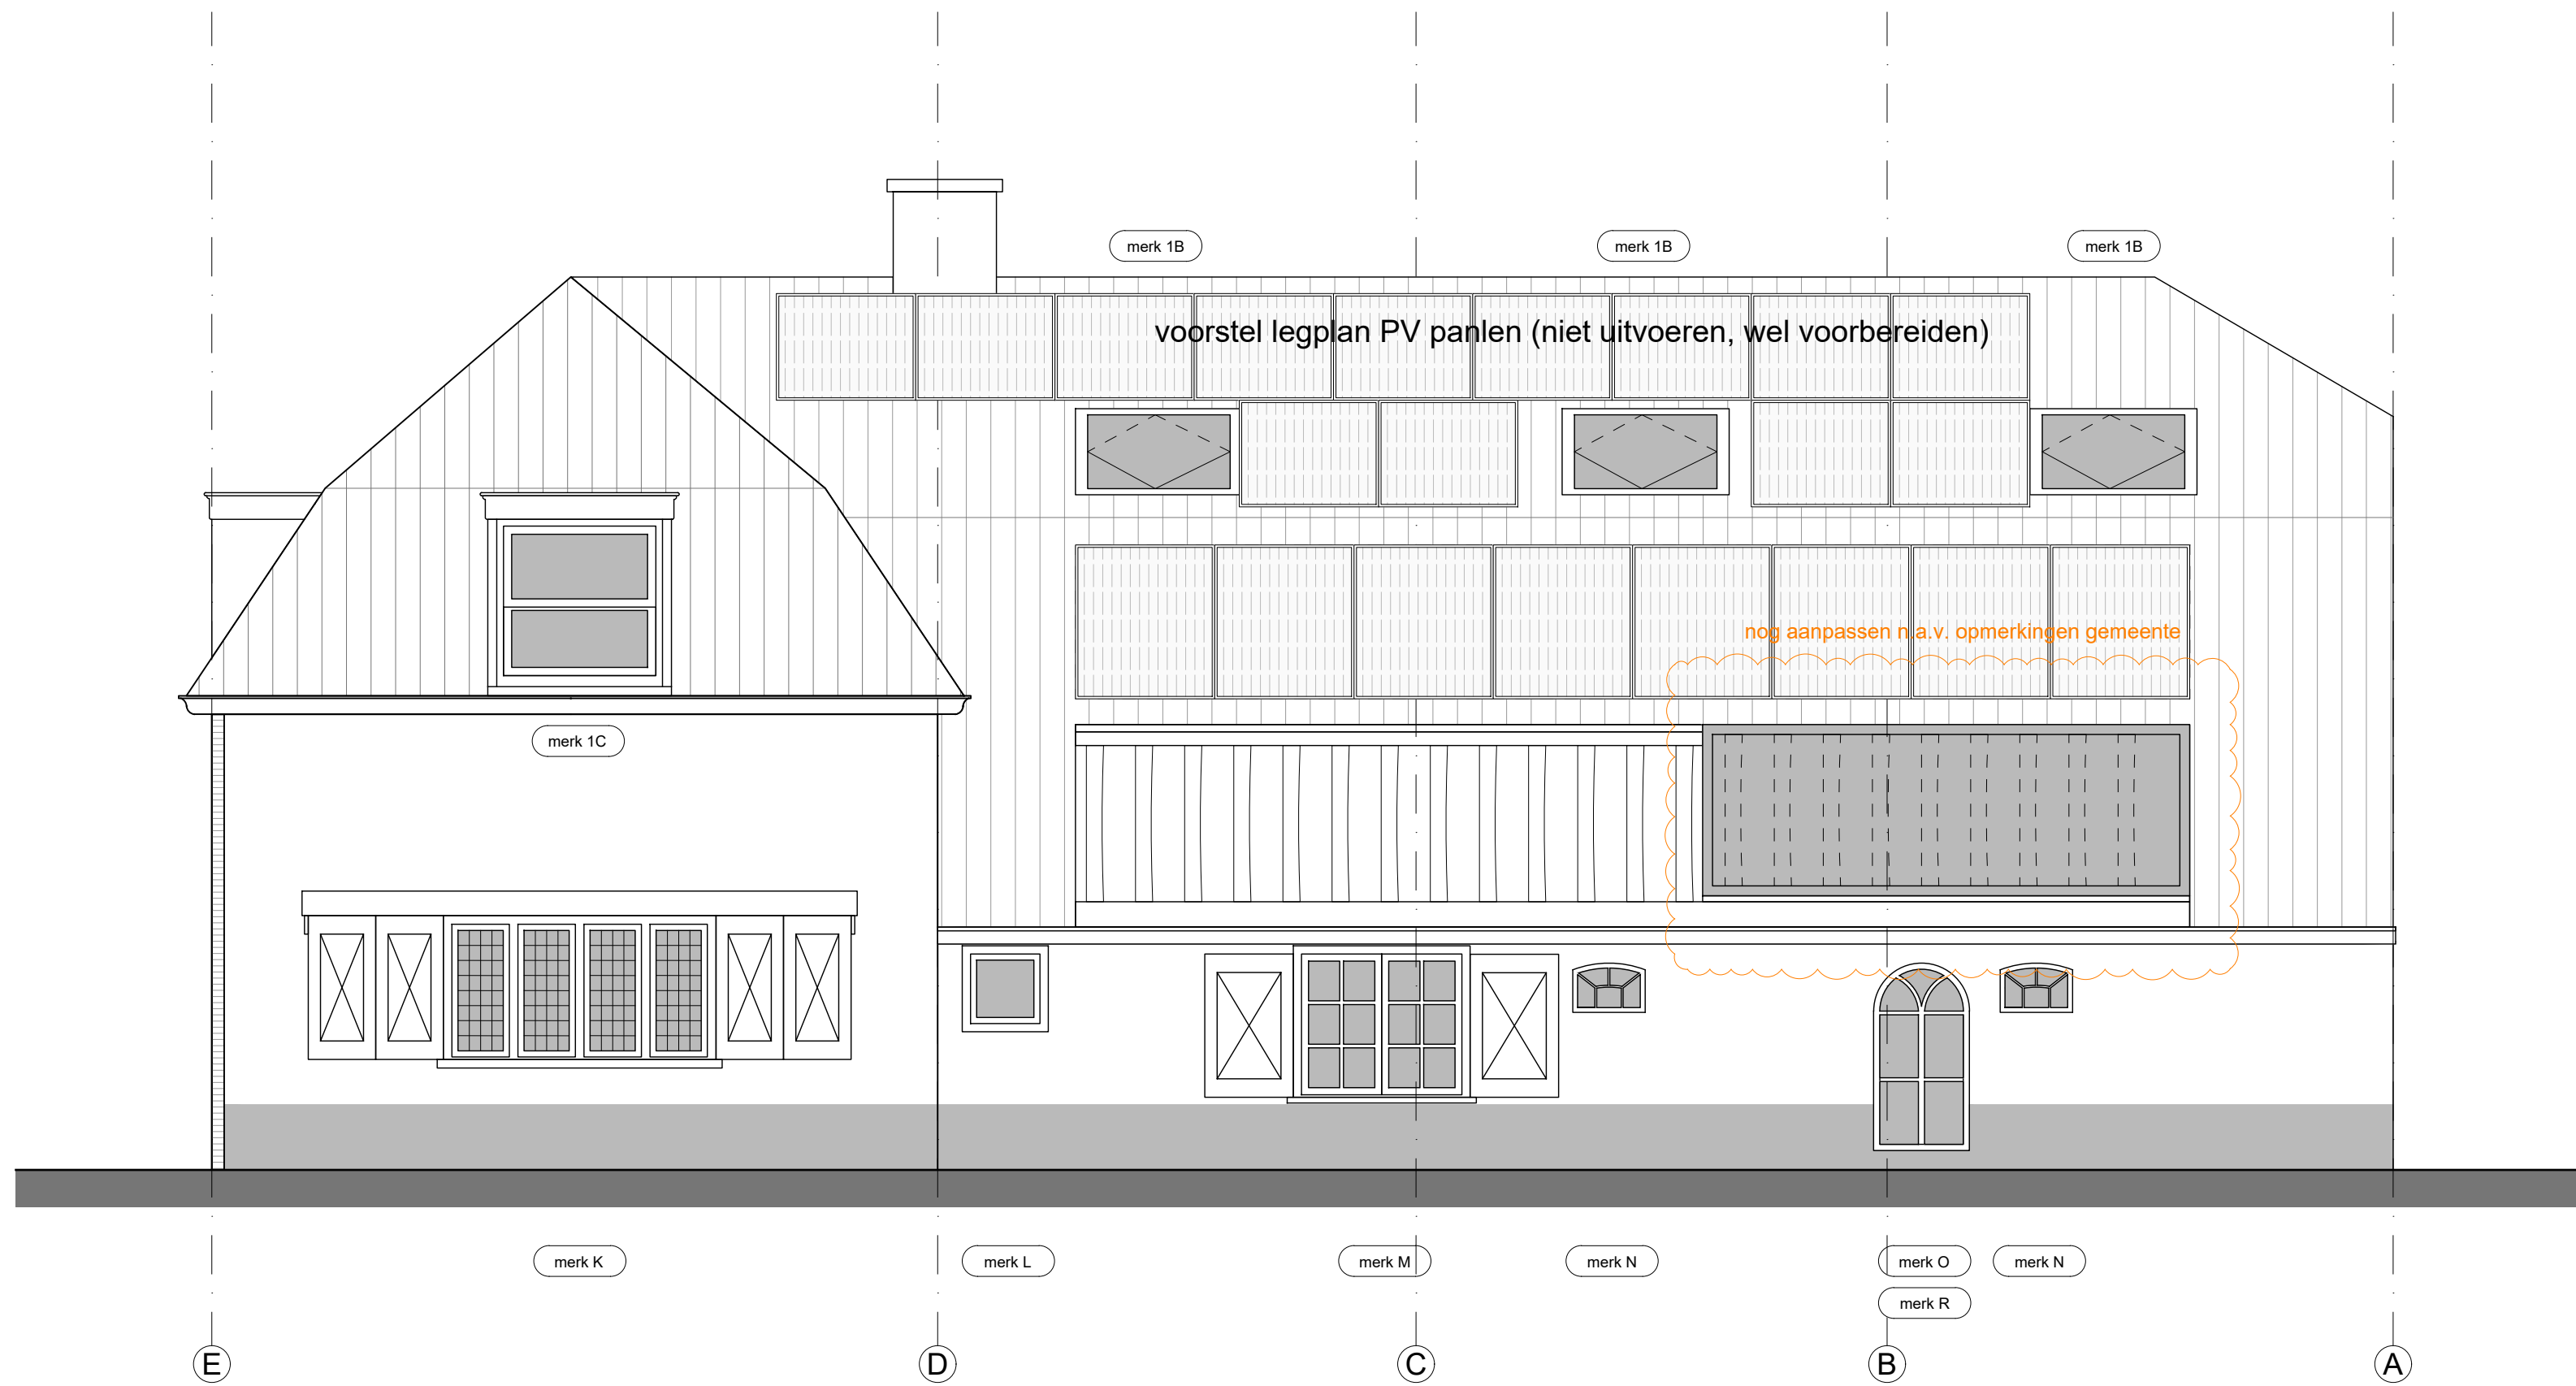

LINKER ZIJGEVEL

Alle maatvoering in het werk te controleren.
Alle hout-, staal- & betonconstructies volgens constructeur.


Aanzicht linker zijgevel

project: Verduurzaming en verbouwing | Buzziburglaan 16 | 3972 EE Driebergen
fase: Definitief ontwerp schaal: 1:50 op A2
datum: 03-07-2026 | TtK wijziging:

25-03.DO.211

Kraal architecten BV | Vossegatselaan 32 | 3583 RT Utrecht | 030 223 96 77
www.kraalarchitecten.nl | info@kraalarchitecten.nl



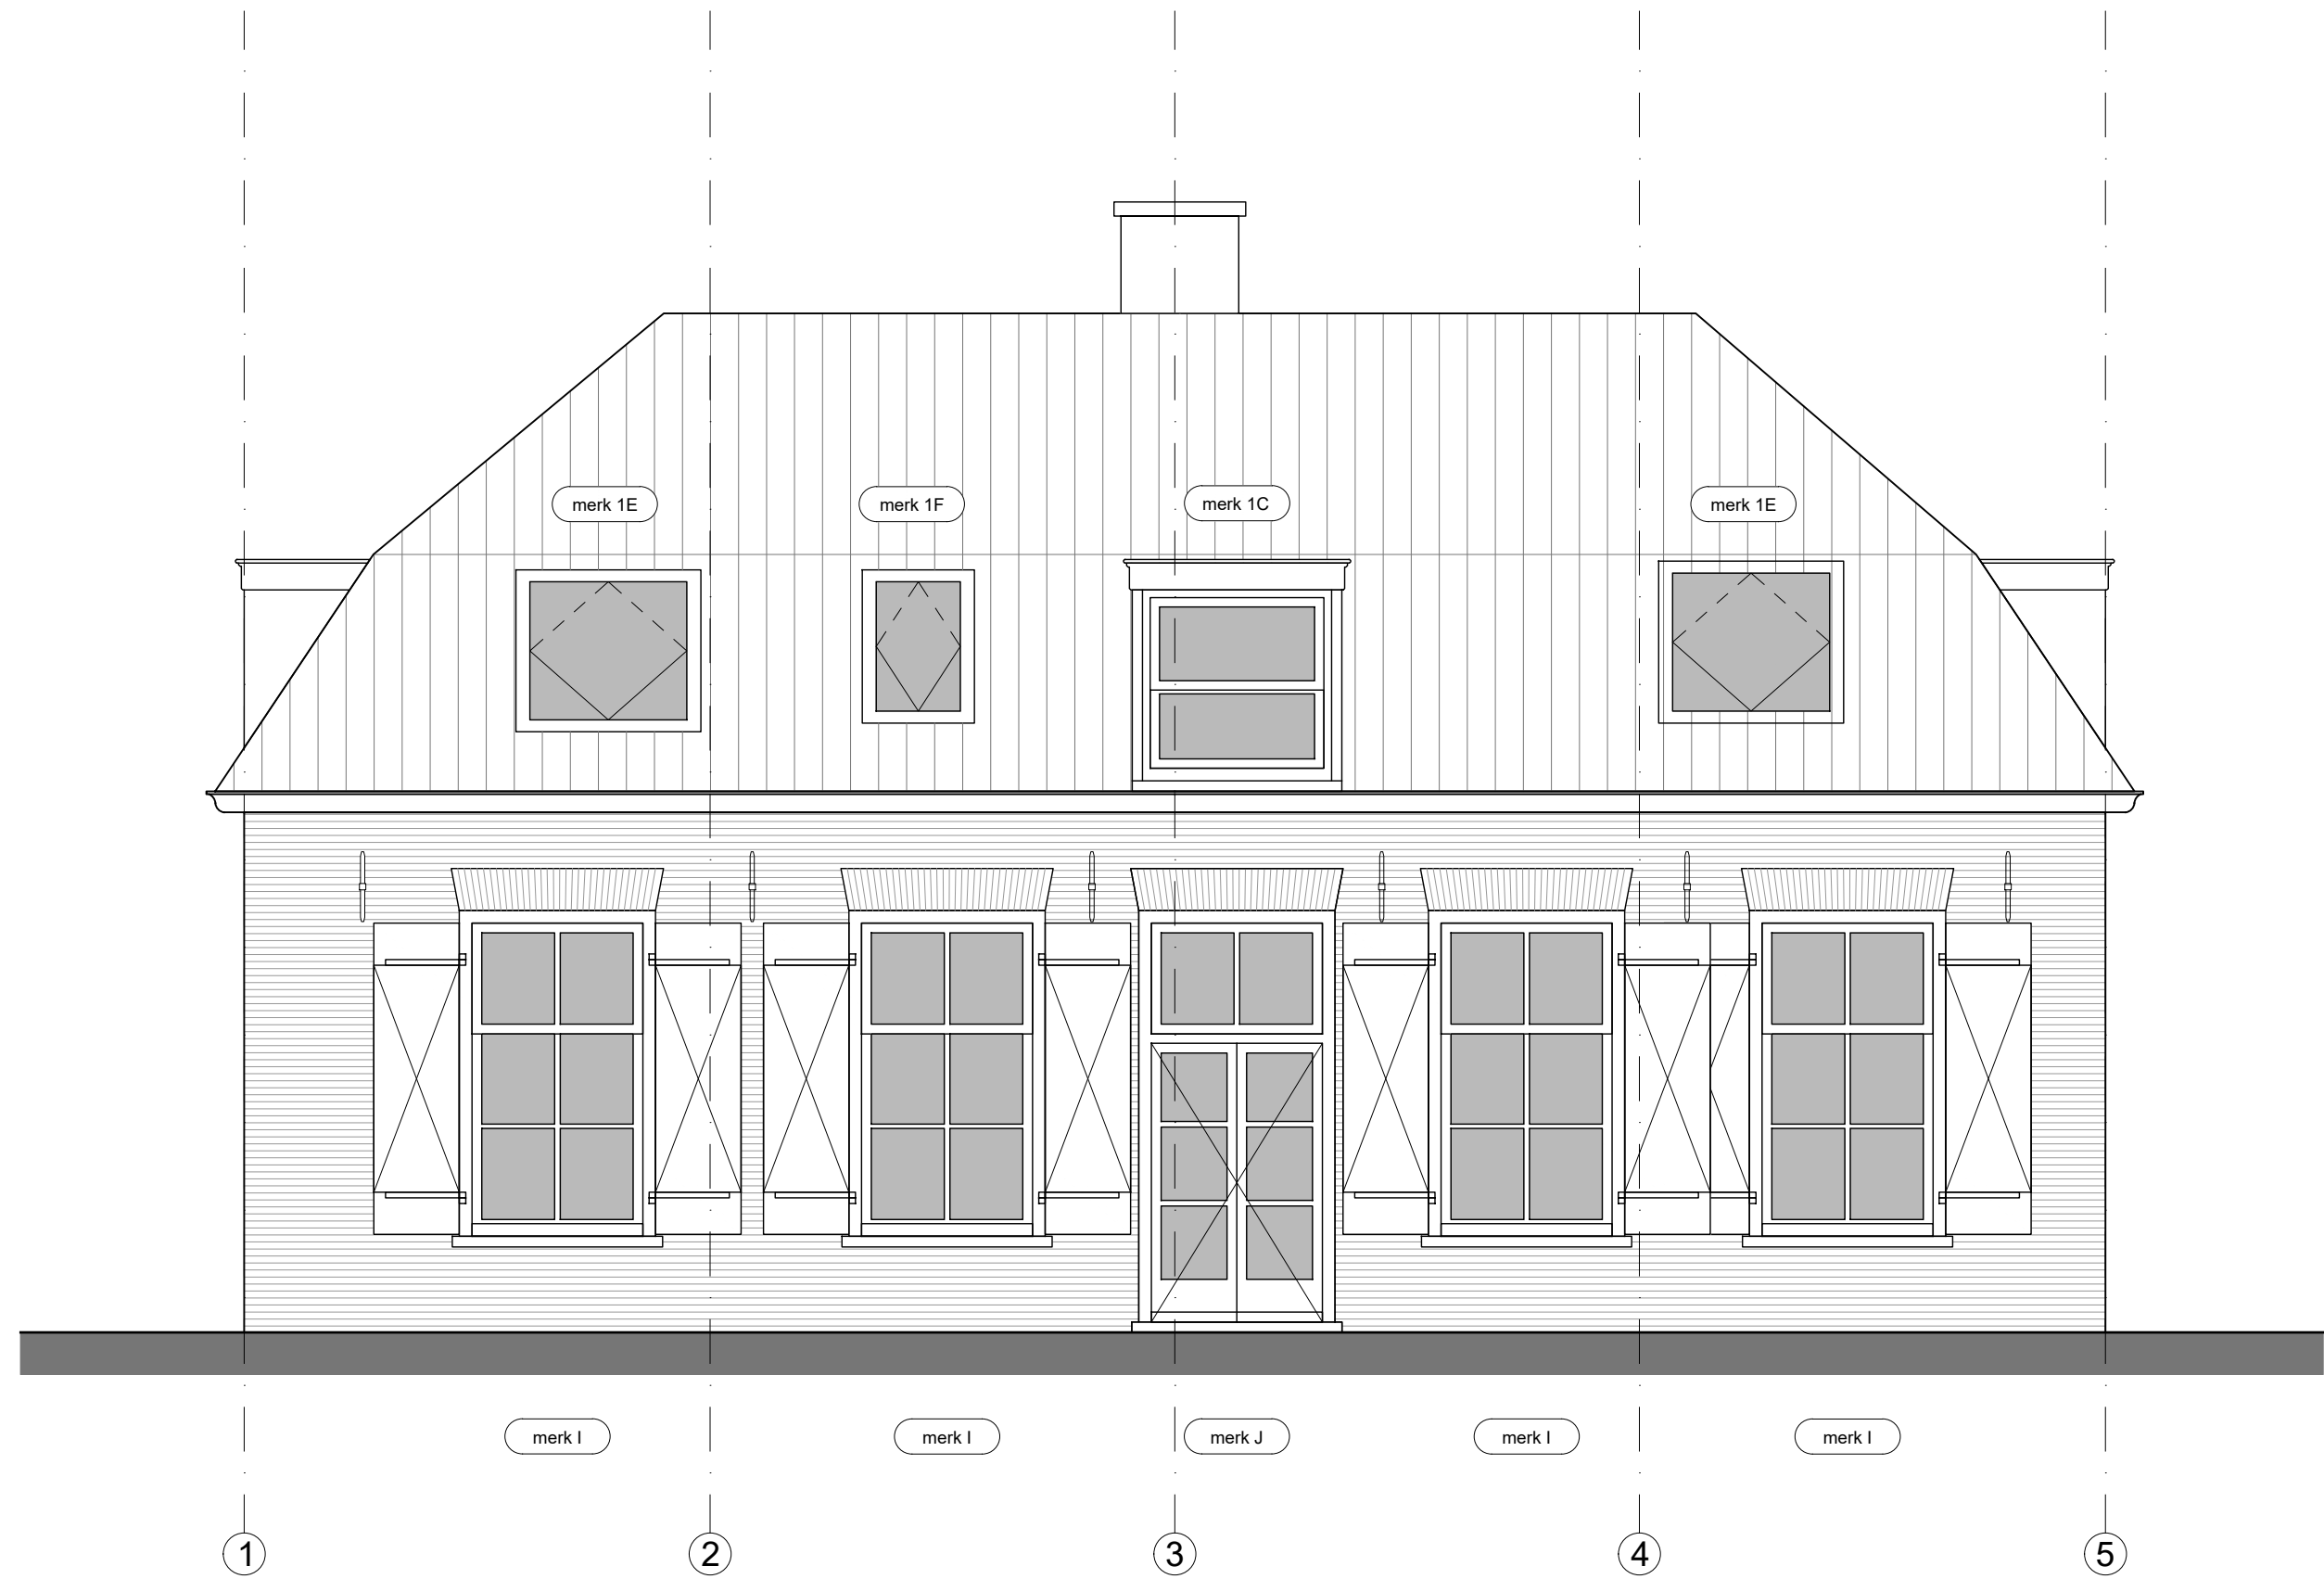

ACHTERGEVEL

Alle maatvoering in het werk te controleren.
Alle hout-, staal- & betonconstructies volgens constructeur.


Aanzicht achtergevel

project: Verduurzaming en verbouwing | Buzziburglaan 16 | 3972 EE Driebergen
fase: Definitief ontwerp schaal: 1:50 op A2
datum: 03-07-2026 | TtK wijziging:

25-03.DO.212

Kraal architecten BV | Vossegatselaan 32 | 3583 RT Utrecht | 030 223 96 77
www.kraalarchitecten.nl | info@kraalarchitecten.nl



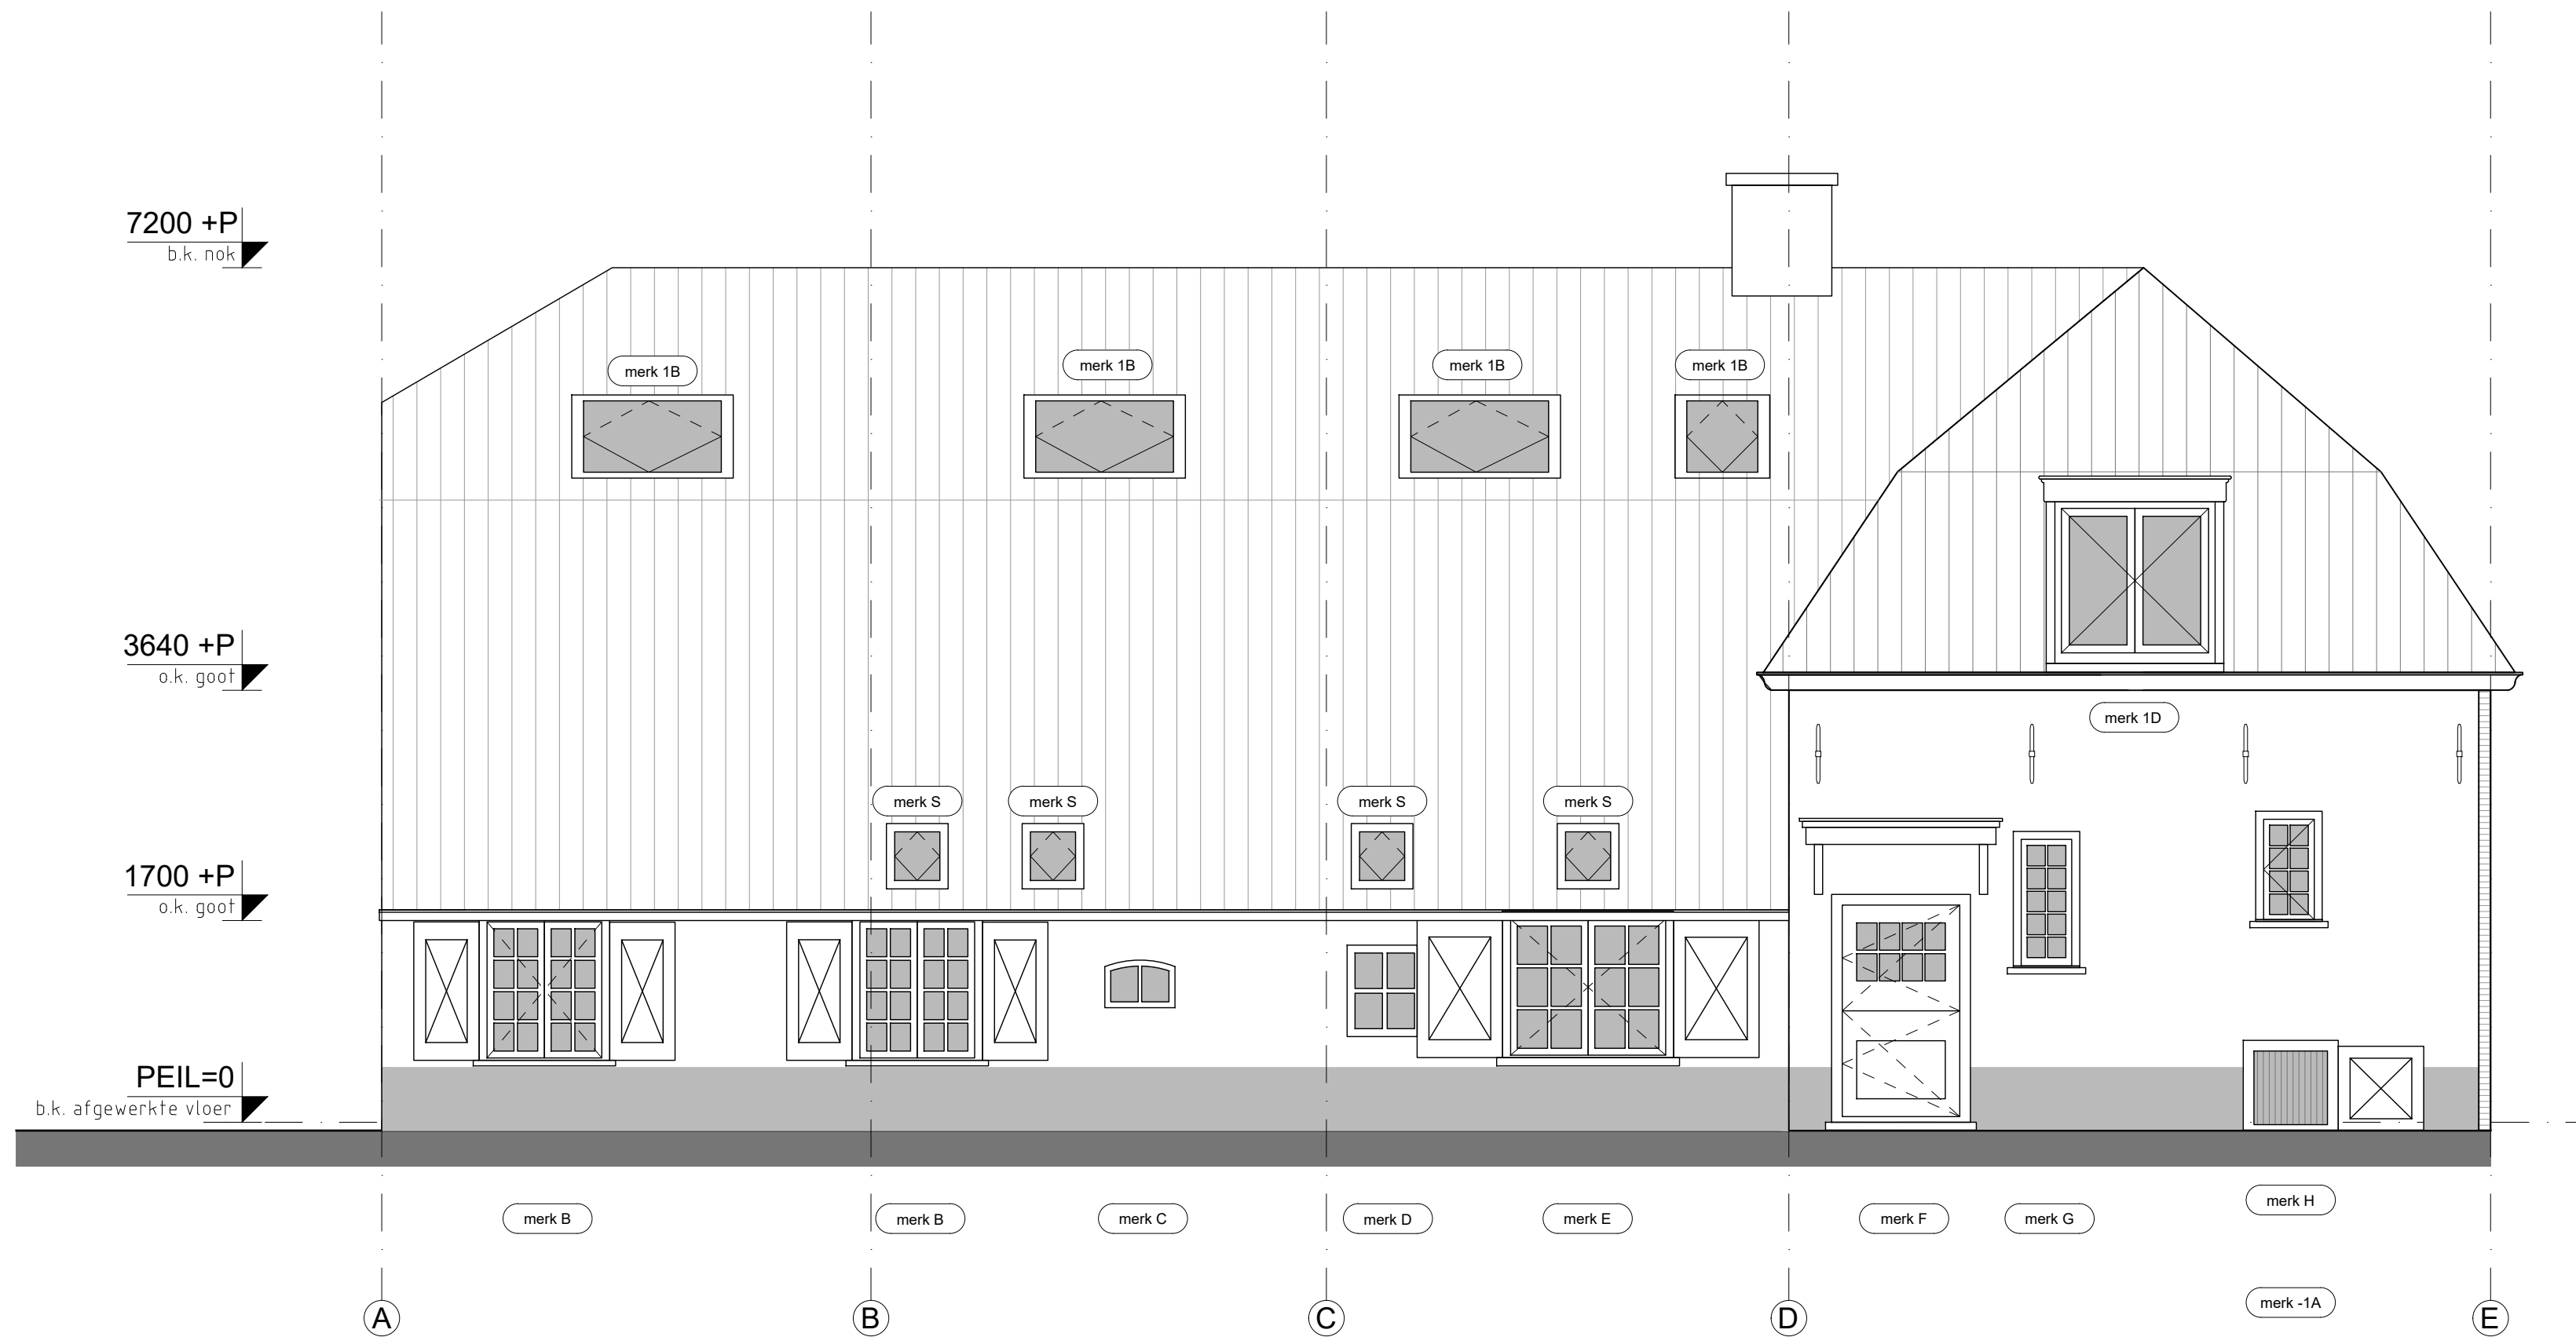

RECHTER ZIJGEVEL

Alle maatvoering in het werk te controleren.
Alle hout-, staal- & betonconstructies volgens constructeur.


Aanzicht rechter zijgevel

project: Verduurzaming en verbouwing | Buzziburglaan 16 | 3972 EE Driebergen
fase: Definitief ontwerp schaal: 1:50 op A2
datum: 03-07-2026 | TtK wijziging:

25-03.DO.213

Kraal architecten BV | Vossegatselaan 32 | 3583 RT Utrecht | 030 223 96 77
www.kraalarchitecten.nl | info@kraalarchitecten.nl



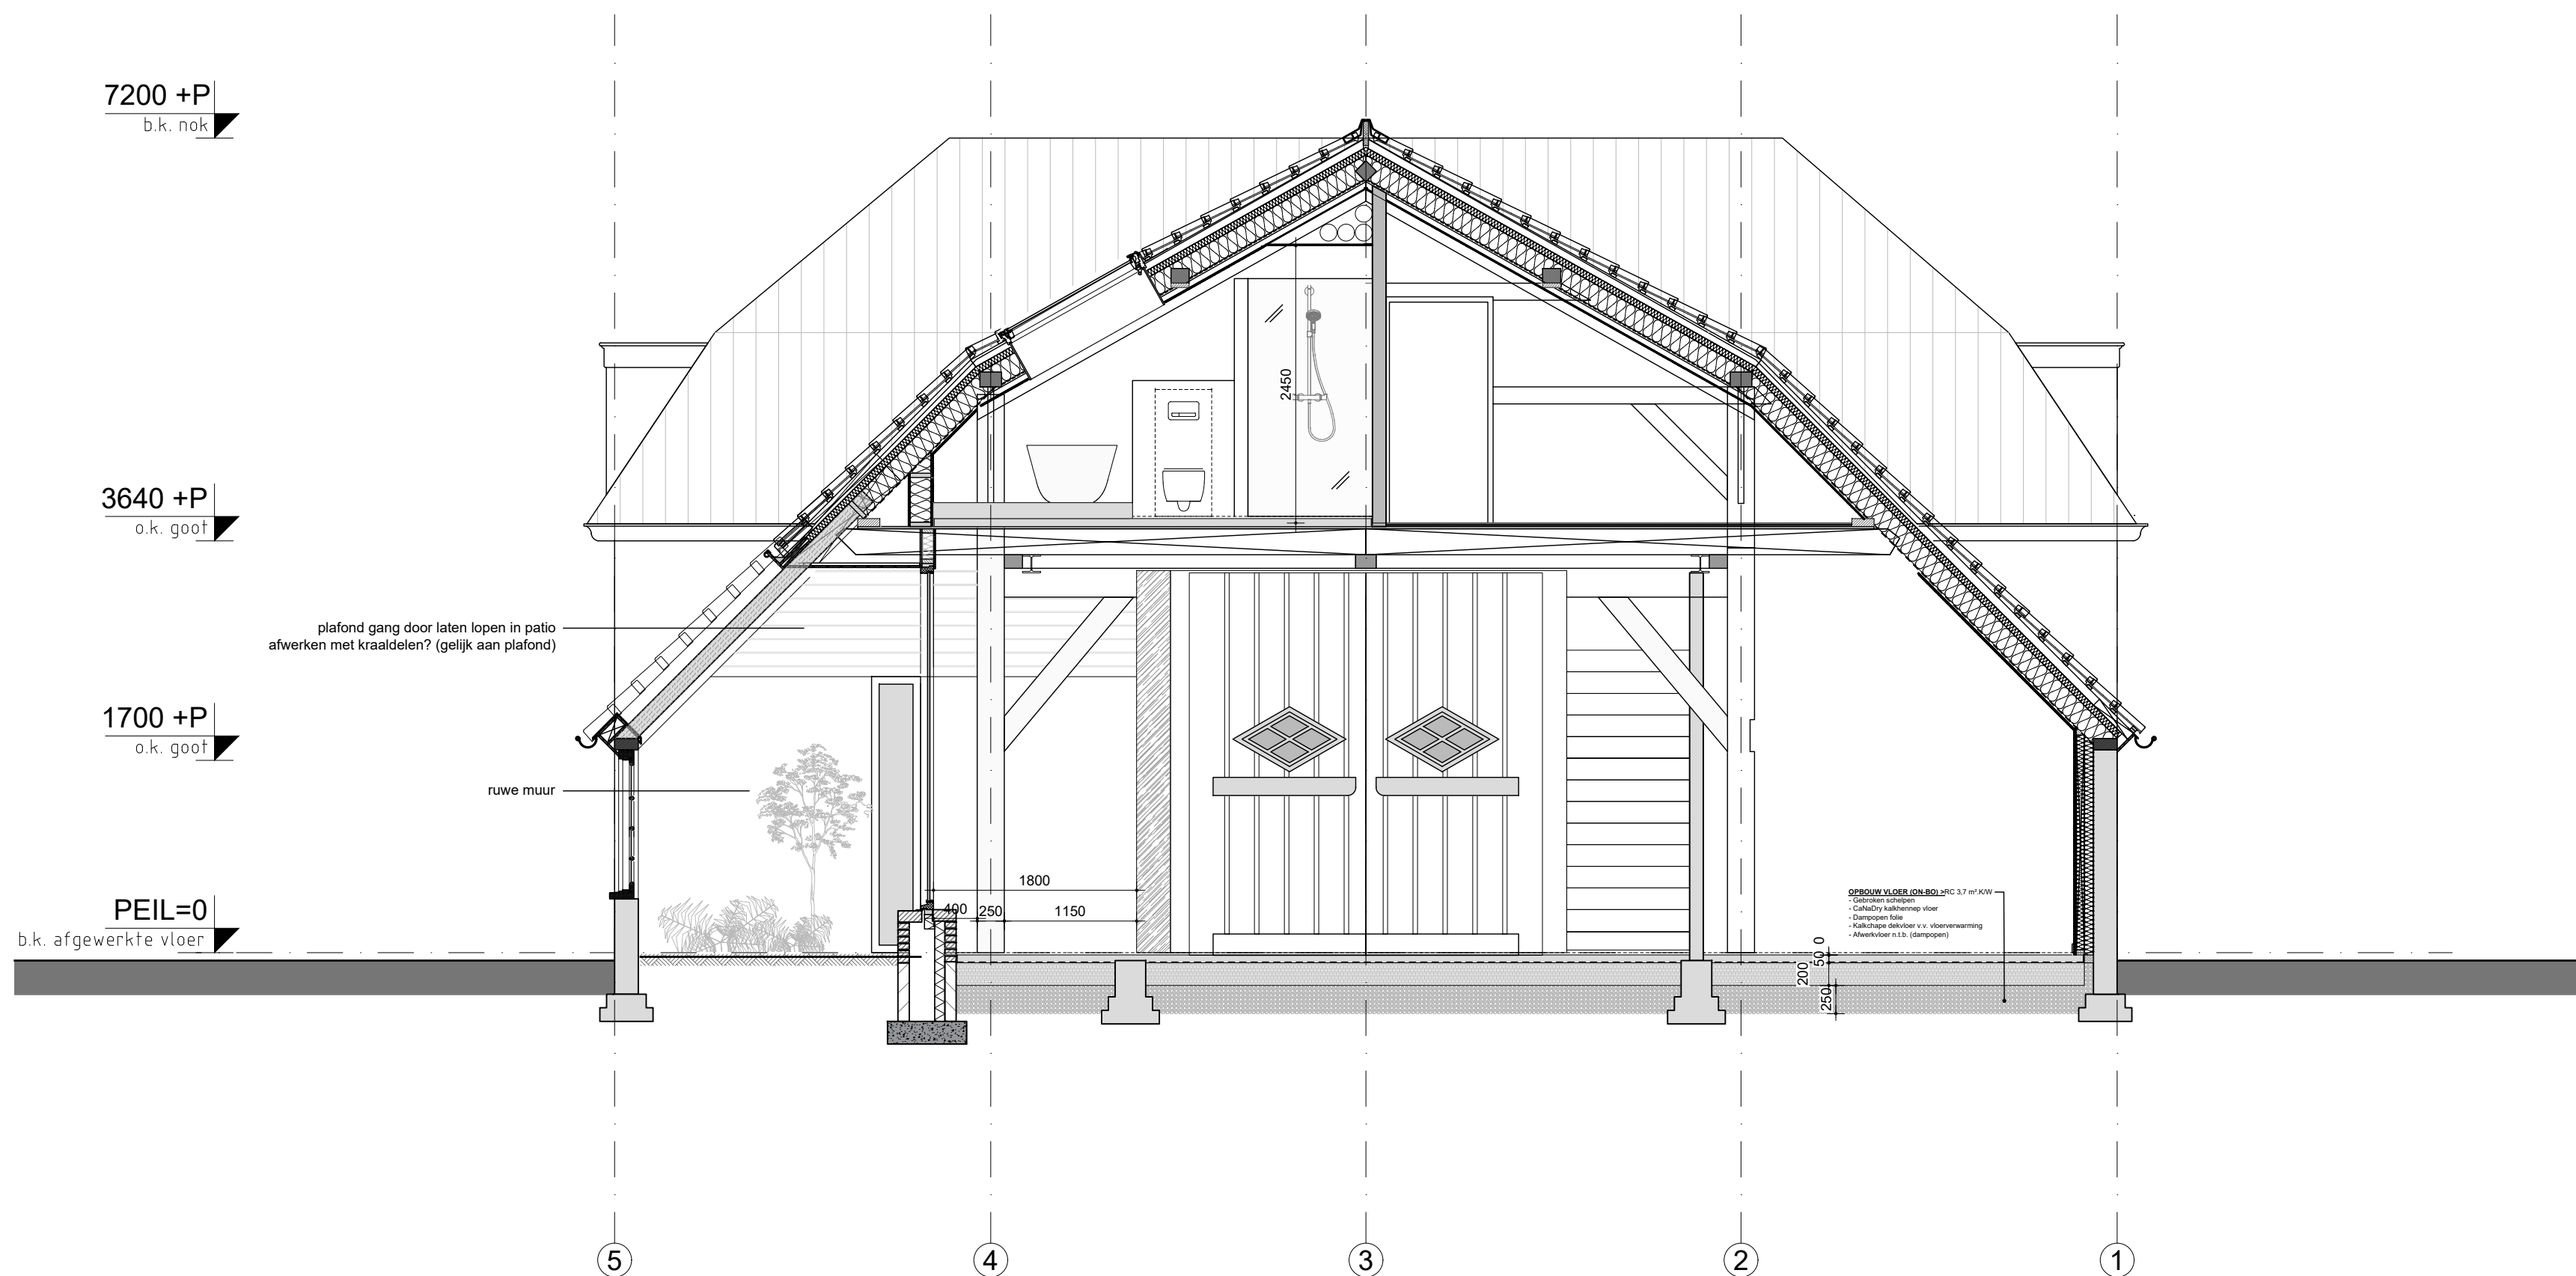

Alle maatvoering in het werk te controleren.
Alle hout-, staal- & betonconstructies volgens constructeur.

Doorsnede A-A



project: Verduurzaming en verbouwing | Buzziburglaan 16 | 3972 EE Driebergen
fase: Definitief ontwerp schaal: 1:50 op A2
datum: 17-03-2026 | TtK wijziging:

25-03.DO.310

Kraal architecten BV | Vossegatselaan 32 | 3583 RT Utrecht | 030 223 96 77
www.kraalarchitecten.nl | info@kraalarchitecten.nl



D.01

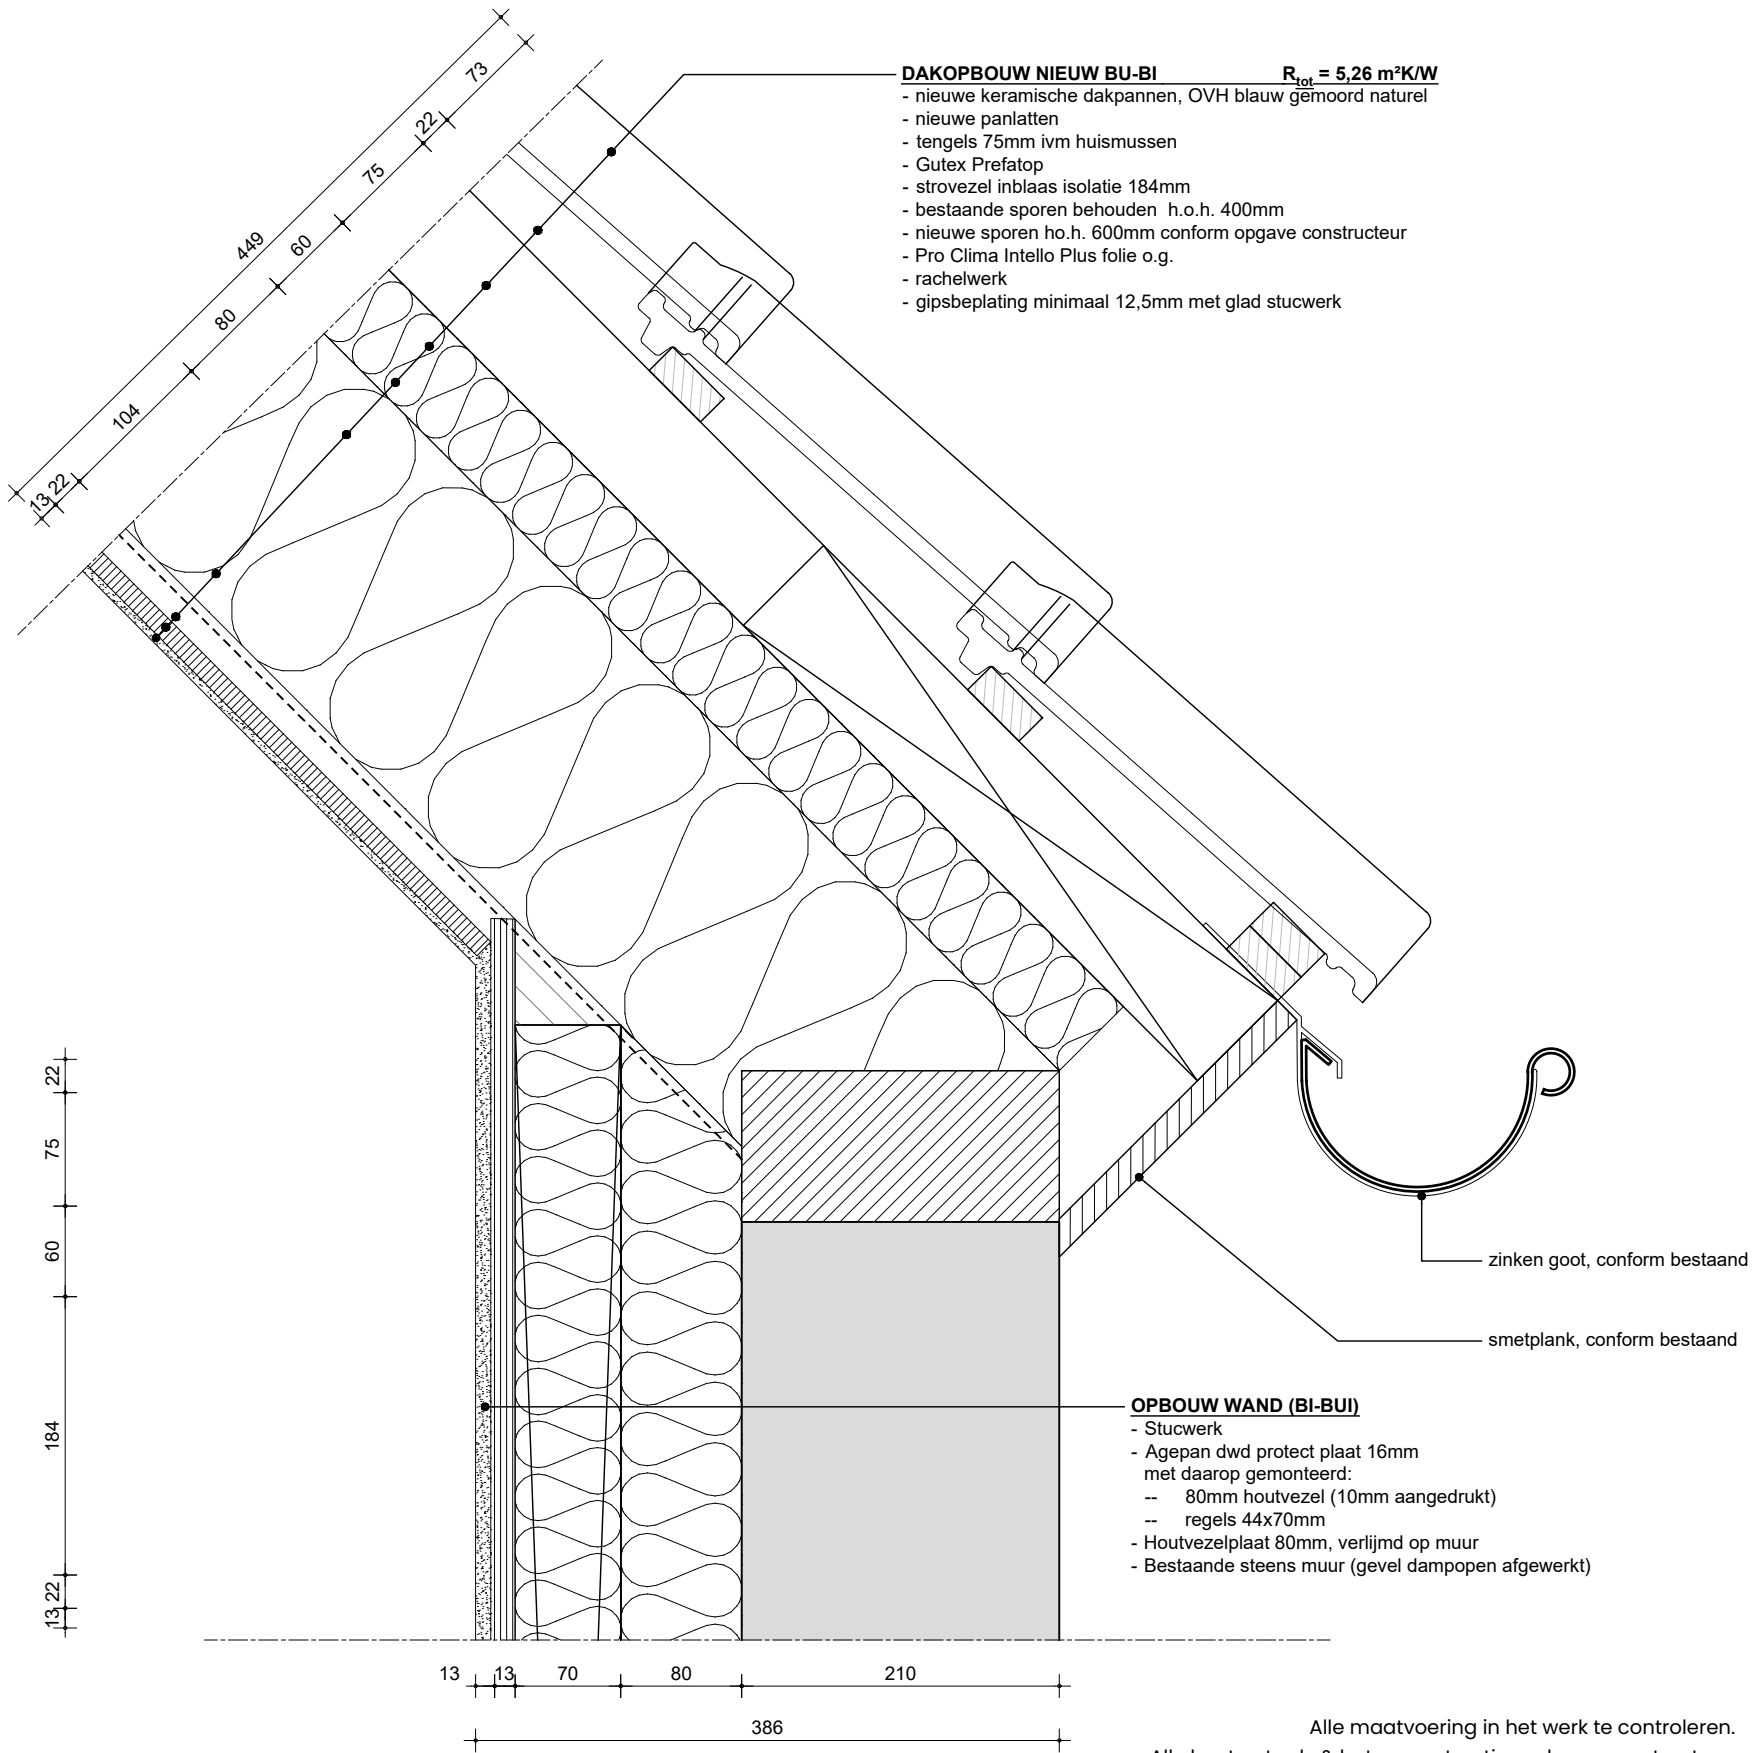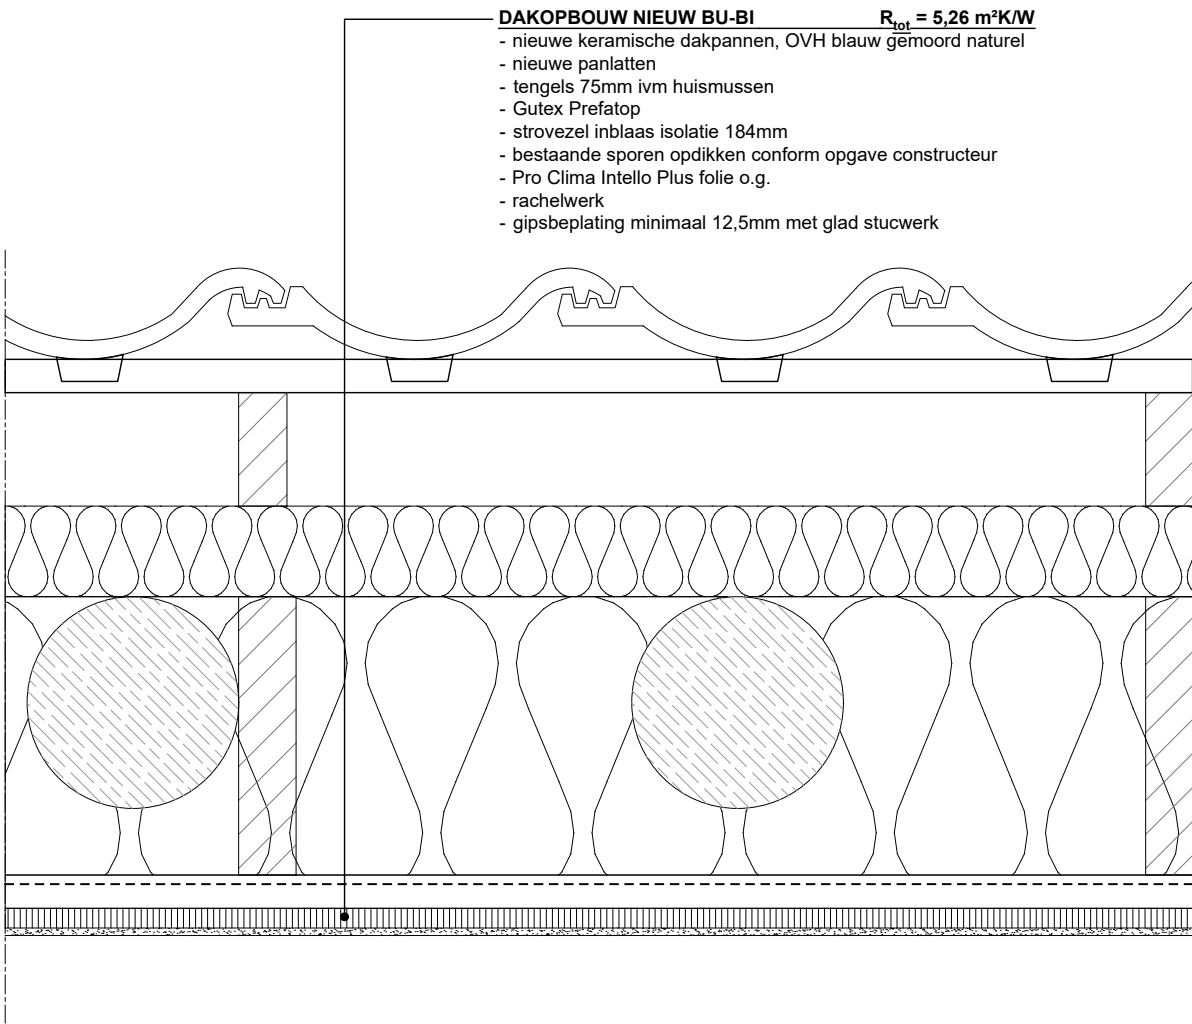


Principedetail

project: Verduurzaming en verbouwing | Buzziburglaan 16 | 3972 EE Driebergen
fase: Bestaande situatie schaal: 1:5 op A3
datum: 03-07-2026 | TtK wijziging:

25-03.DO.410



D.02

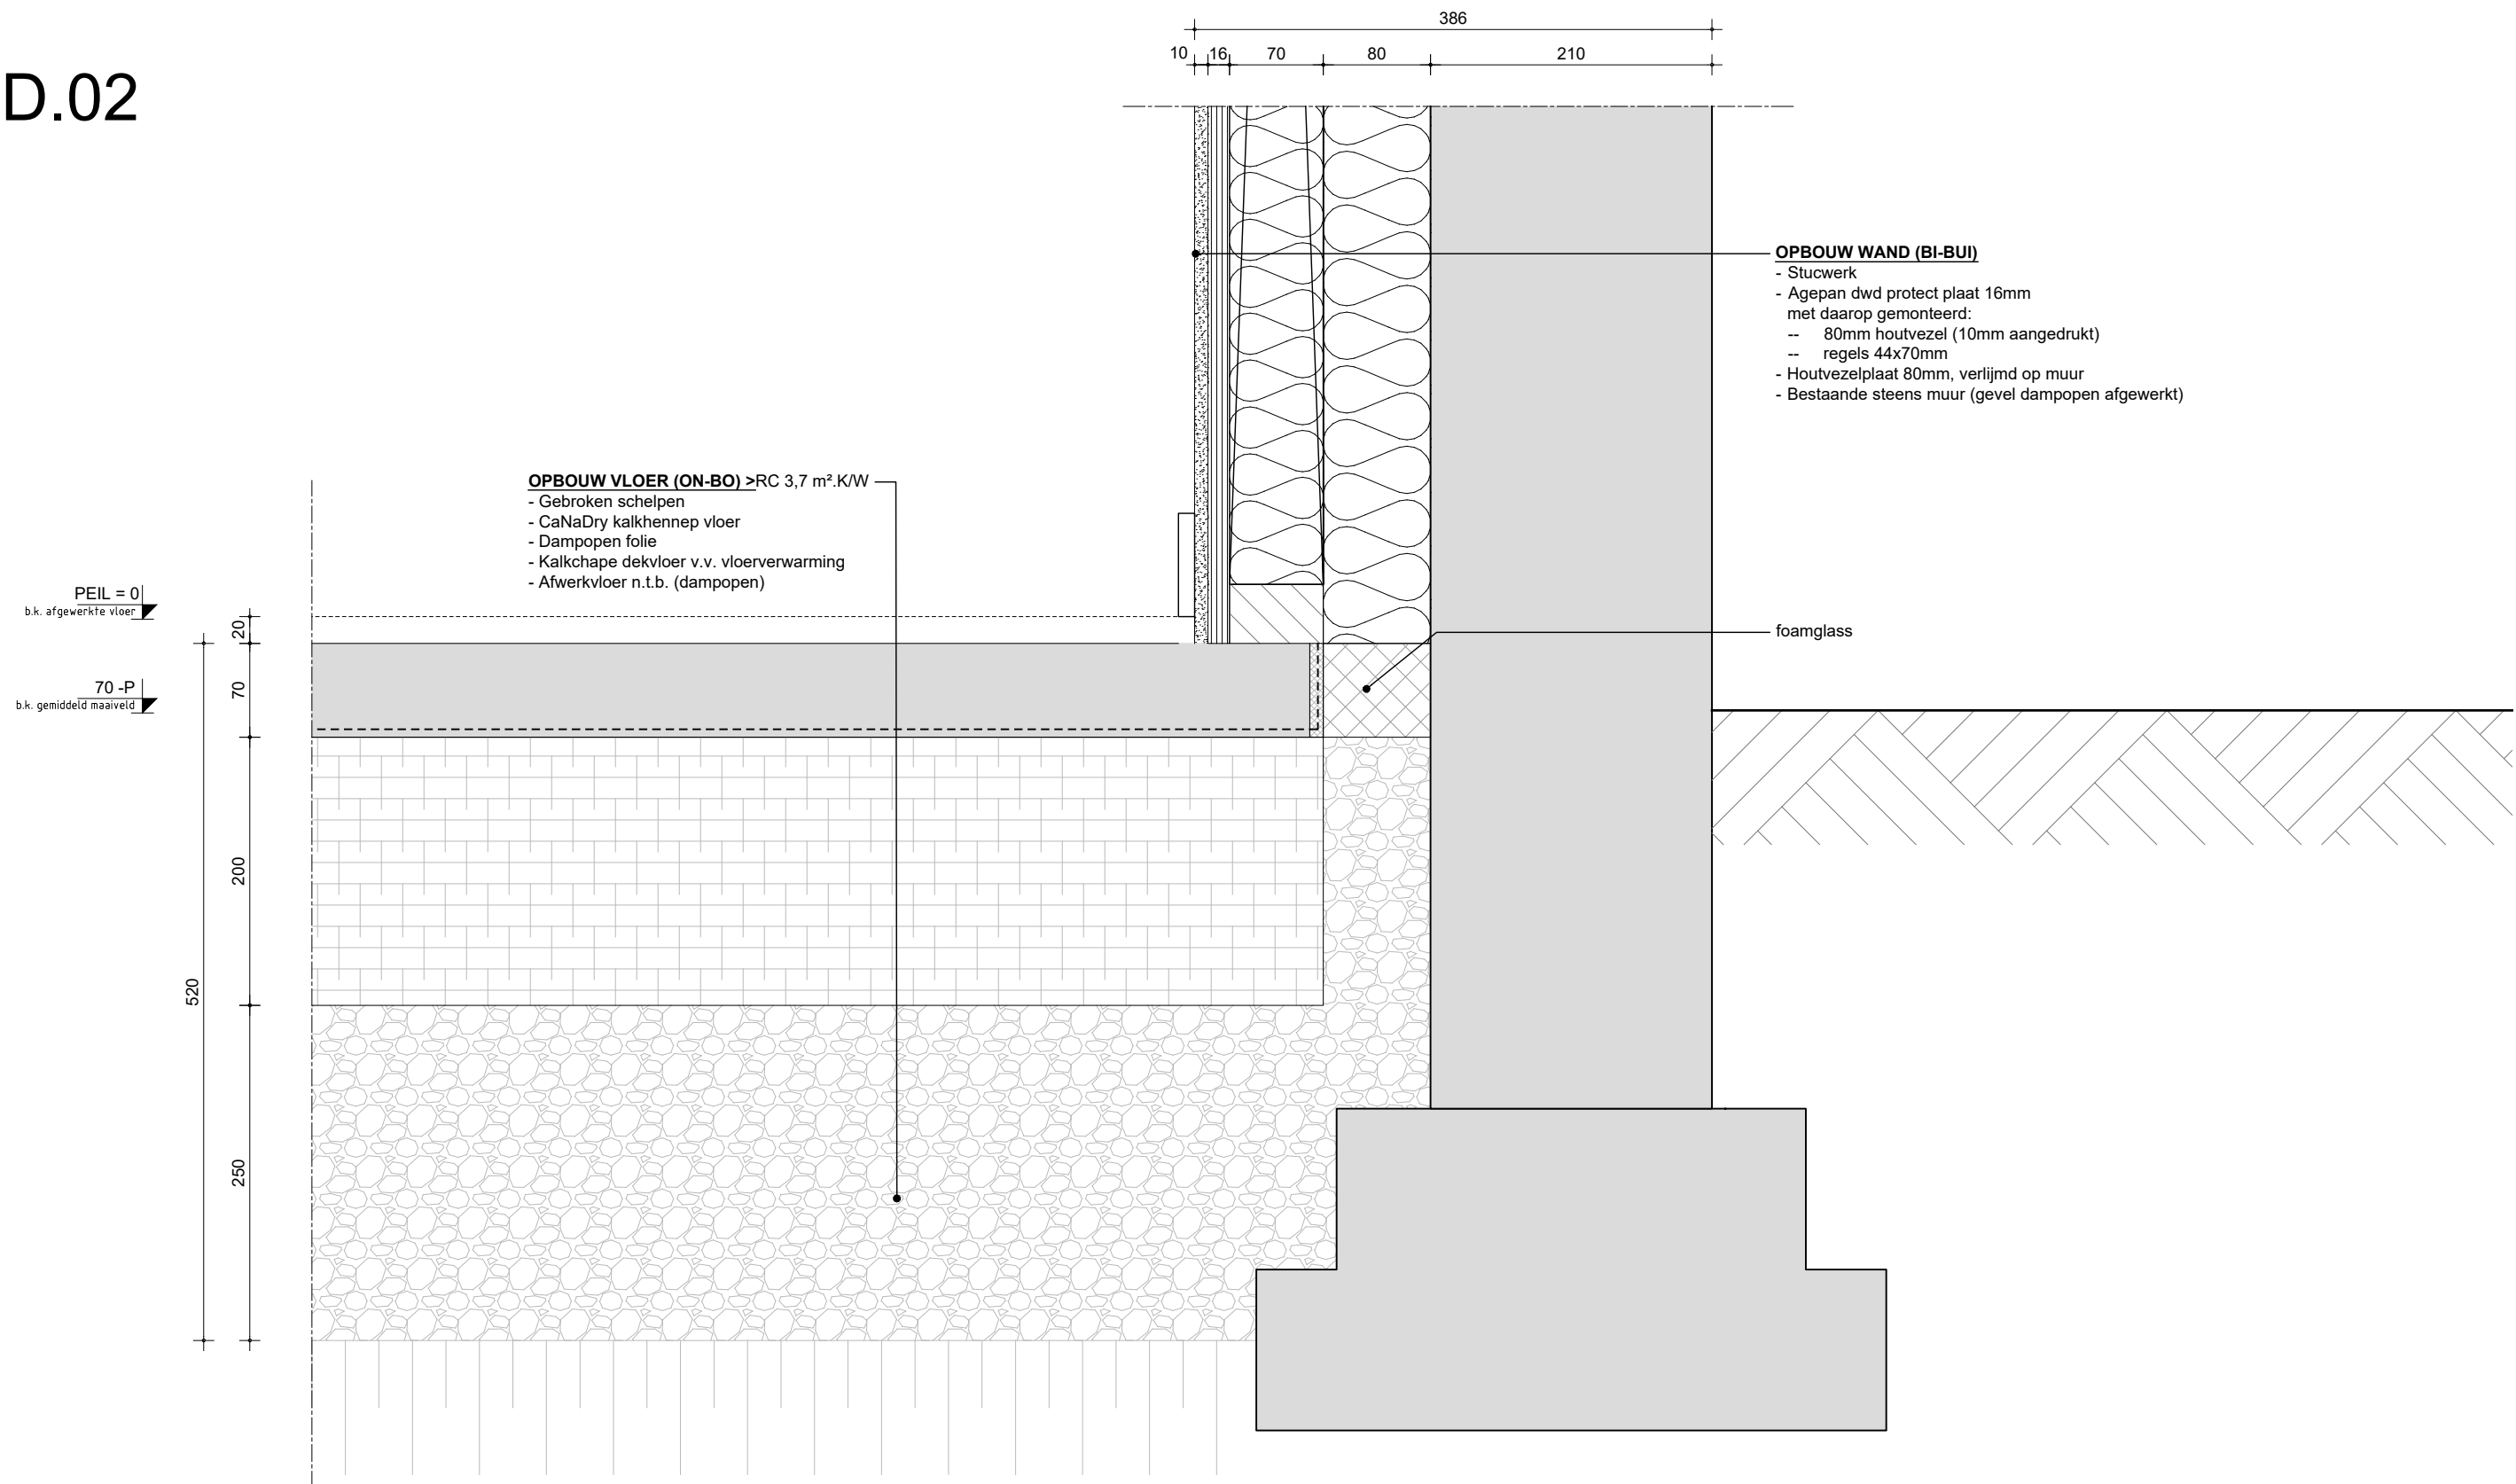

Alle maatvoering in het werk te controleren.
Alle hout-, staal- & betonconstructies volgens constructeur.

Principedetail


project: Verduurzaming en verbouwing | Buzziburglaan 16 | 3972 EE Driebergen
fase: Definitief ontwerp schaal: 1:5 op A3
datum: 03-07-2026 | TtK wijziging:

25-03.DO.411

Kraal architecten BV | Vossegatselaan 32 | 3583 RT Utrecht | 030 223 96 77
www.kraalarchitecten.nl | info@kraalarchitecten.nl



D.03

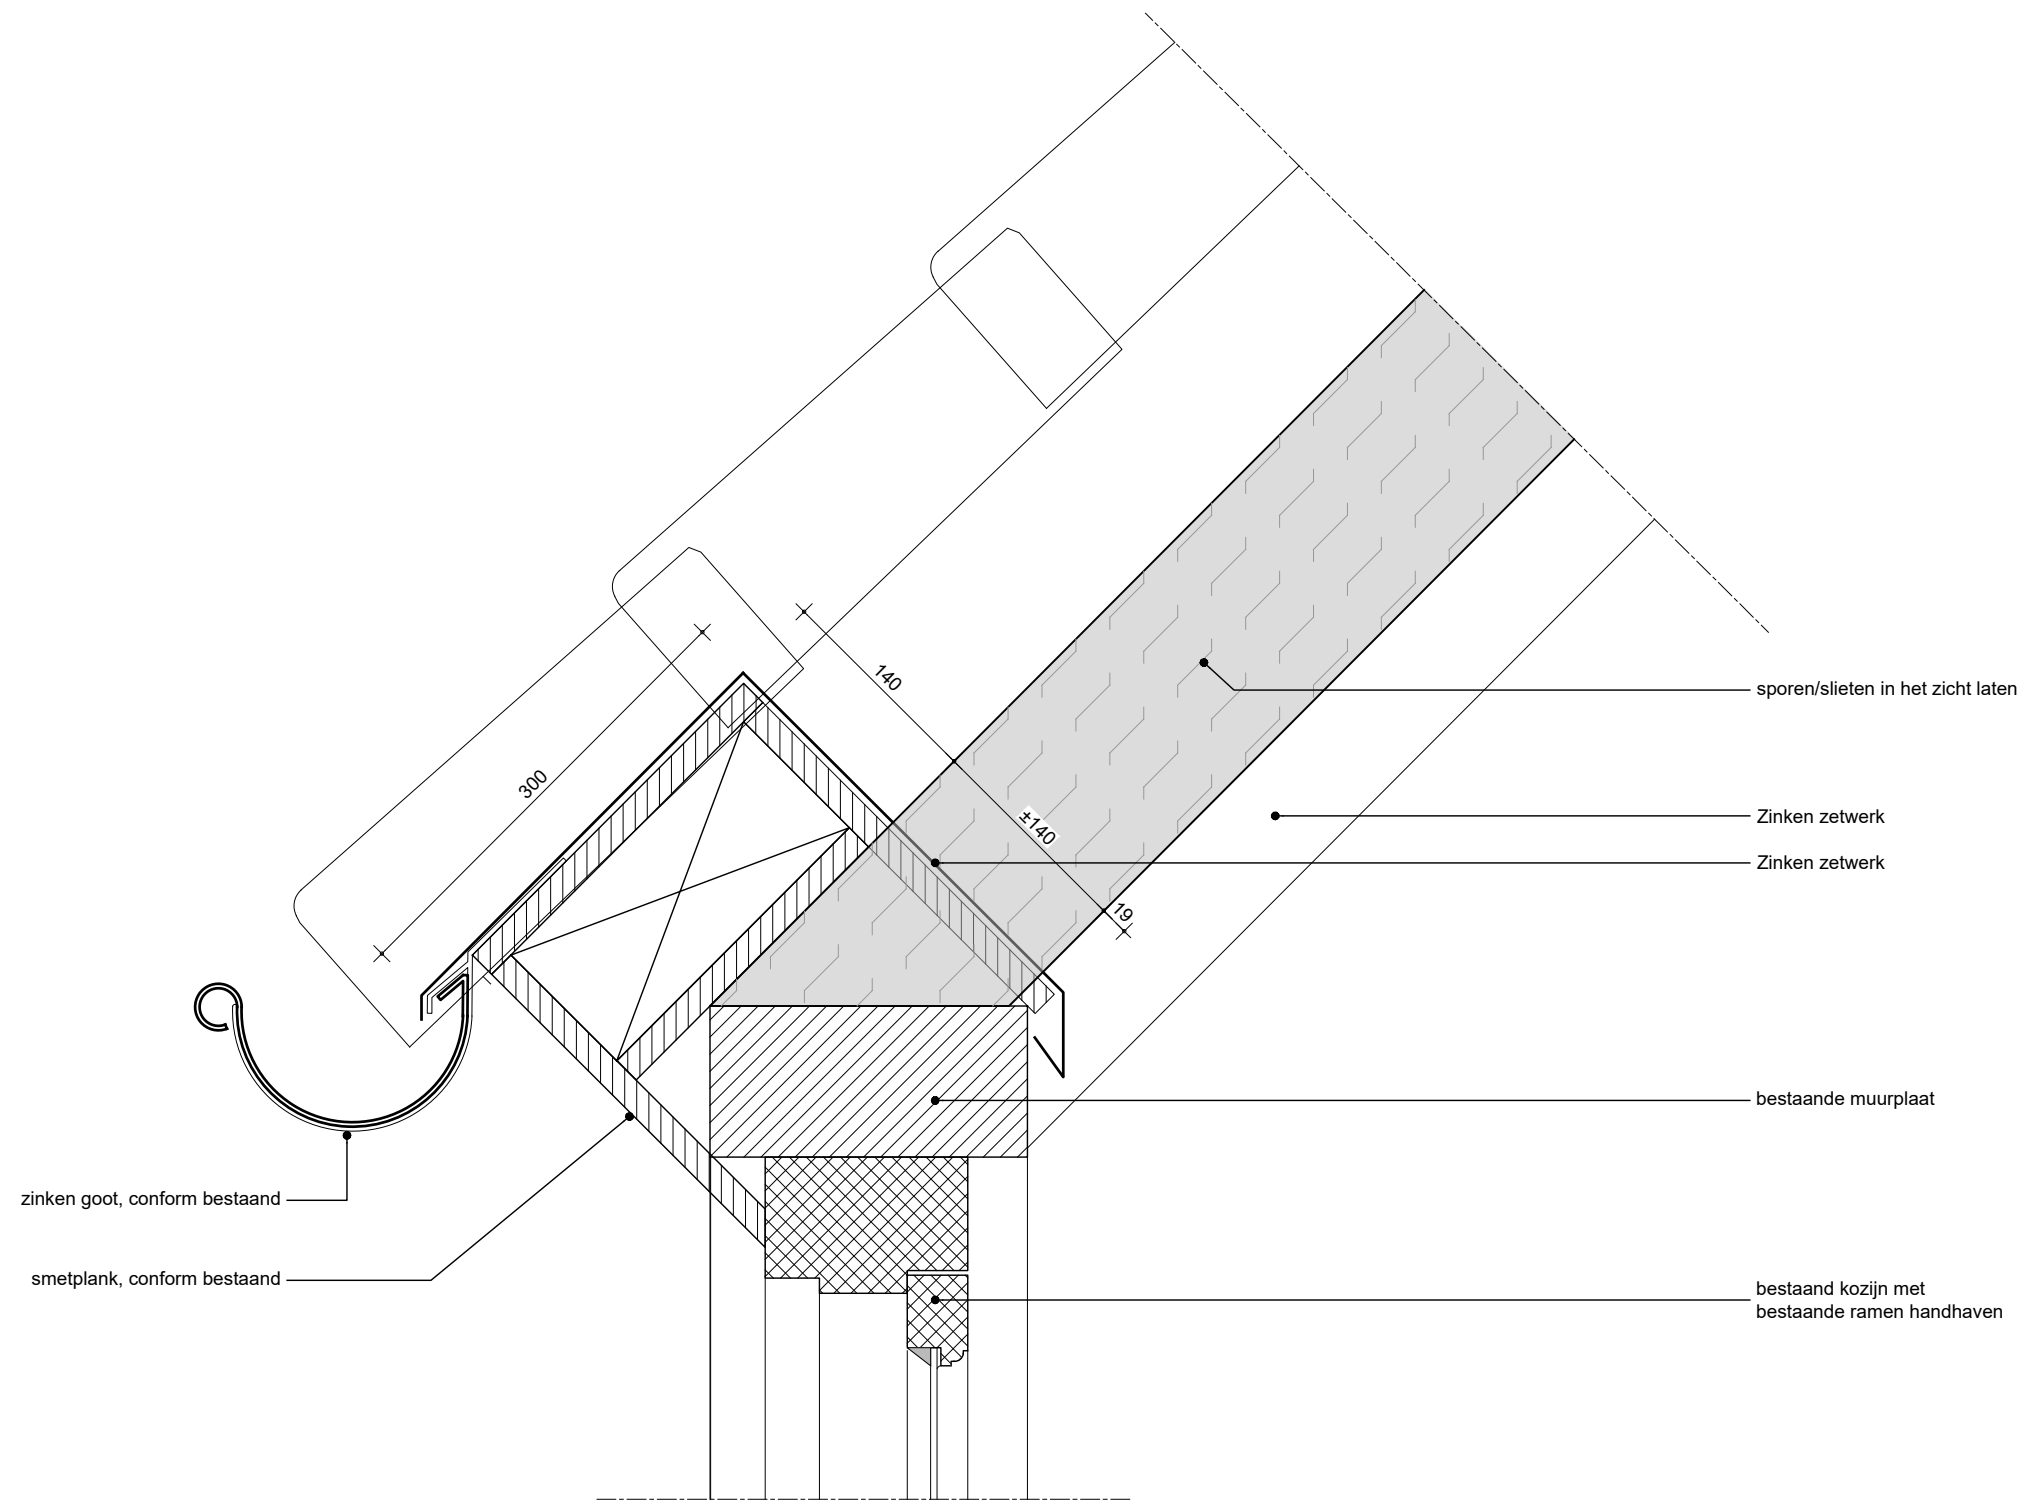

Alle maatvoering in het werk te controleren.
Alle hout-, staal- & betonconstructies volgens constructeur.

Principedetail


project: Verduurzaming en verbouwing | Buzziburglaan 16 | 3972 EE Driebergen
fase: Definitief ontwerp schaal: 1:5 op A3
datum: 03-07-2026 | TtK wijziging:

25-03.DO.412

Kraal architecten BV | Vossegatselaan 32 | 3583 RT Utrecht | 030 223 96 77
www.kraalarchitecten.nl | info@kraalarchitecten.nl



D.04

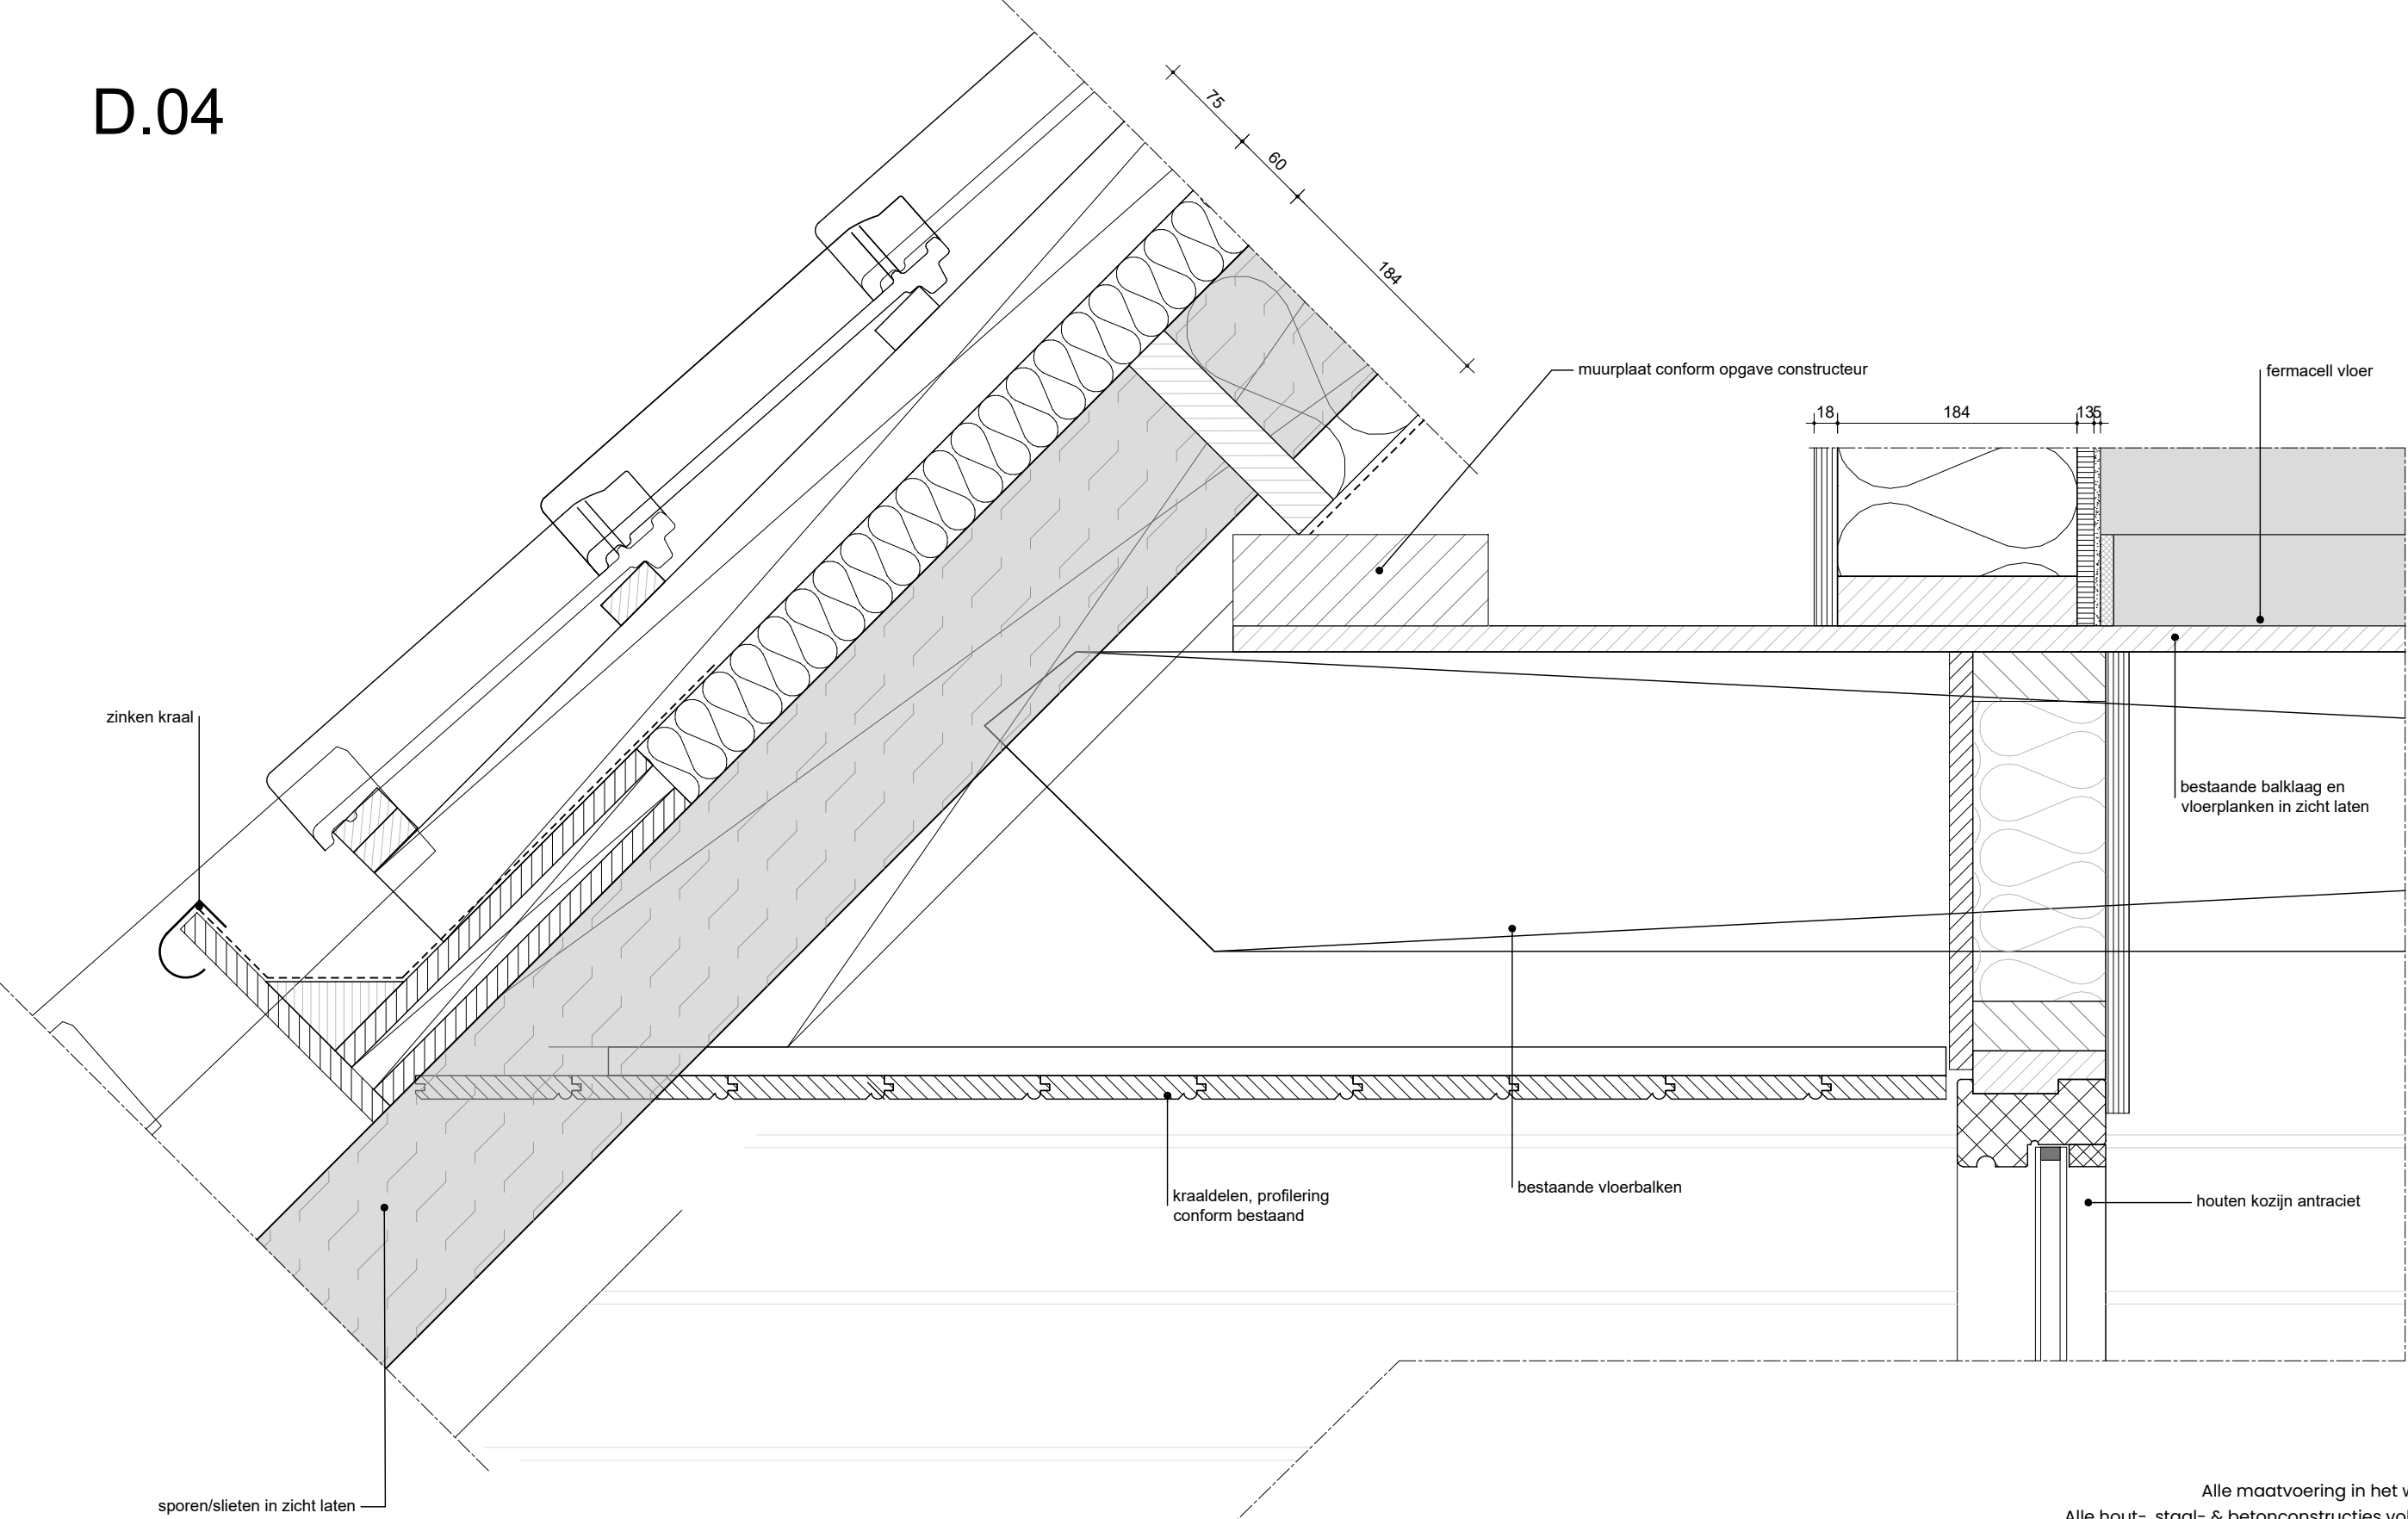

Alle maatvoering in het werk te controleren.
Alle hout-, staal- & betonconstructies volgens constructeur.

Principedetail

project: Verduurzaming en verbouwing | Buzziburglaan 16 | 3972 EE Driebergen
fase: Definitief ontwerp schaal: 1:5 op A3
datum: 03-07-2026 | TtK wijziging:

25-03.DO.413


Kraal architecten BV | Vossegatselaan 32 | 3583 RT Utrecht | 030 223 96 77
www.kraalarchitecten.nl | info@kraalarchitecten.nl



D.05

- DAKOPBOUW NIEUW BU-BI** $R_{tot} = 5,26 \text{ m}^2\text{K/W}$
- nieuwe keramische dakpannen, OVH blauw gemoord naturel
 - nieuwe panlatten
 - tengels 75mm ivm huismussen
 - Gutex Prefatop
 - strovezel inblaas isolatie 184mm
 - bestaande sporen behouden h.o.h. 400mm
 - nieuwe sporen ho.h. 600mm conform opgave constructeur
 - Pro Clima Intello Plus folie o.g.
 - rachelwerk
 - gipsbeplating minimaal 12,5mm met glad stucwerk

D.06

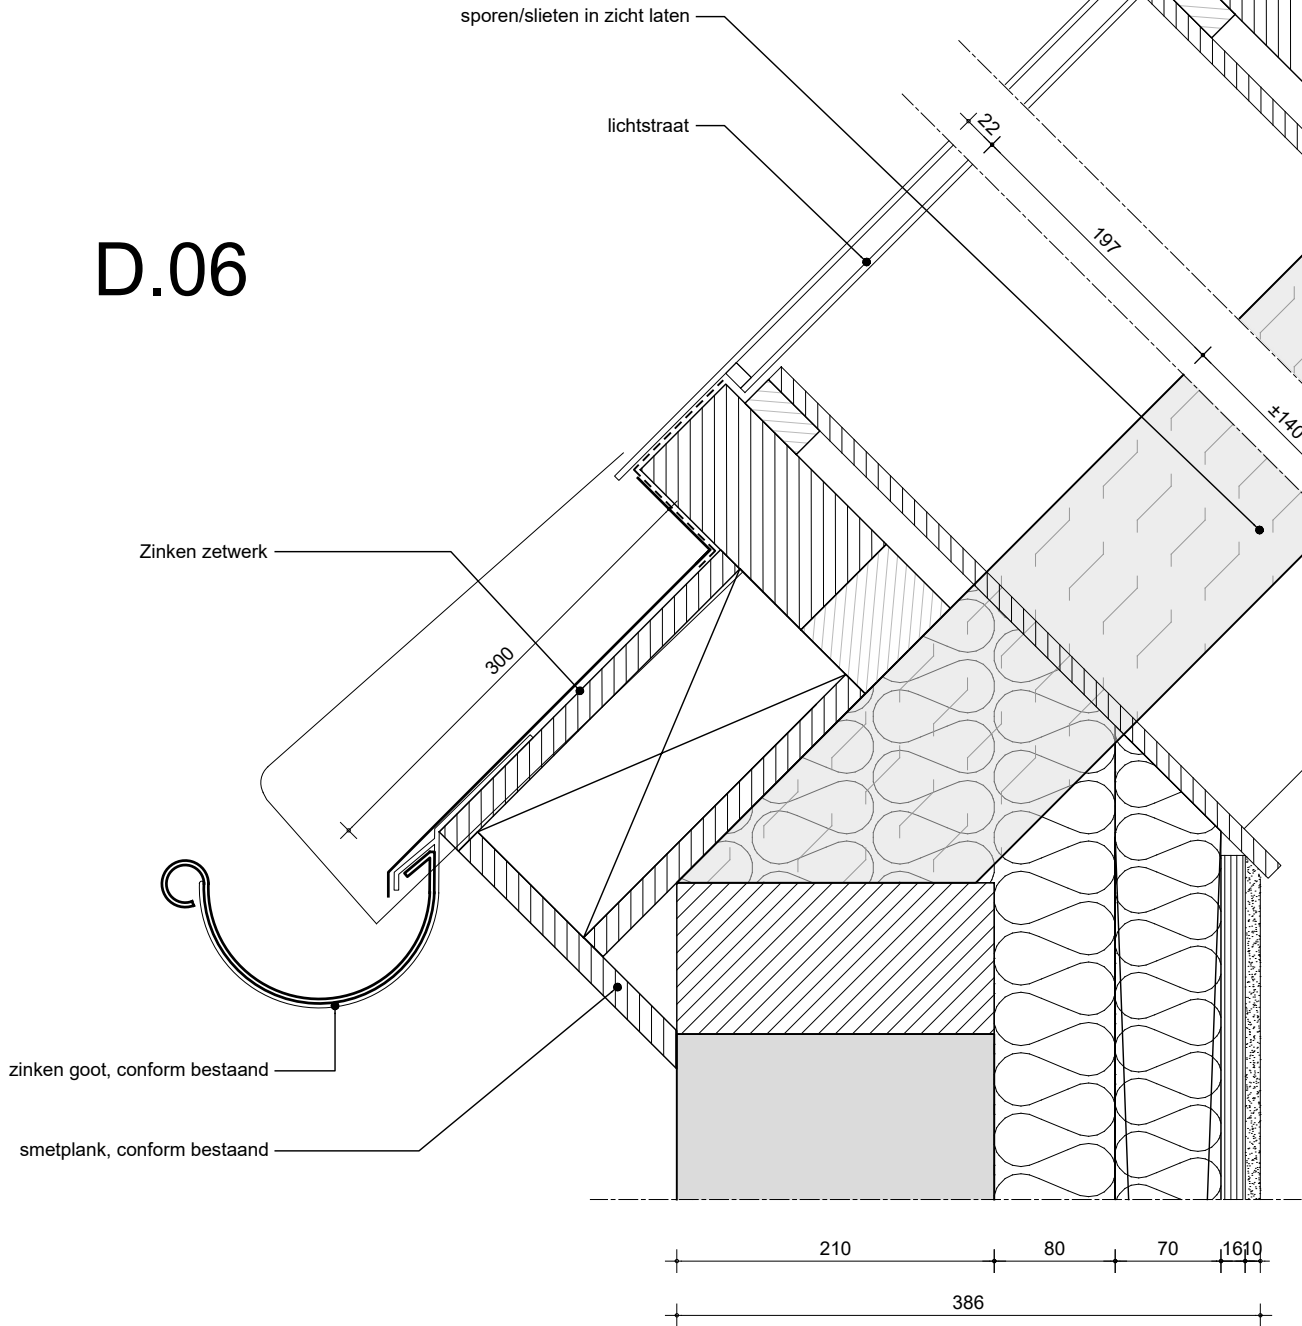

Alle maatvoering in het werk te controleren.
Alle hout-, staal- & betonconstructies volgens constructeur.


Principedetail

project: Verduurzaming en verbouwing | Buzziburglaan 16 | 3972 EE Driebergen
fase: Definitief ontwerp schaal: 1:5 op A3
datum: 03-07-2026 | TtK wijziging:

25-03.DO.414

Kraal architecten BV | Vossegatselaan 32 | 3583 RT Utrecht | 030 223 96 77
www.kraalarchitecten.nl | info@kraalarchitecten.nl



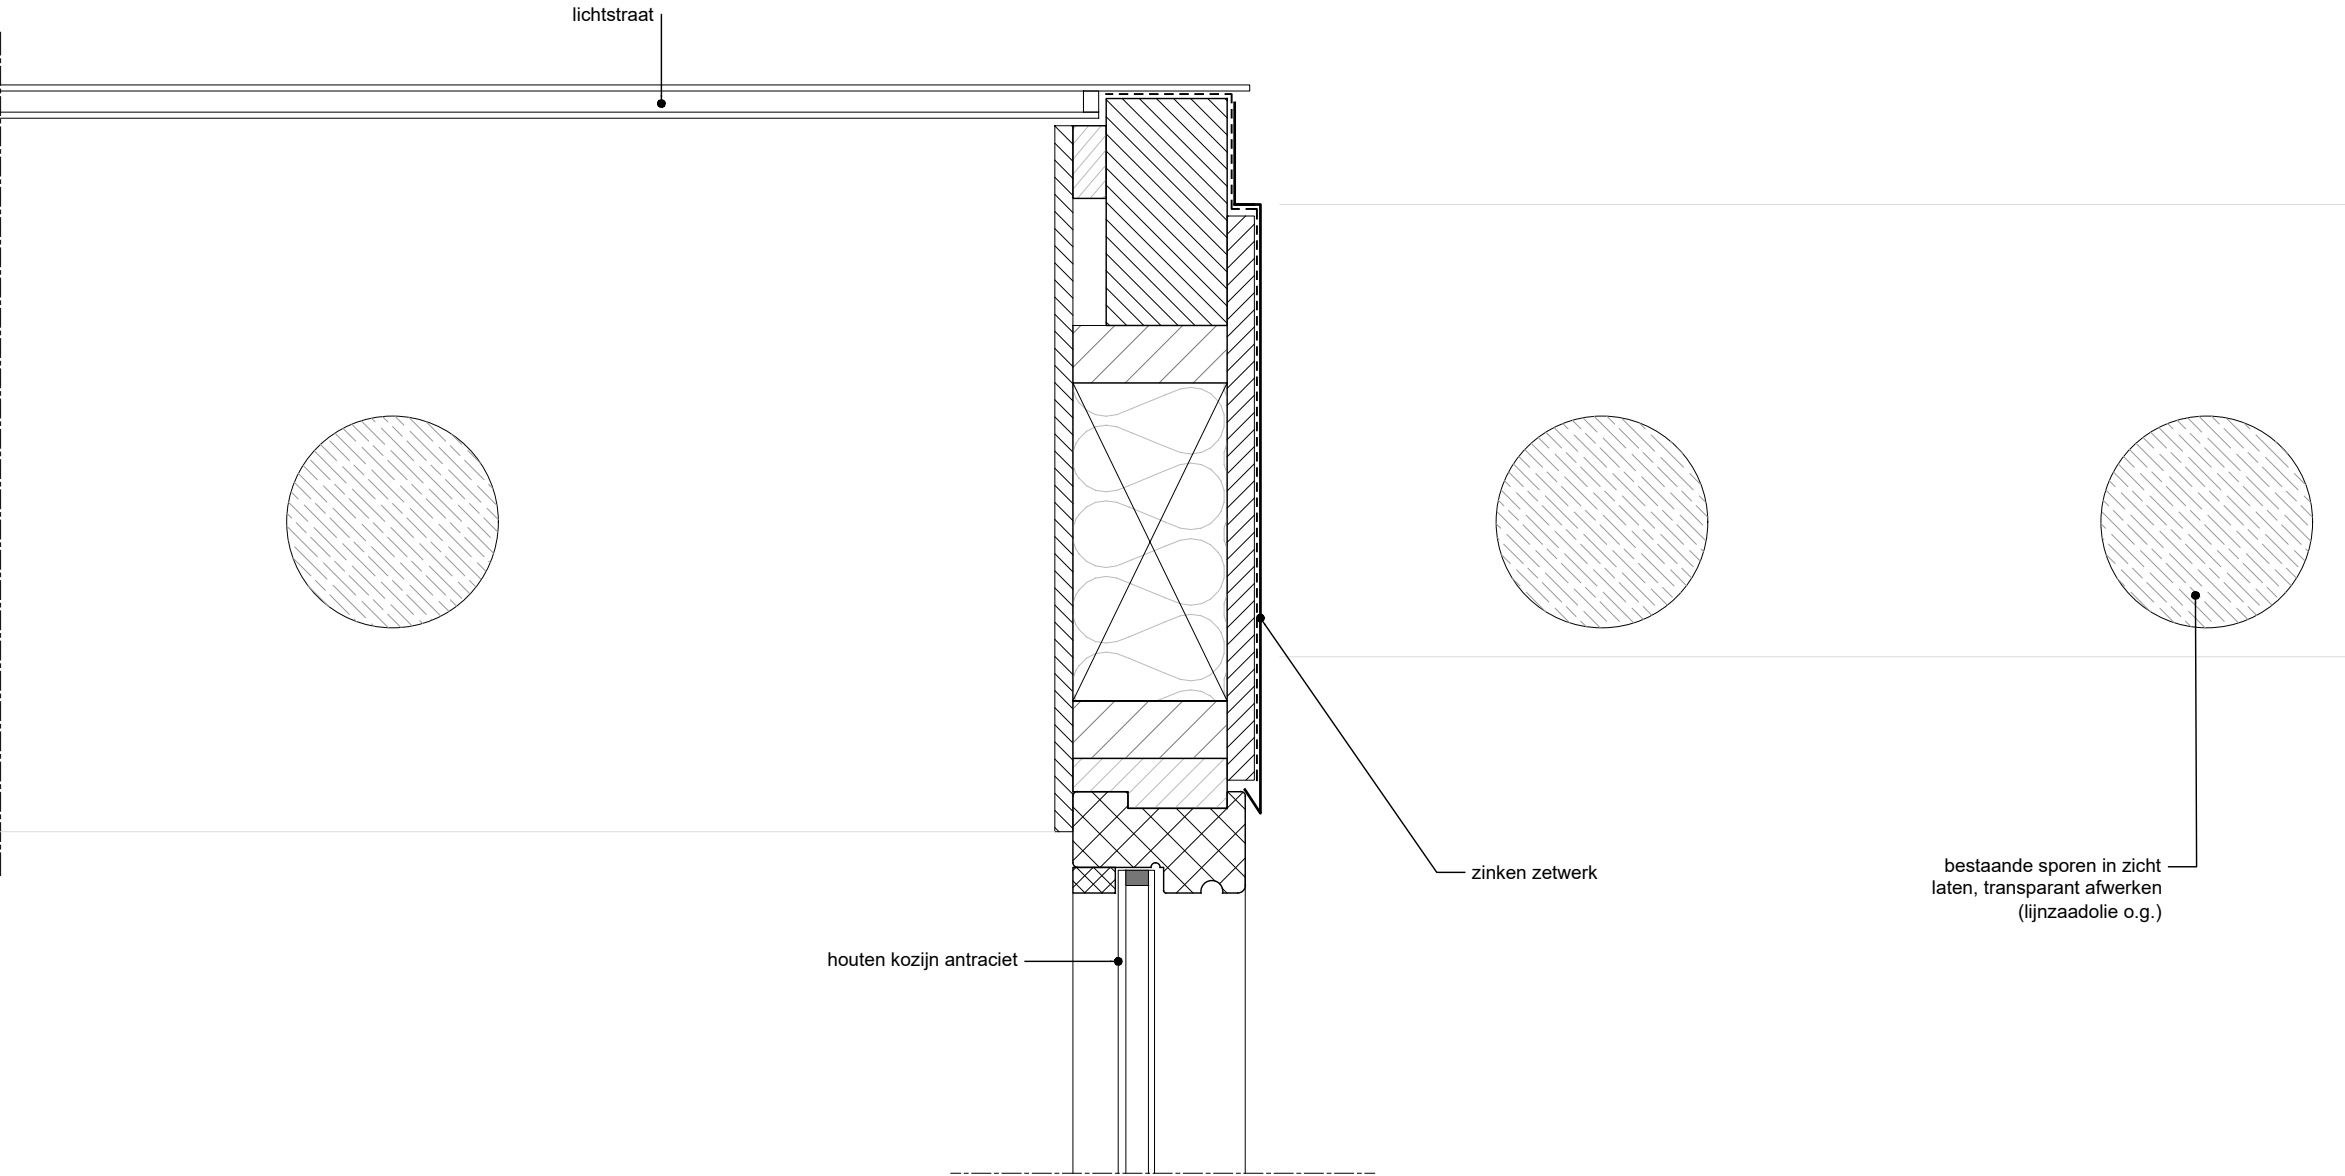


Alle maatvoering in het werk te controleren.
Alle hout-, staal- & betonconstructies volgens constructeur.

Principedetail


project: Verduurzaming en verbouwing | Buzziburglaan 16 | 3972 EE Driebergen
fase: Definitief ontwerp schaal: 1:5 op A3
datum: 03-07-2026 | TtK wijziging:

25-03.DO.414




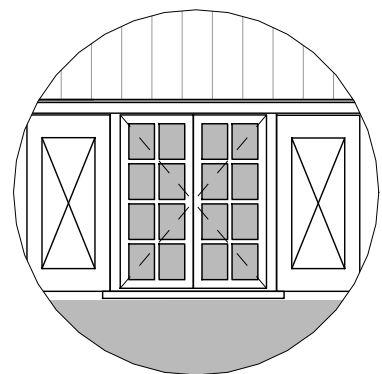

merk B

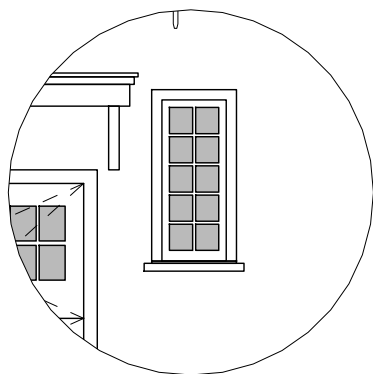


merk G


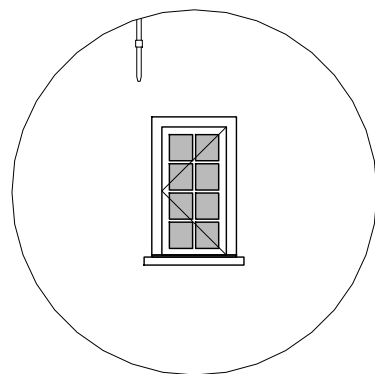


merk H

NIEUW

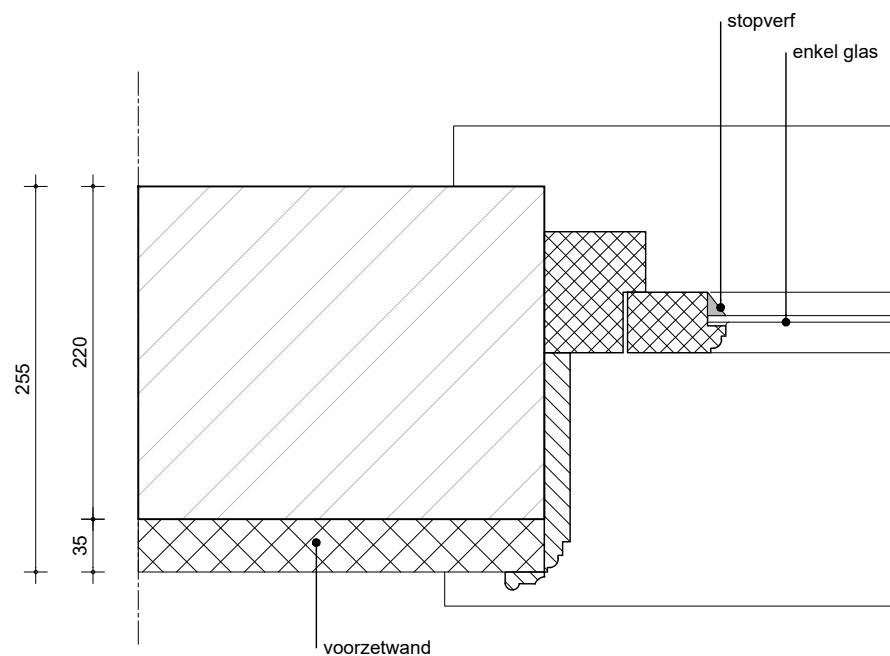

BESTAAND

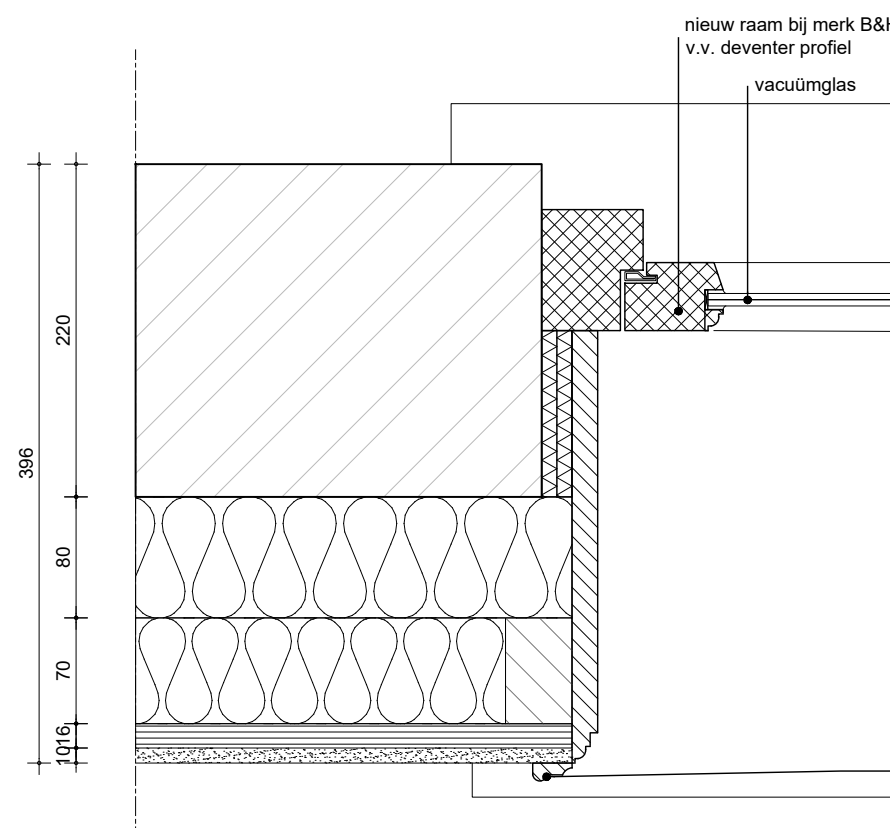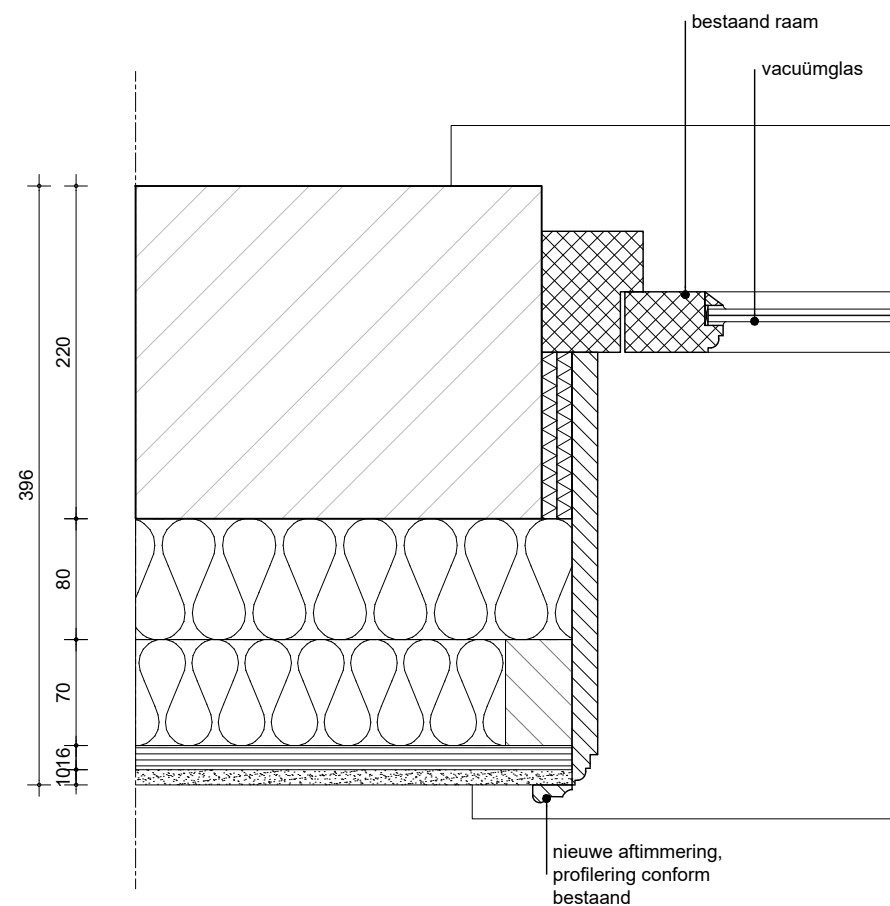

NIEUW

Alle maatvoering in het werk te controleren.
Alle hout-, staal- & betonconstructies volgens constructeur.


Principedetail

project: Verduurzaming en verbouwing | Buzziburglaan 16 | 3972 EE Driebergen
fase: Definitief ontwerp schaal: 1:5 op A3
datum: 03-07-2026 | TtK wijziging:


25-03.DO.510

Kraal architecten BV | Vossegatselaan 32 | 3583 RT Utrecht | 030 223 96 77
www.kraalarchitecten.nl | info@kraalarchitecten.nl




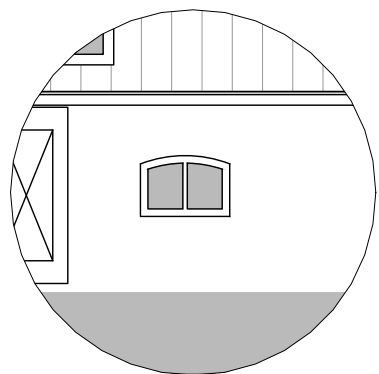


merk C

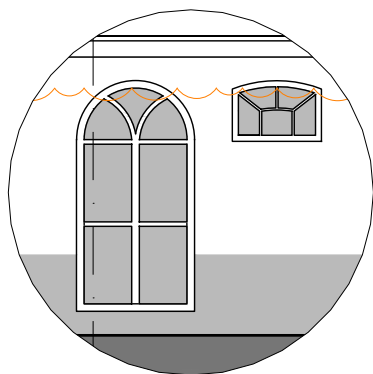

merk O&N

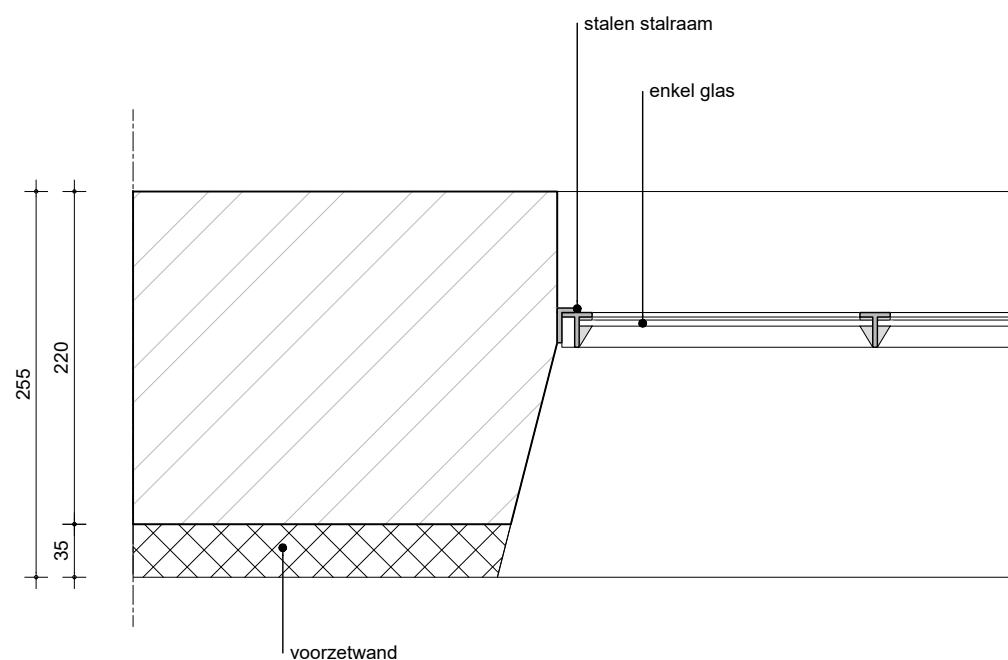

BESTAAND

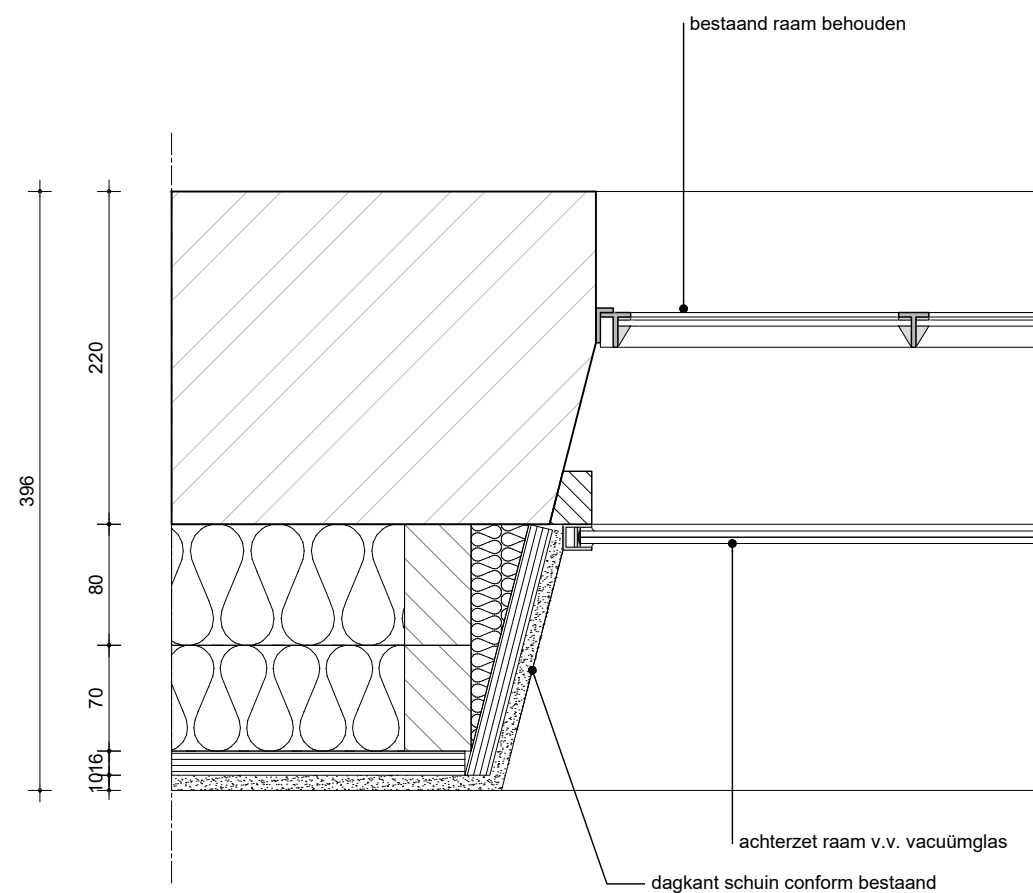

NIEUW

Alle maatvoering in het werk te controleren.
Alle hout-, staal- & betonconstructies volgens constructeur.


Principedetail verduurzaming kozijn

project: Verduurzaming en verbouwing | Buzziburglaan 16 | 3972 EE Driebergen
fase: Definitief ontwerp schaal: 1:5 op A3
datum: 03-07-2026 | TtK wijziging:


25-03.DO.511

Kraal architecten BV | Vossegatselaan 32 | 3583 RT Utrecht | 030 223 96 77
www.kraalarchitecten.nl | info@kraalarchitecten.nl




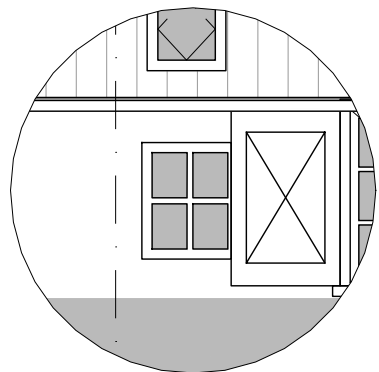

merk D

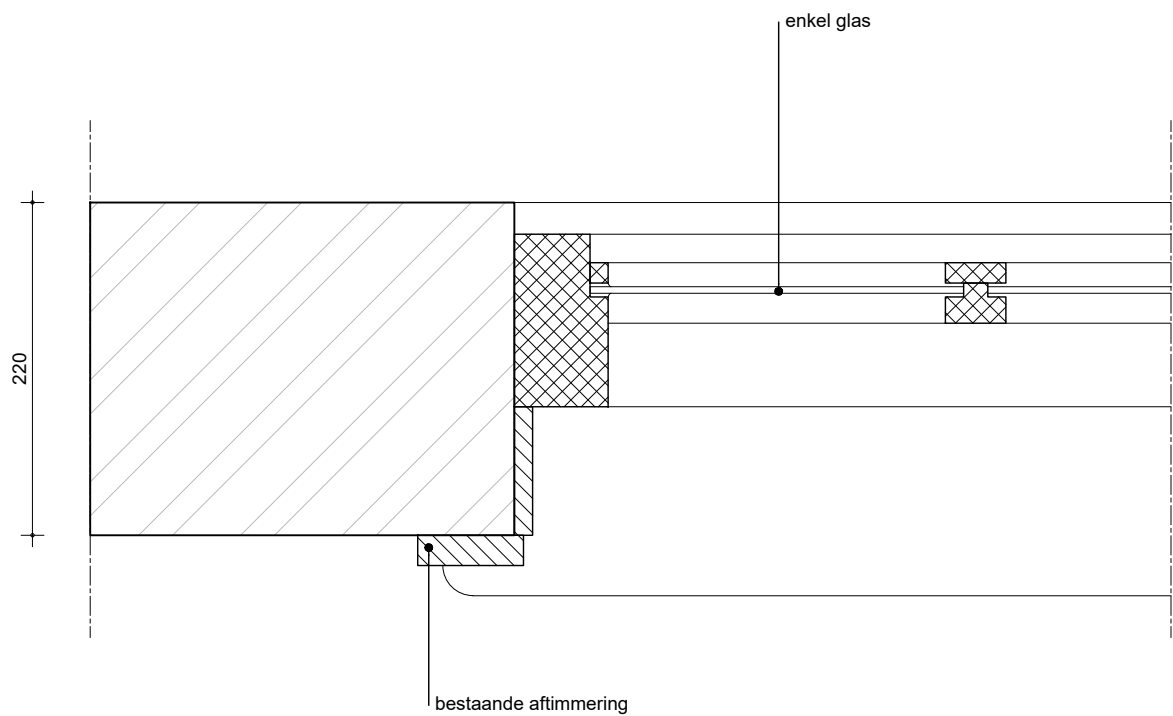

BESTAAND

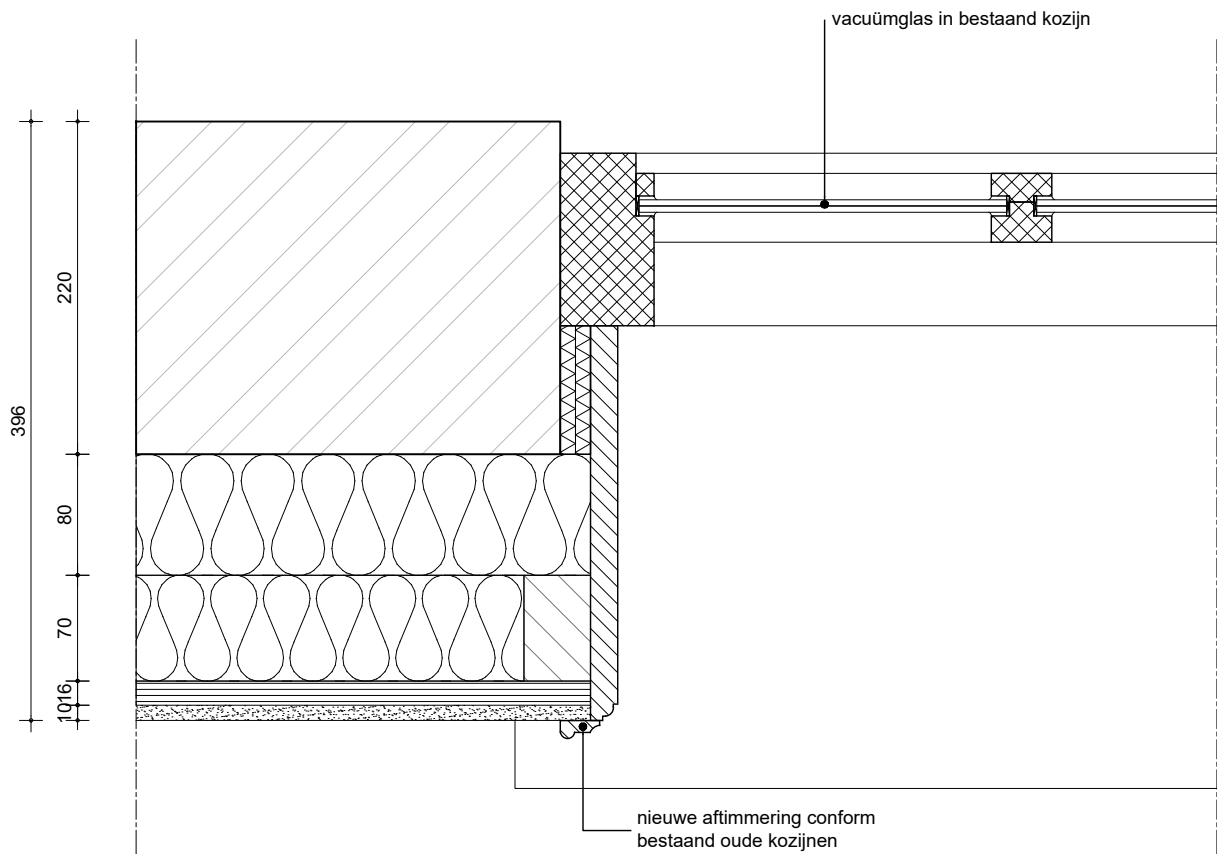

NIEUW

Alle maatvoering in het werk te controleren.
Alle hout-, staal- & betonconstructies volgens constructeur.


Principedetail verduurzaming kozijn

project: Verduurzaming en verbouwing | Buzziburglaan 16 | 3972 EE Driebergen
fase: Definitief ontwerp schaal: 1:5 op A3
datum: 03-07-2026 | TtK wijziging:


25-03.DO.512

Kraal architecten BV | Vossegatselaan 32 | 3583 RT Utrecht | 030 223 96 77
www.kraalarchitecten.nl | info@kraalarchitecten.nl




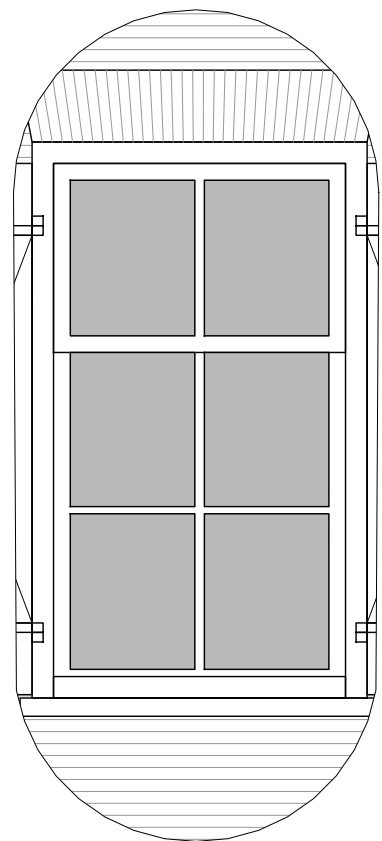

merk I

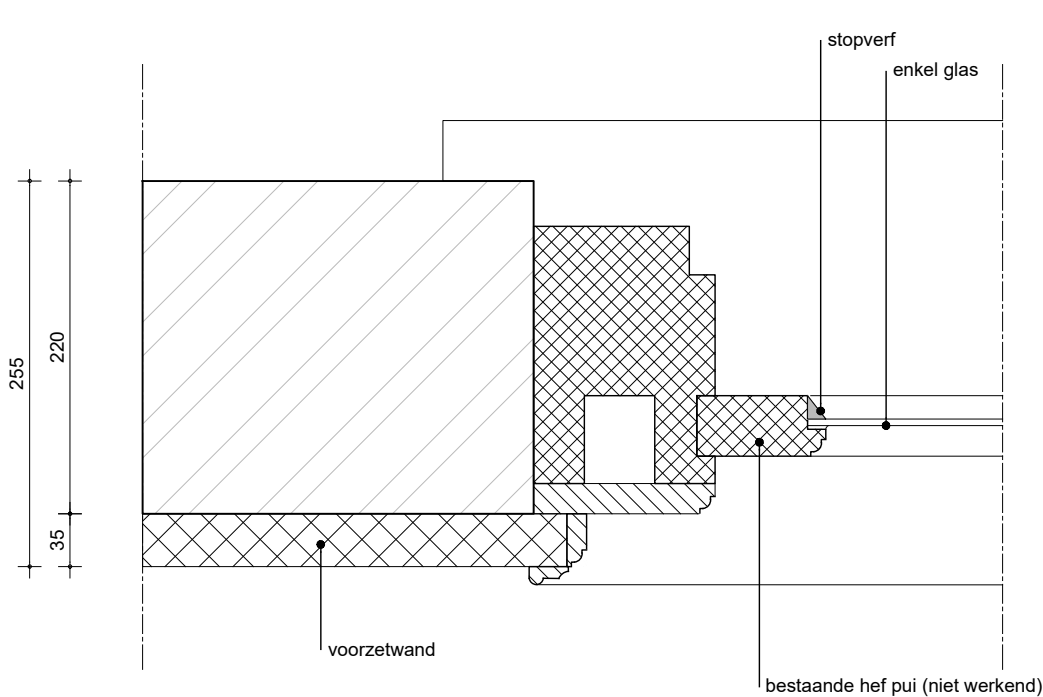

BESTAAND

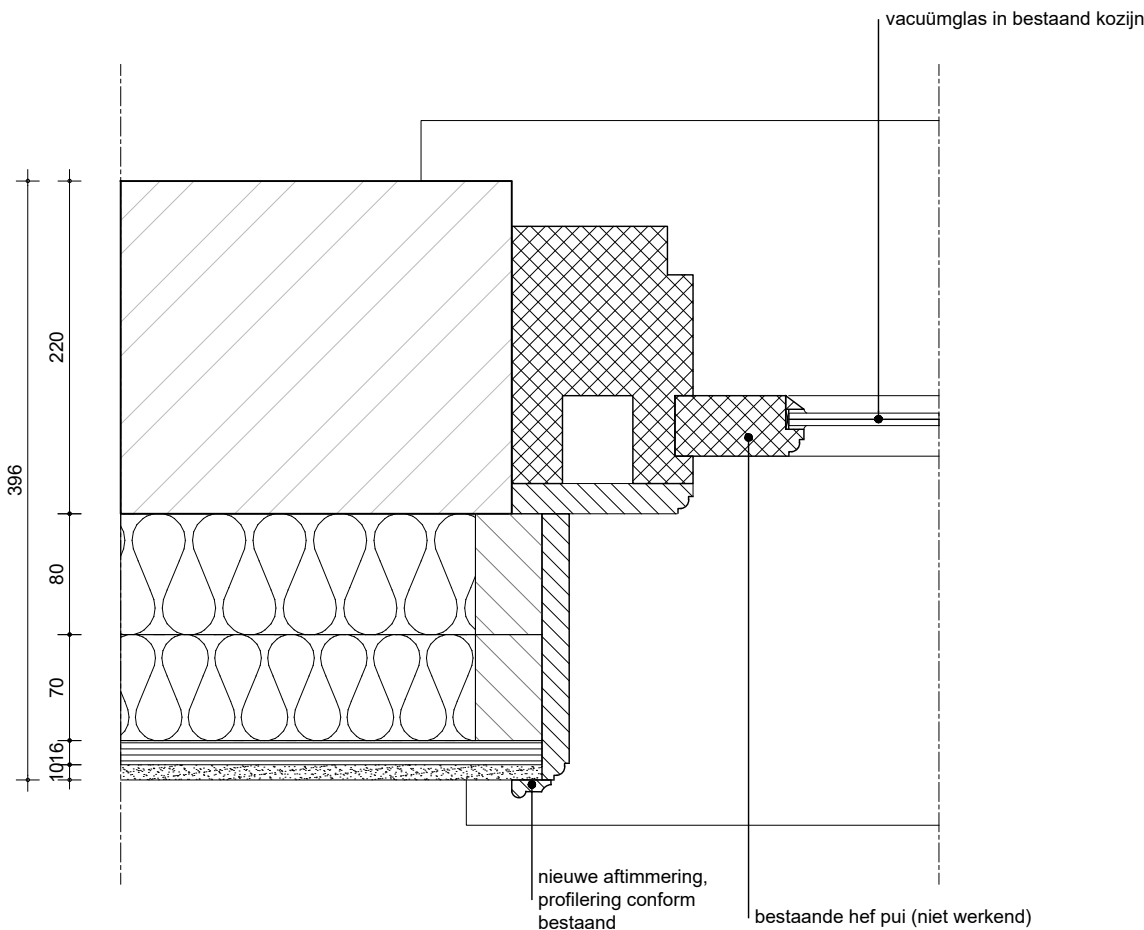

NIEUW

Alle maatvoering in het werk te controleren.
Alle hout-, staal- & betonconstructies volgens constructeur.


Principedetail verduurzaming kozijn

project: Verduurzaming en verbouwing | Buzziburglaan 16 | 3972 EE Driebergen
fase: Definitief ontwerp schaal: 1:5 op A3
datum: 03-07-2026 | TtK wijziging:


25-03.DO.513

Kraal architecten BV | Vossegatselaan 32 | 3583 RT Utrecht | 030 223 96 77
www.kraalarchitecten.nl | info@kraalarchitecten.nl




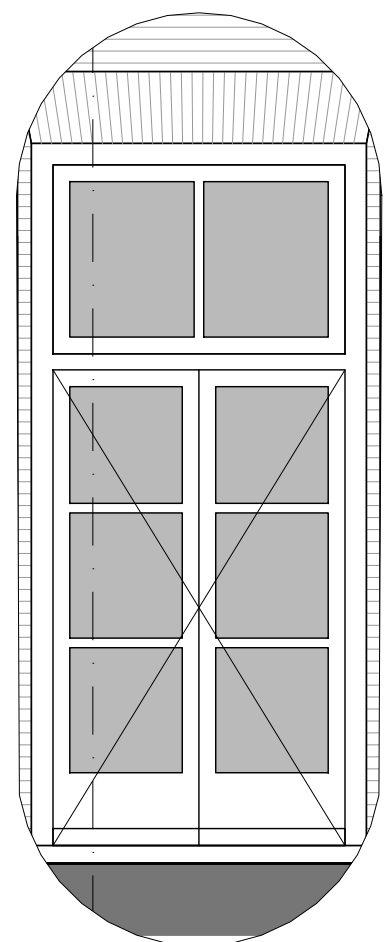


merk I

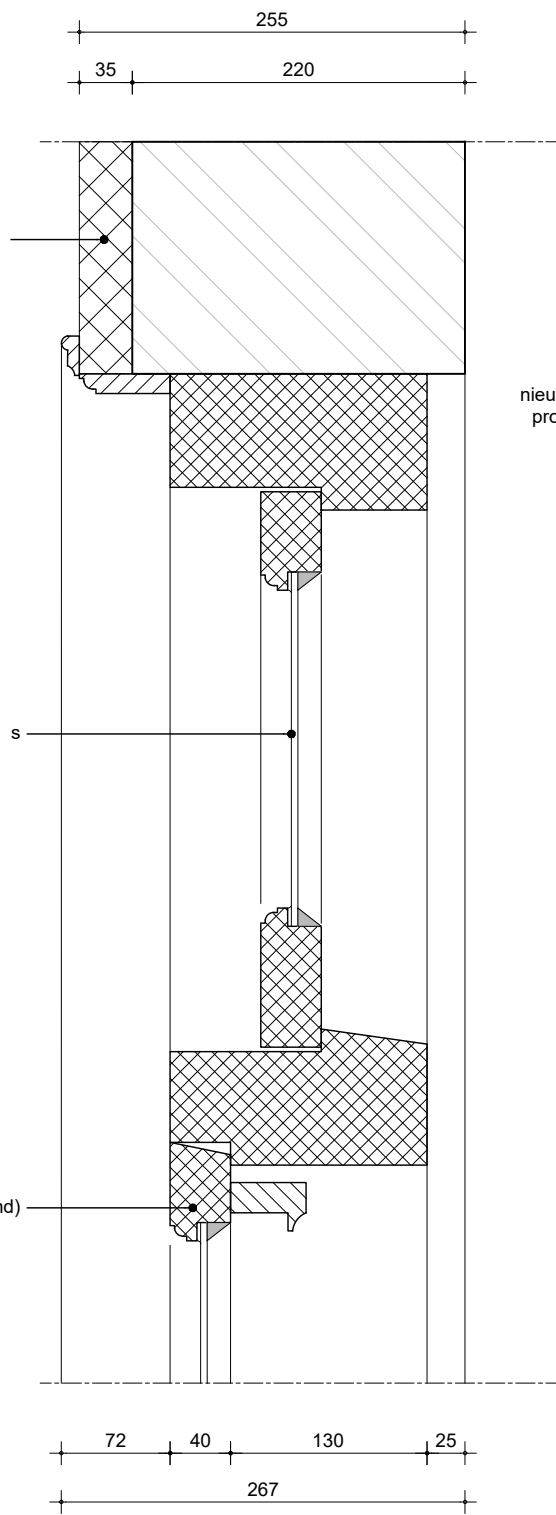

BESTAAND

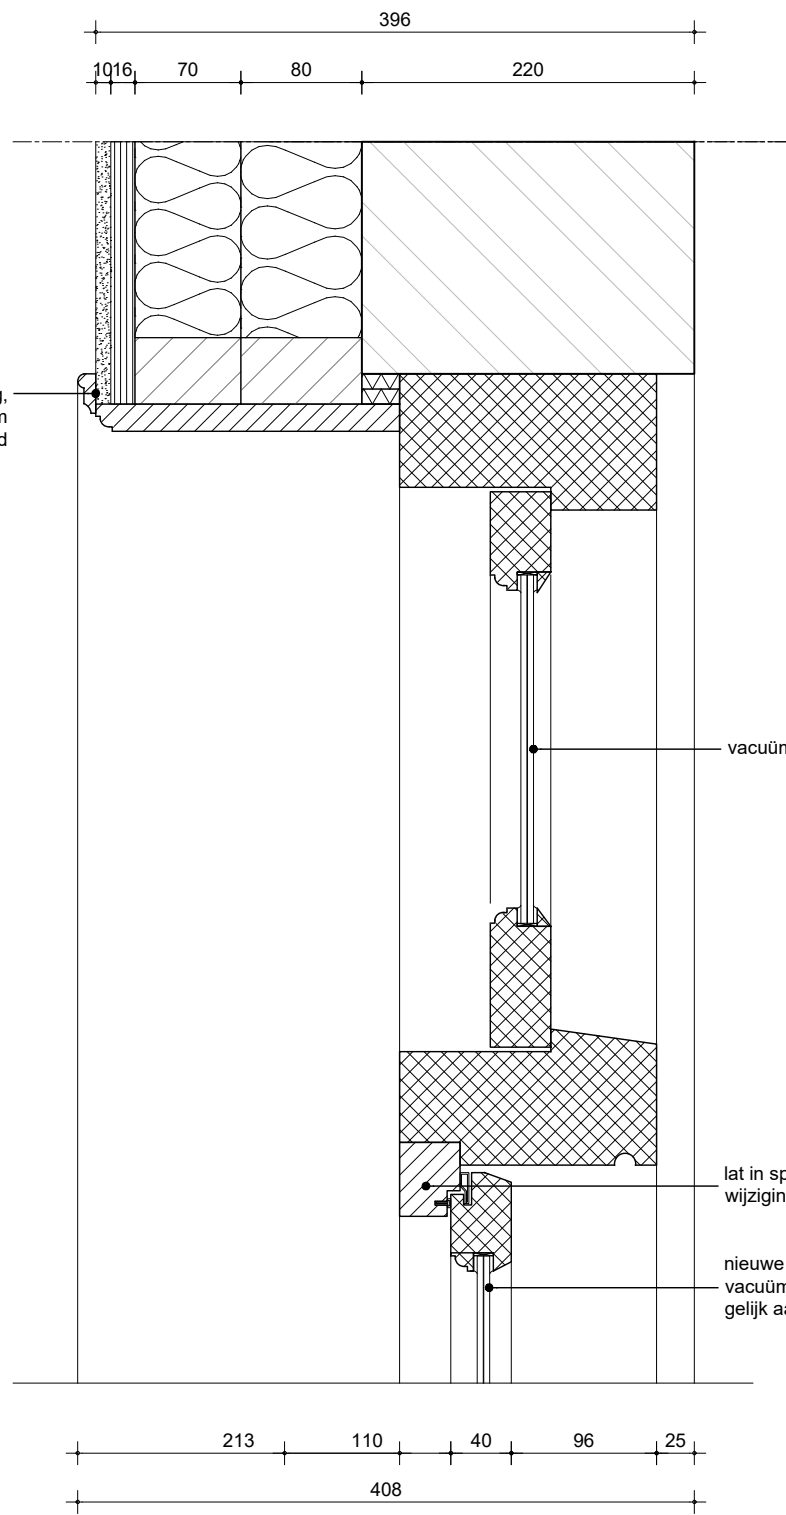

NIEUW

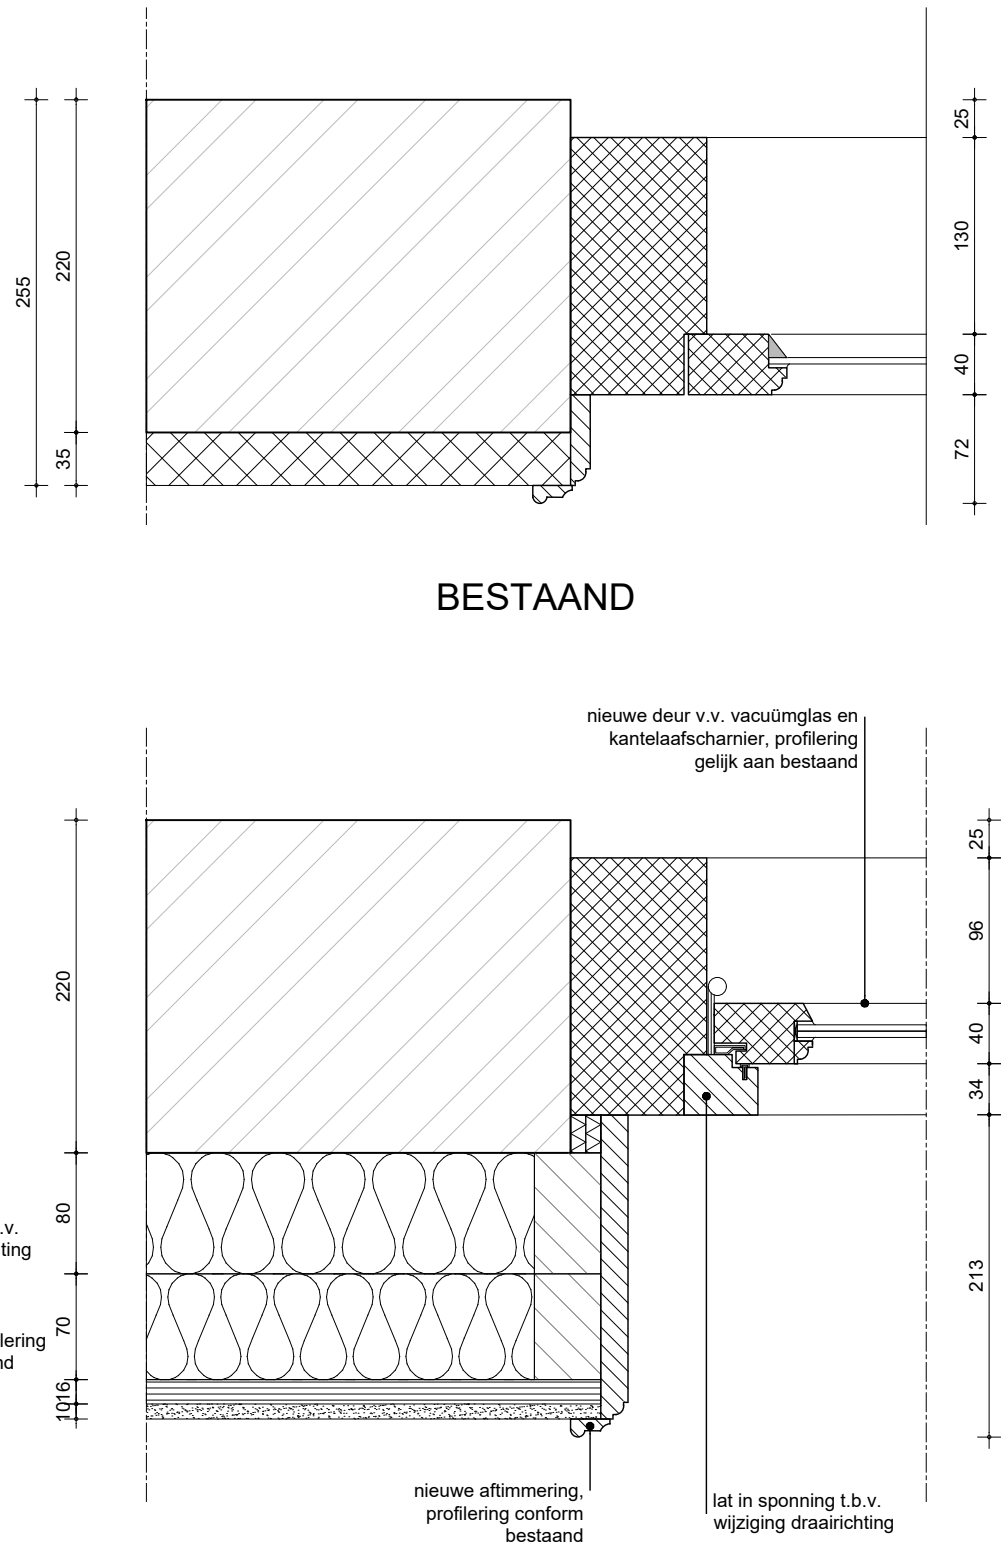

NIEUW

Alle maatvoering in het werk te controleren.
Alle hout-, staal- & betonconstructies volgens constructeur.


Principedetail verduurzaming kozijn

project: Verduurzaming en verbouwing | Buzziburglaan 16 | 3972 EE Driebergen
fase: Definitief ontwerp schaal: 1:5 op A3
datum: 03-07-2026 | TtK wijziging:


25-03.DO.514

Kraal architecten BV | Vossegatselaan 32 | 3583 RT Utrecht | 030 223 96 77
www.kraalarchitecten.nl | info@kraalarchitecten.nl




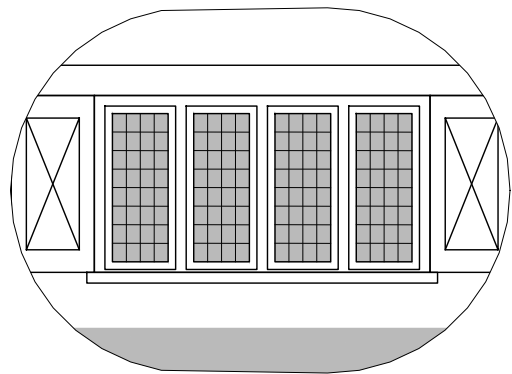

merk K

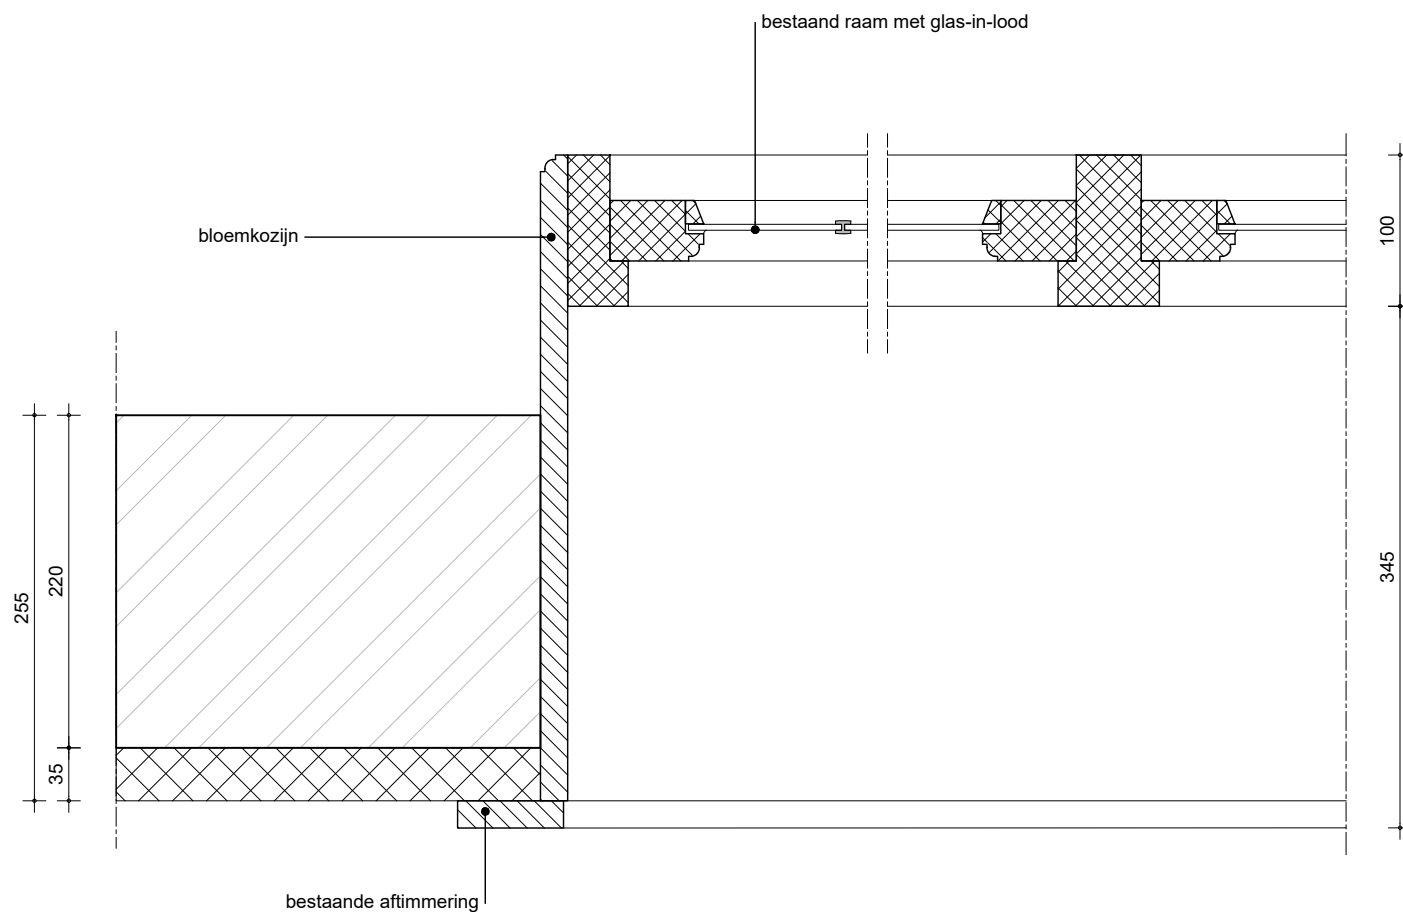

BESTAAND

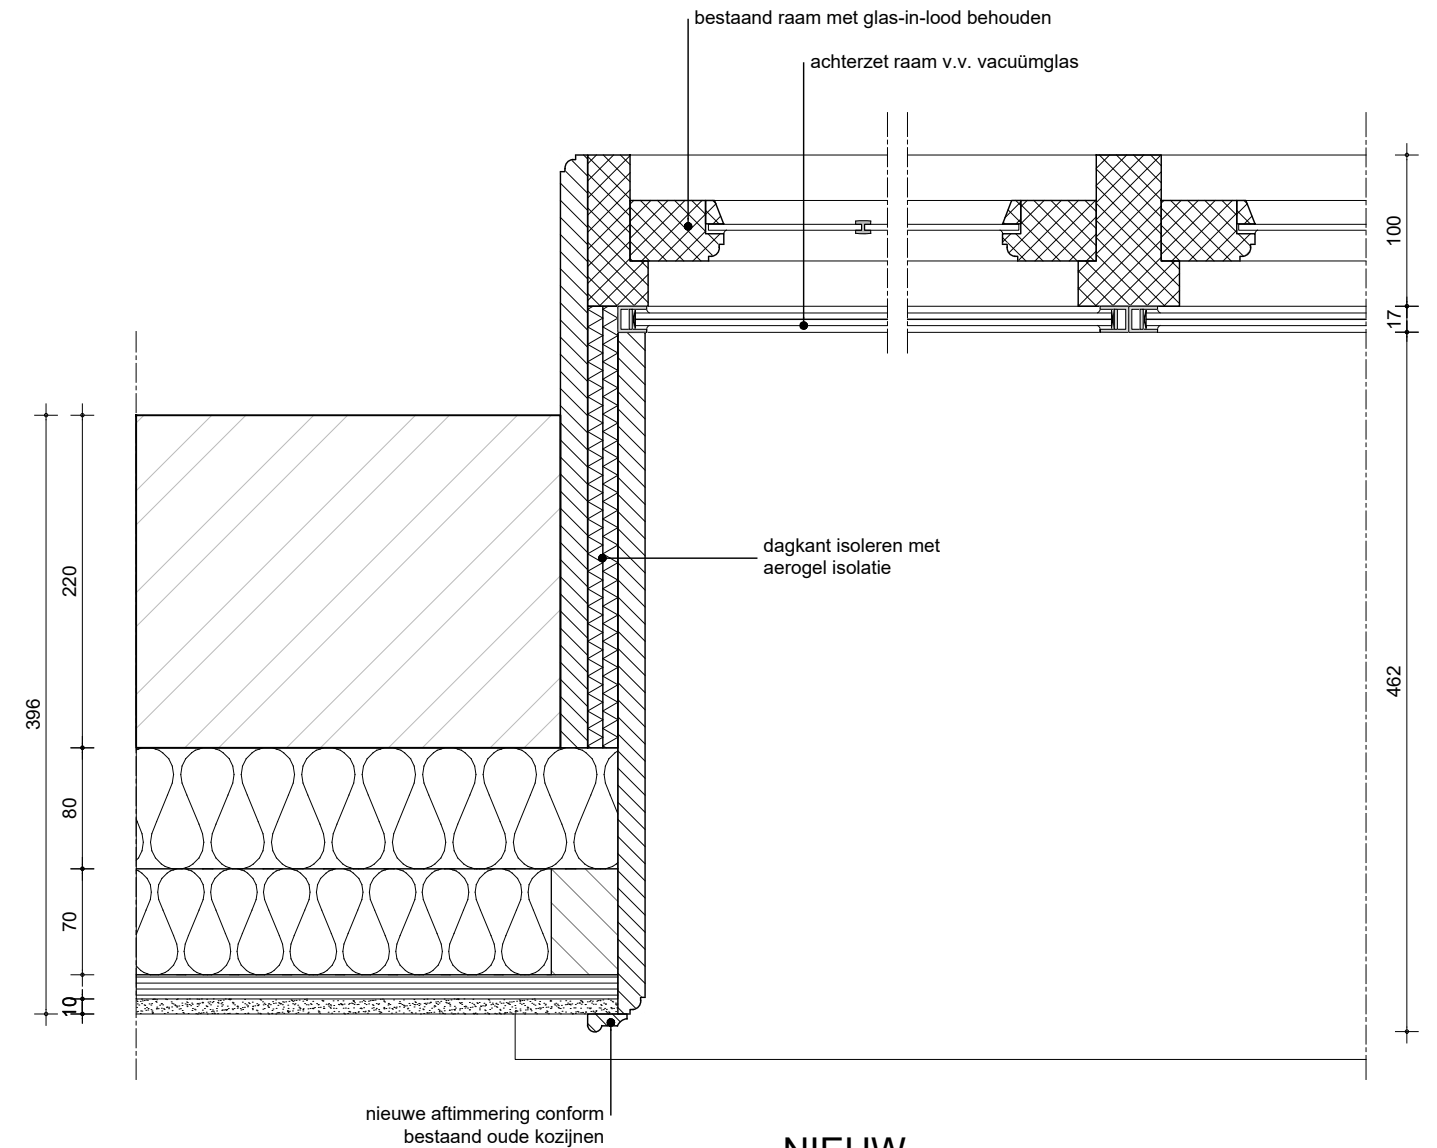

NIEUW

Alle maatvoering in het werk te controleren.
Alle hout-, staal- & betonconstructies volgens constructeur.


Principedetail verduurzaming kozijn

project: Verduurzaming en verbouwing | Buzziburglaan 16 | 3972 EE Driebergen
fase: Definitief ontwerp schaal: 1:5 op A3
datum: 03-07-2026 | TtK wijziging:


25-03.DO.515

Kraal architecten BV | Vossegatselaan 32 | 3583 RT Utrecht | 030 223 96 77
www.kraalarchitecten.nl | info@kraalarchitecten.nl




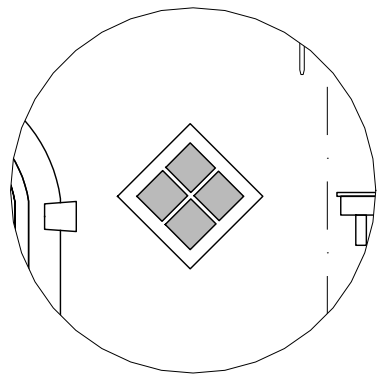

merk P

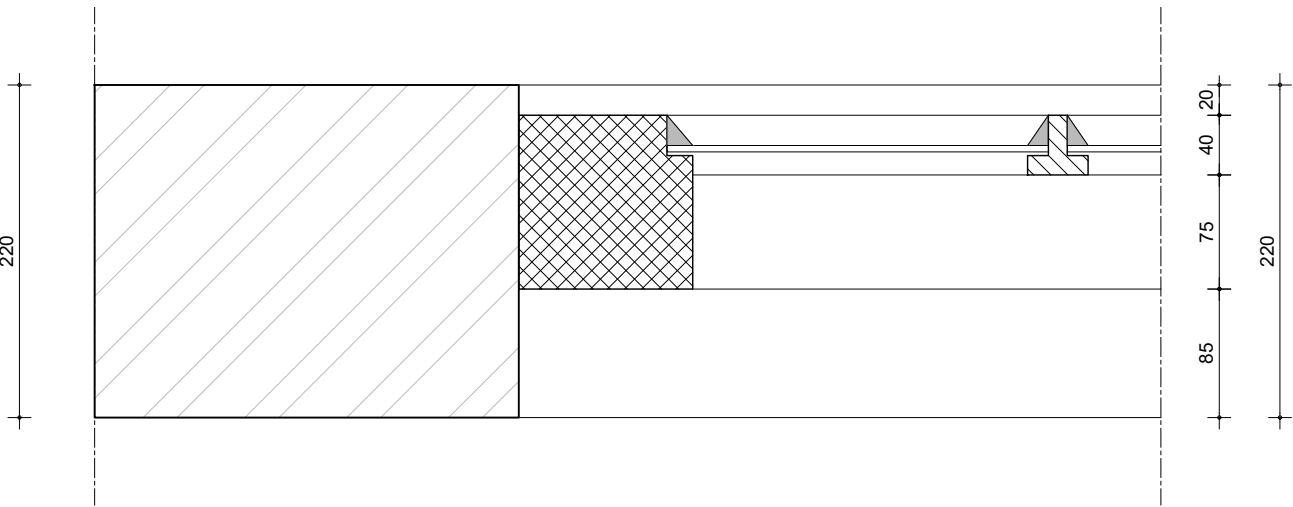

BESTAAND

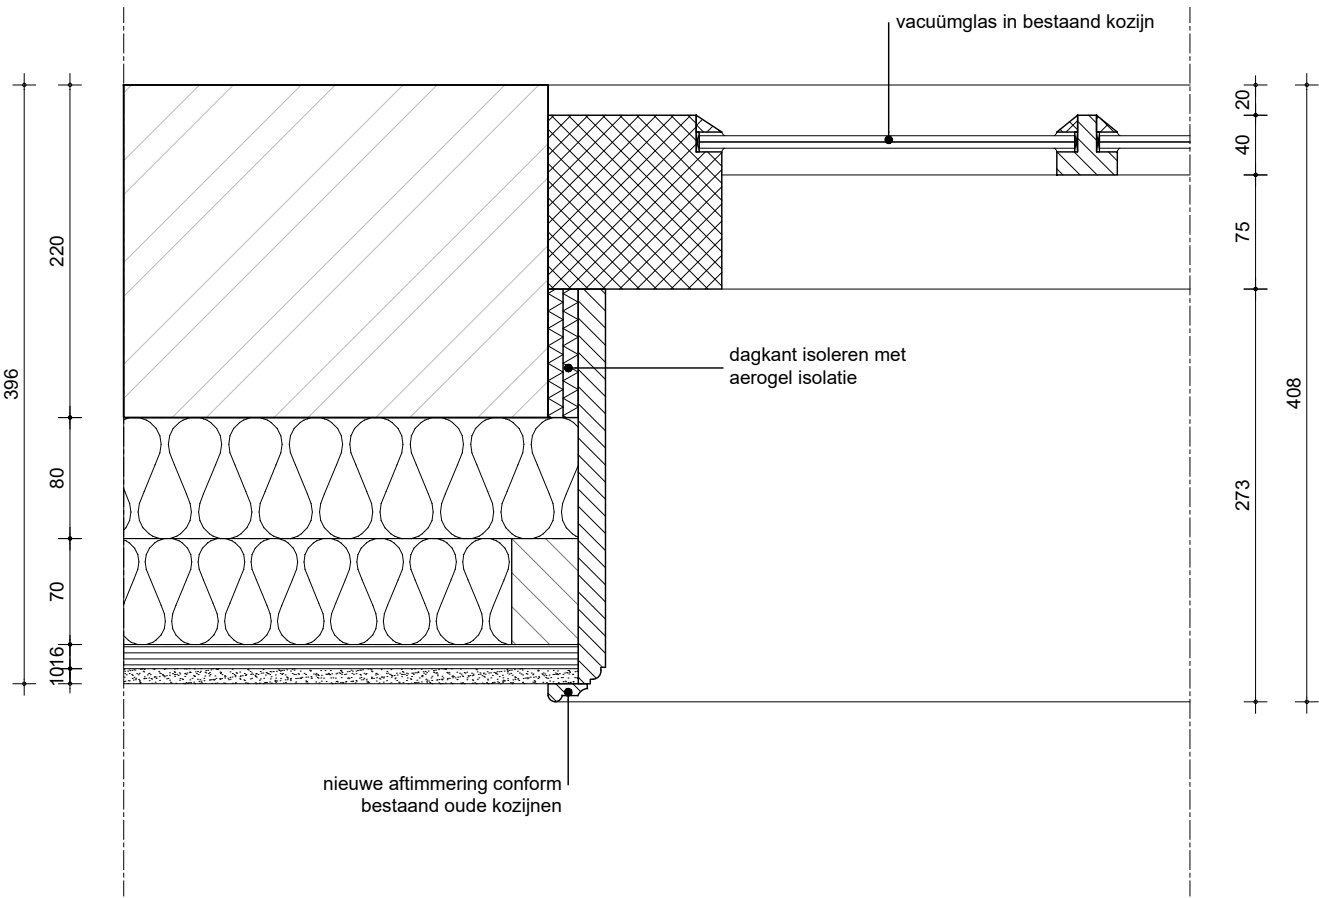

NIEUW

Alle maatvoering in het werk te controleren.
Alle hout-, staal- & betonconstructies volgens constructeur.


Principedetail verduurzaming kozijn

project: Verduurzaming en verbouwing | Buzziburglaan 16 | 3972 EE Driebergen
fase: Definitief ontwerp schaal: 1:5 op A3
datum: 03-07-2026 | TtK wijziging:

25-03.DO.516


Kraal architecten BV | Vossegatselaan 32 | 3583 RT Utrecht | 030 223 96 77
www.kraalarchitecten.nl | info@kraalarchitecten.nl



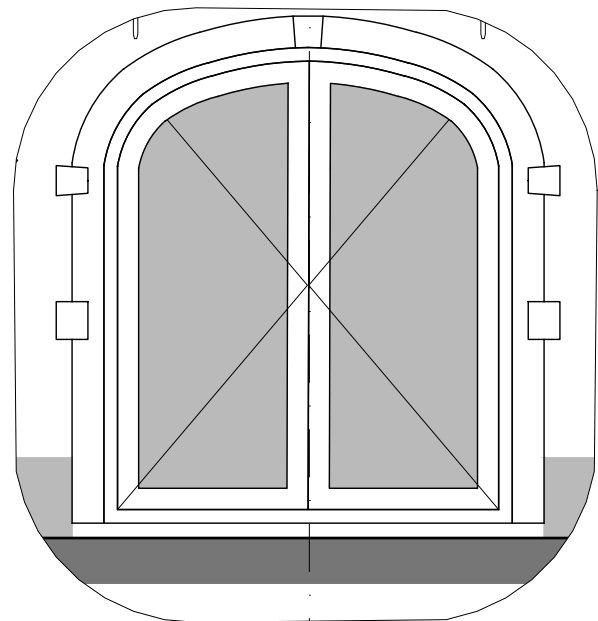


merk Q


220
115

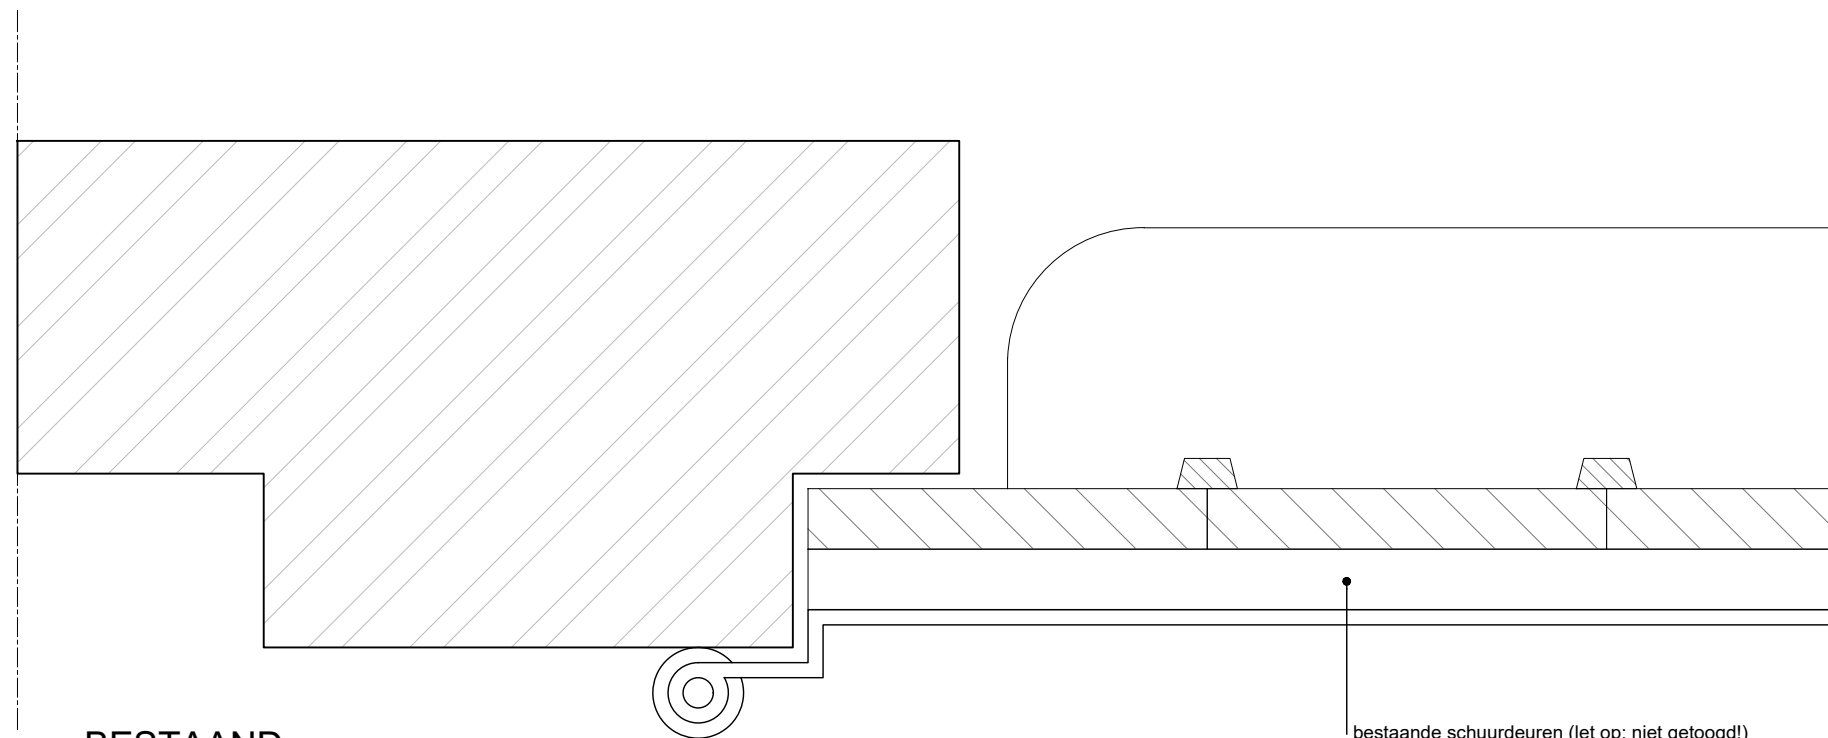

BESTAAND

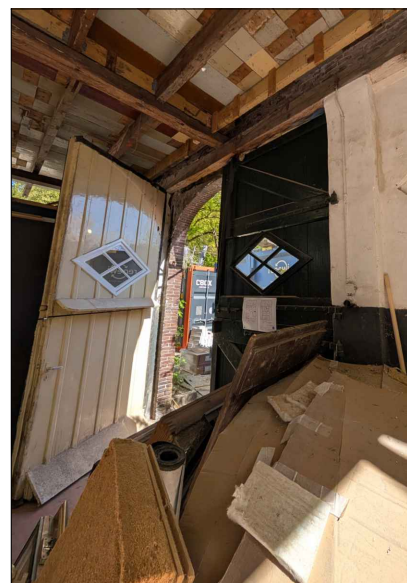

396
220
80
70
1016

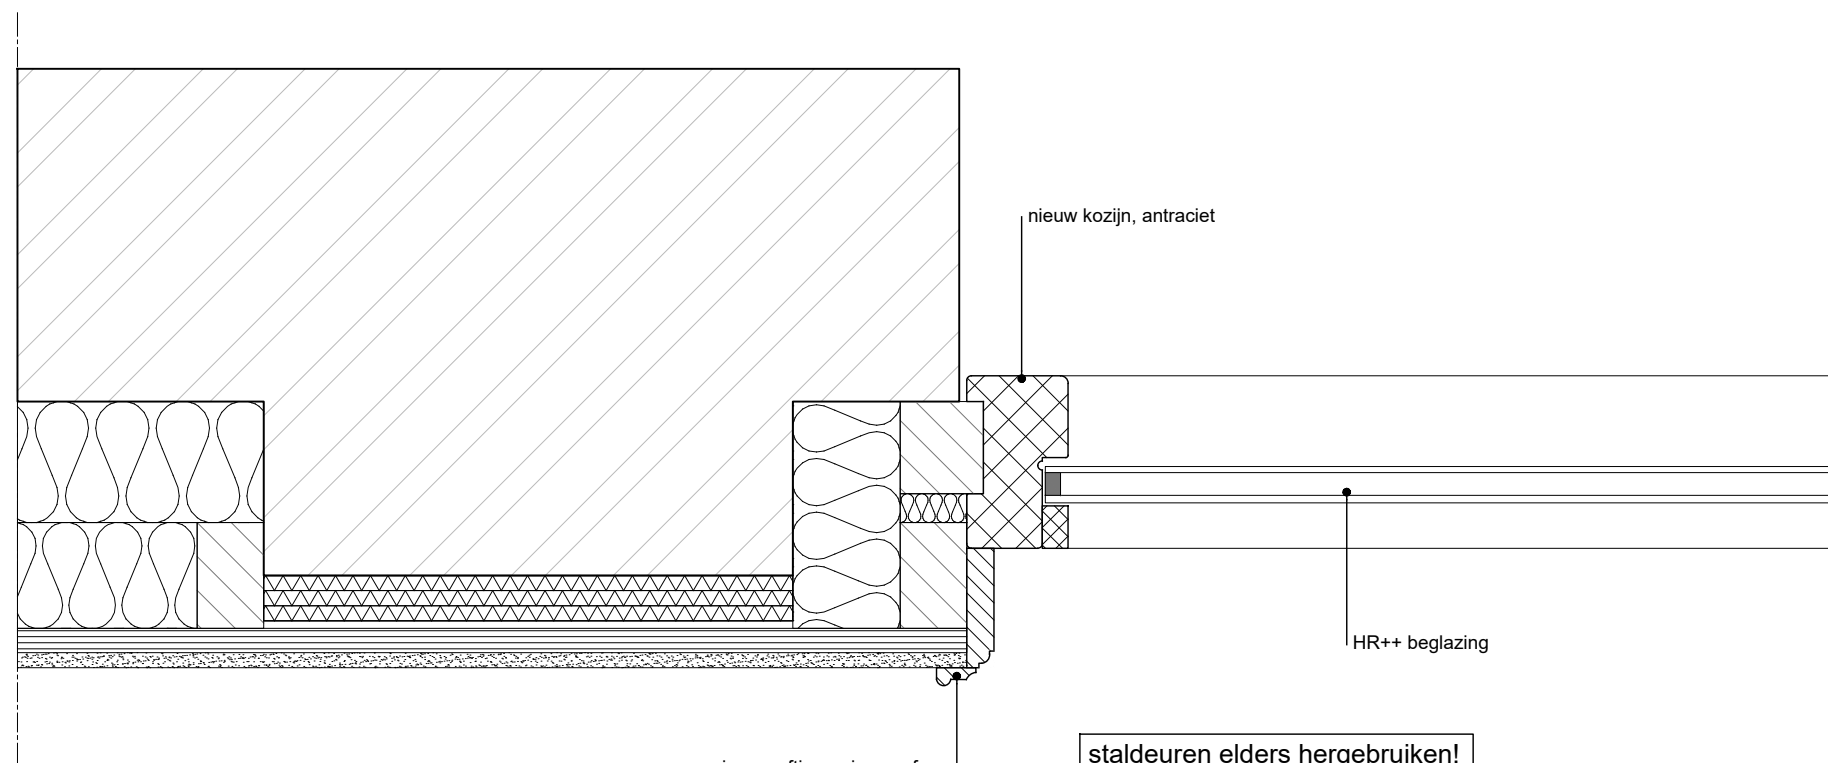

NIEUW

Alle maatvoering in het werk te controleren.
Alle hout-, staal- & betonconstructies volgens constructeur.


Principedetail verduurzaming kozijn

project: Verduurzaming en verbouwing | Buzziburglaan 16 | 3972 EE Driebergen
fase: Definitief ontwerp
datum: 03-07-2026 | TtK
schaal: 1:5 op A3
wijziging:


25-03.DO.517

Kraal architecten BV | Vossegatselaan 32 | 3583 RT Utrecht | 030 223 96 77
www.kraalarchitecten.nl | info@kraalarchitecten.nl




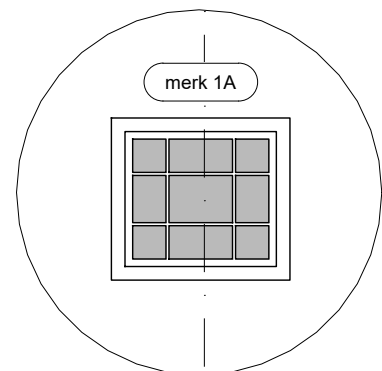

merk 1A

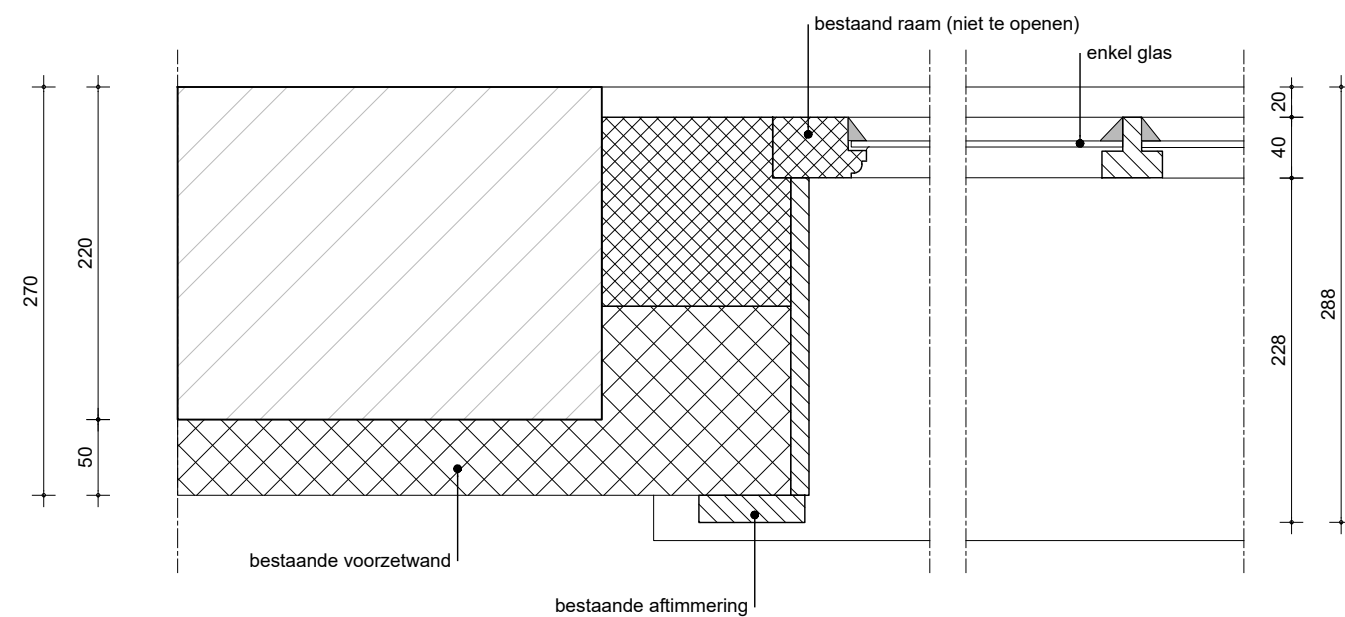

BESTAAND

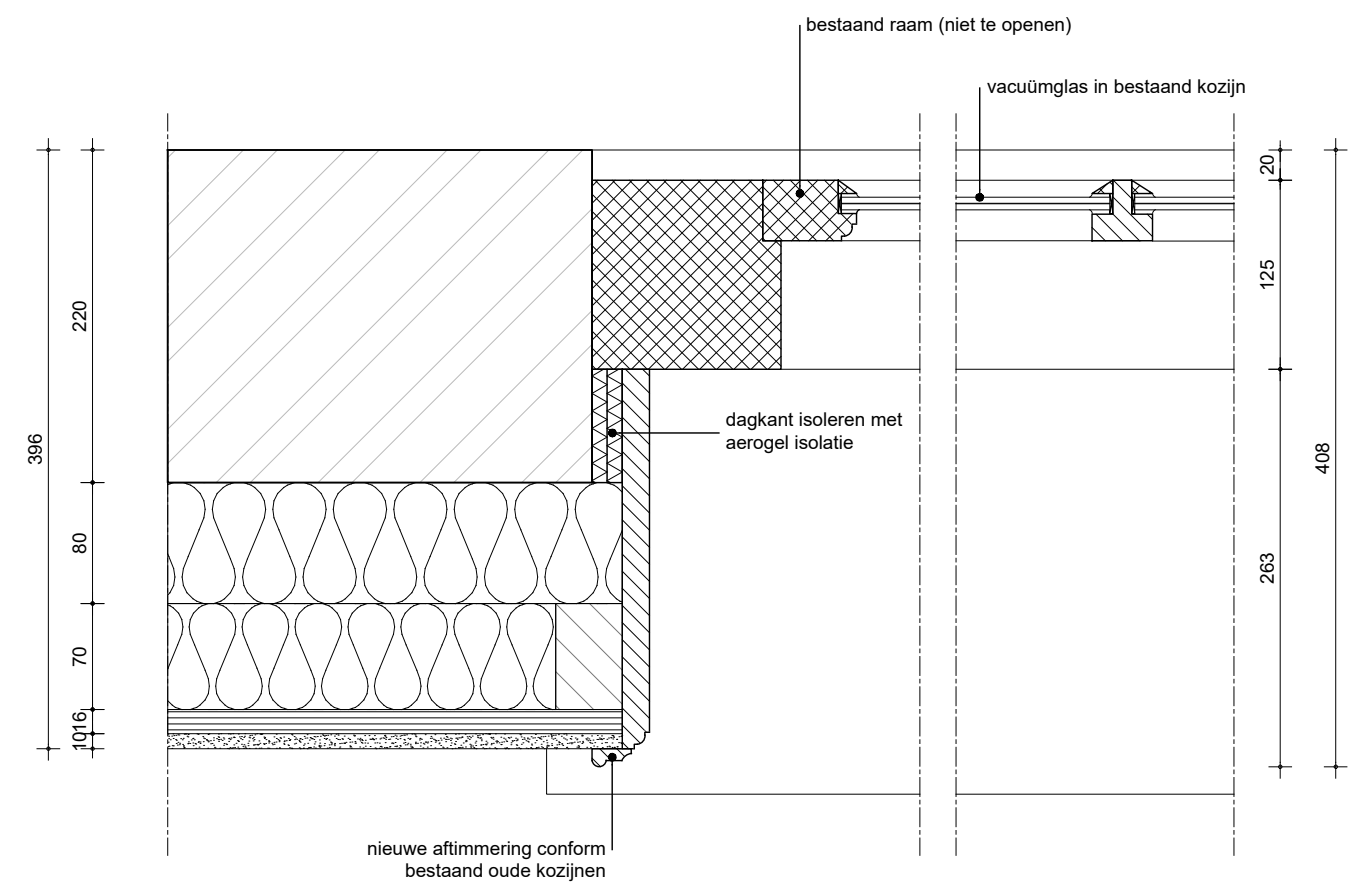

NIEUW

Alle maatvoering in het werk te controleren.
Alle hout-, staal- & betonconstructies volgens constructeur.


Principedetail verduurzaming kozijn

project: Verduurzaming en verbouwing | Buzziburglaan 16 | 3972 EE Driebergen
fase: Definitief ontwerp schaal: 1:5 op A3
datum: 03-07-2026 | TtK wijziging:



25-03.DO.518

Kraal architecten BV | Vossegatselaan 32 | 3583 RT Utrecht | 030 223 96 77
www.kraalarchitecten.nl | info@kraalarchitecten.nl





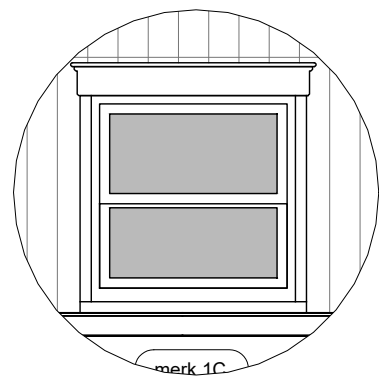

merk 1C

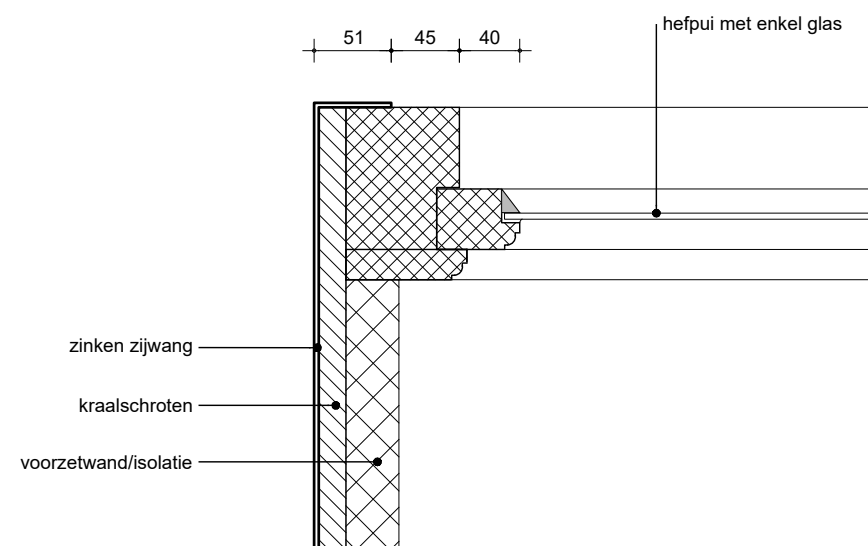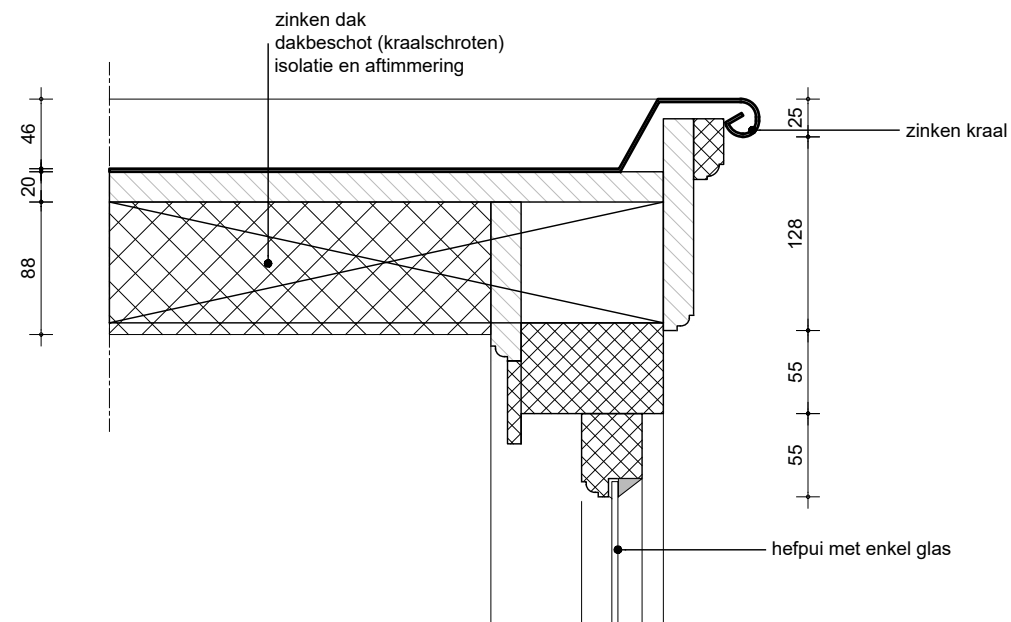

BESTAAND

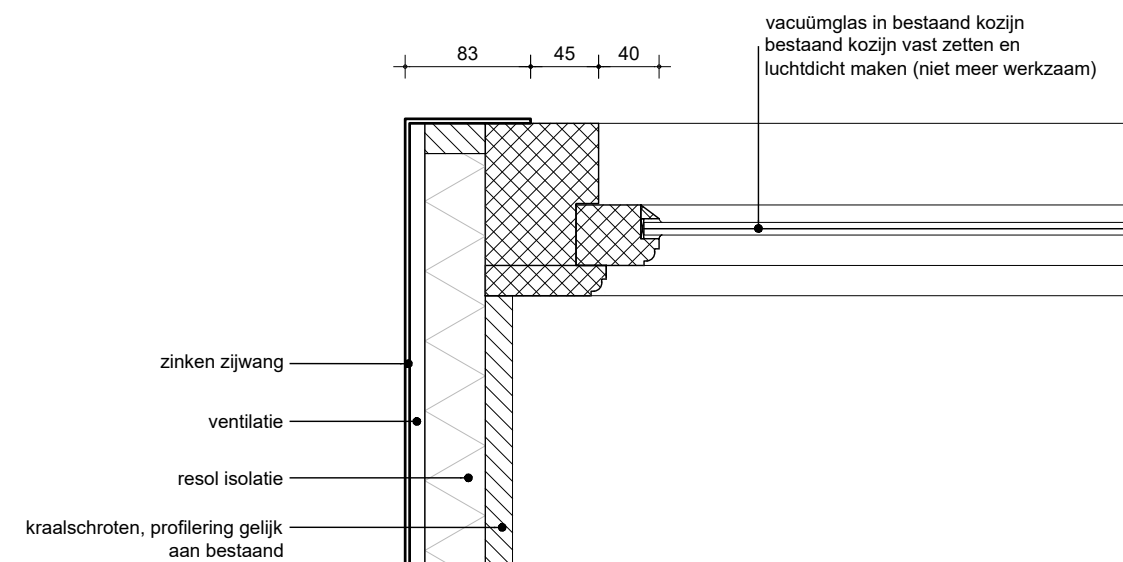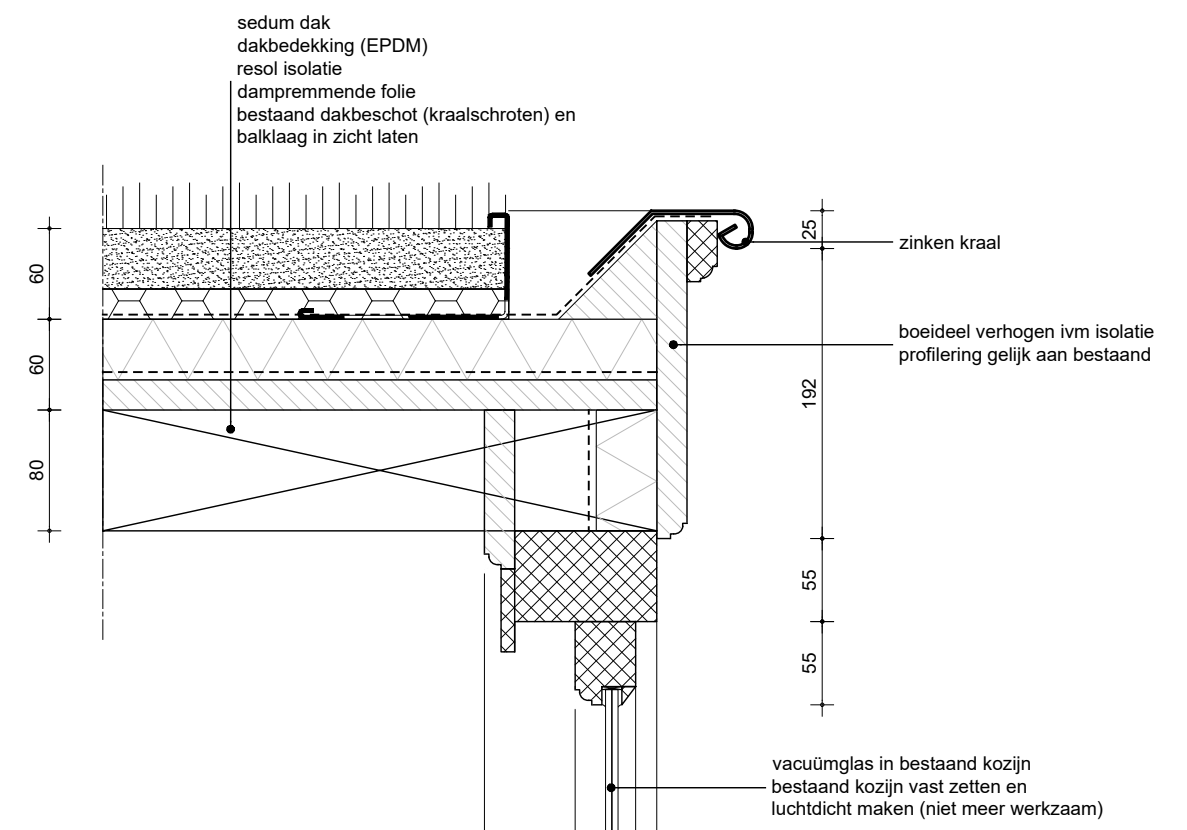

NIEUW

Alle maatvoering in het werk te controleren.
Alle hout-, staal- & betonconstructies volgens constructeur.


Principedetail verduurzaming kozijn

project: Verduurzaming en verbouwing | Buzziburglaan 16 | 3972 EE Driebergen
fase: Definitief ontwerp schaal: 1:5 op A3
datum: 03-07-2026 | TtK wijziging:

25-03.DO.519

Kraal architecten BV | Vossegatselaan 32 | 3583 RT Utrecht | 030 223 96 77
www.kraalarchitecten.nl | info@kraalarchitecten.nl



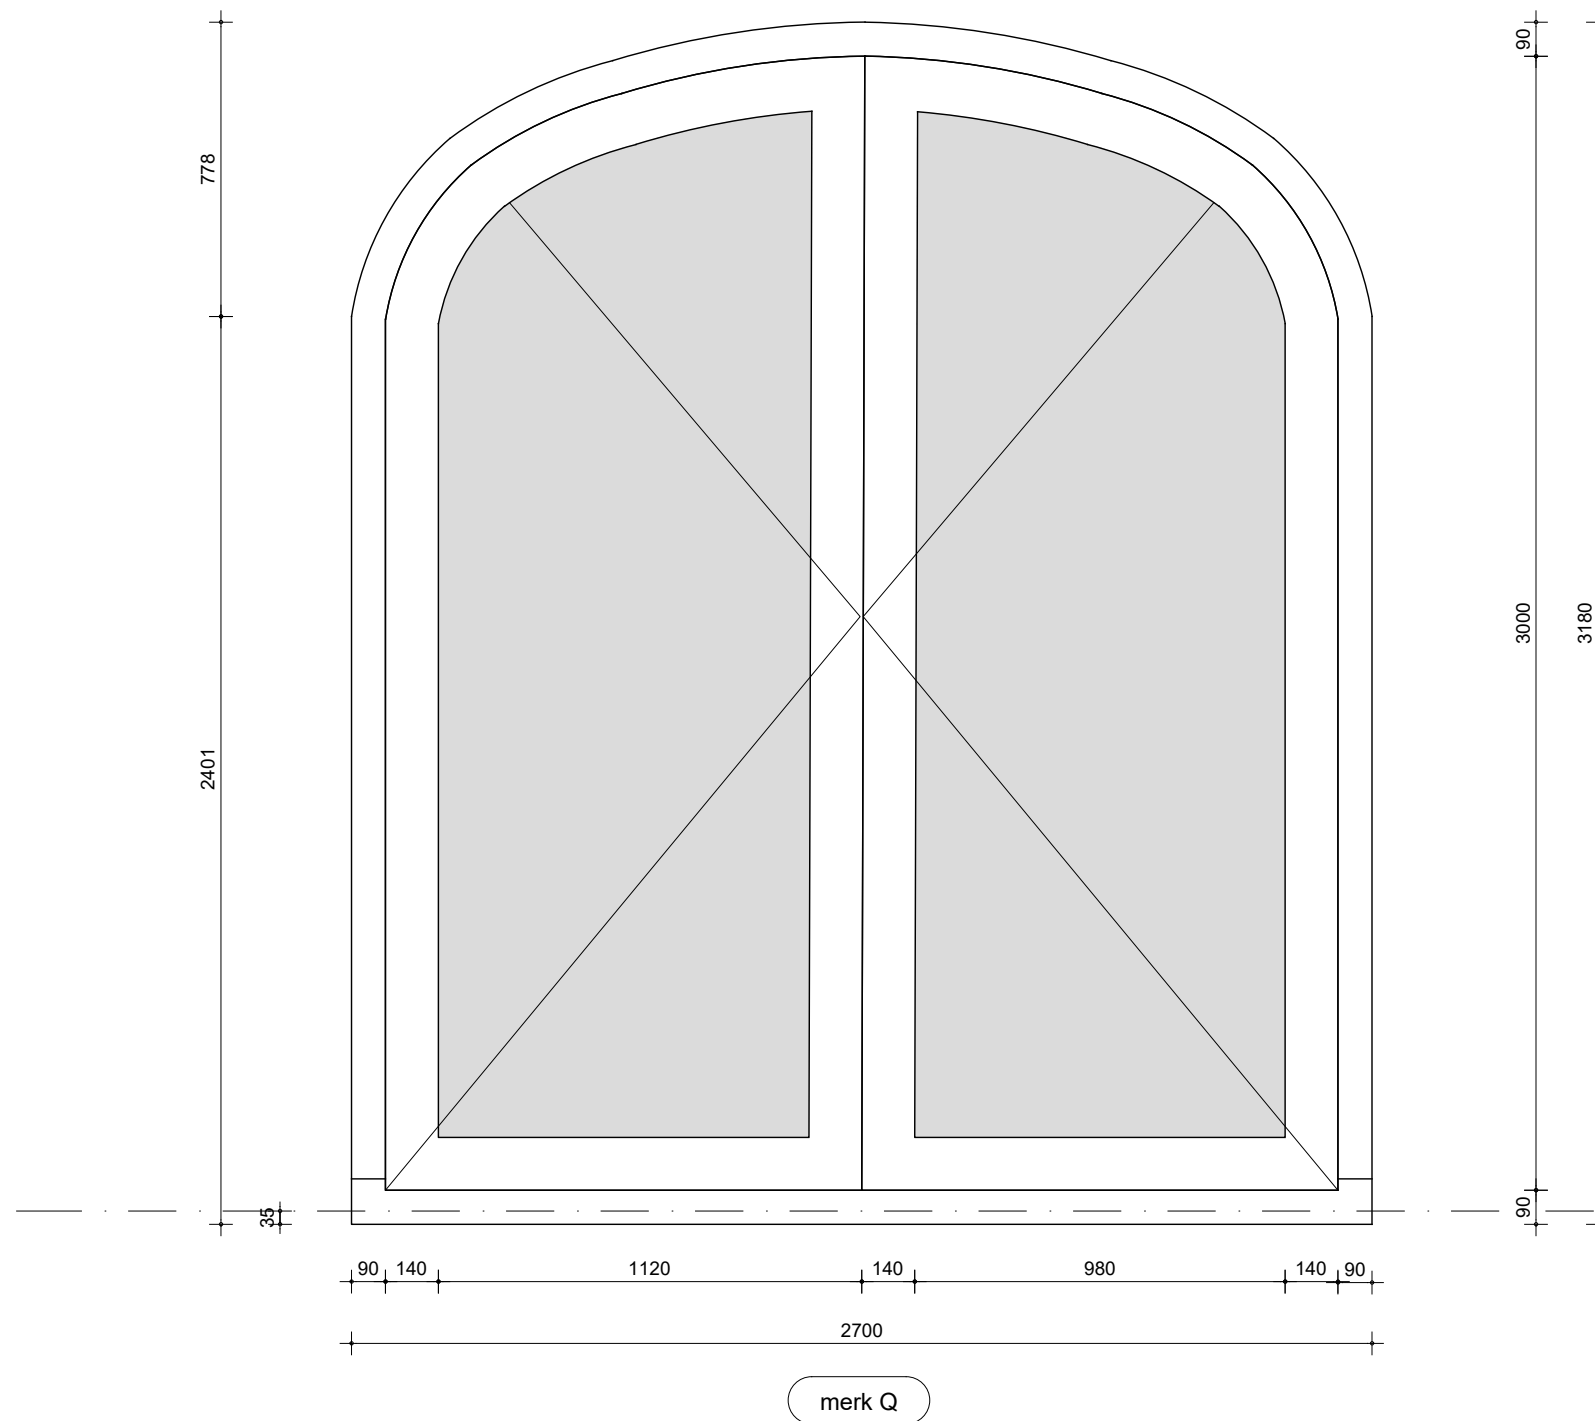

Alle maatvoering in het werk te controleren.
Alle hout-, staal- & betonconstructies volgens constructeur.


Kozijntekeningen

project: Verduurzaming en verbouwing | Buzziburglaan 16 | 3972 EE Driebergen
fase: Definitief ontwerp schaal: 1:20 op A3
datum: 03-07-2026 | TtK wijziging:

25-03.DO.520

Kraal architecten BV | Vossegatselaan 32 | 3583 RT Utrecht | 030 223 96 77
www.kraalarchitecten.nl | info@kraalarchitecten.nl



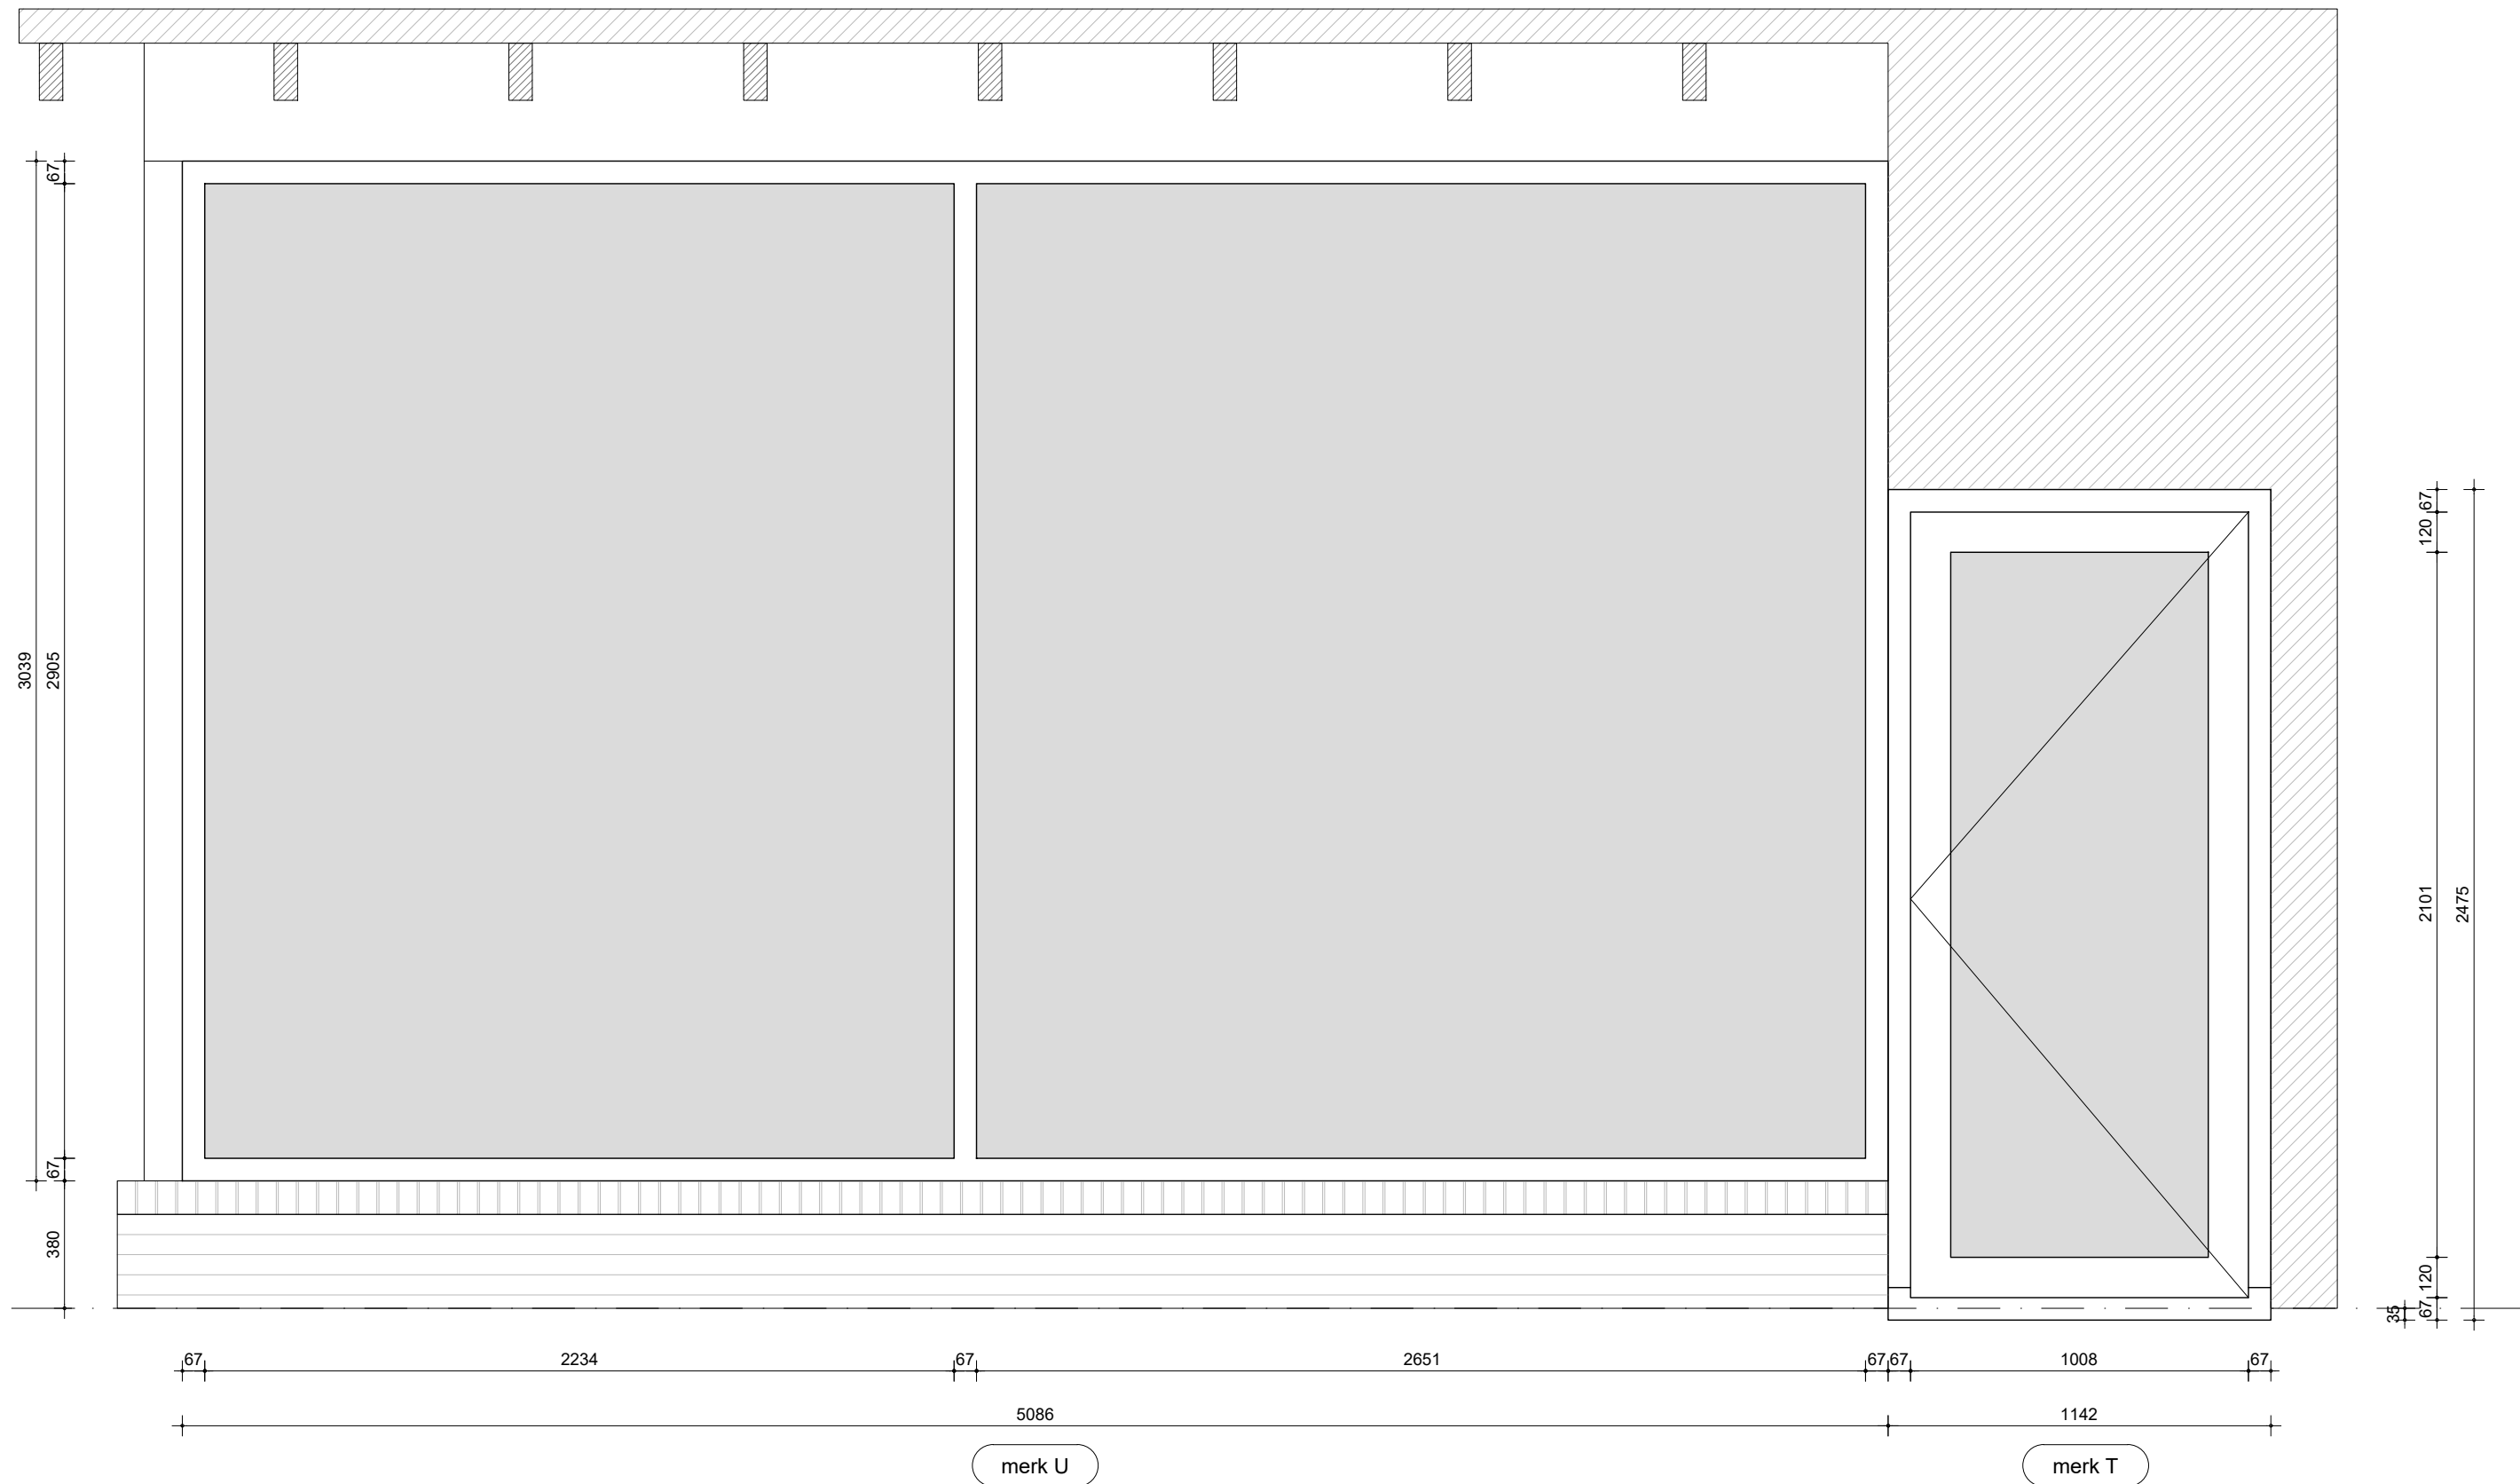

Alle maatvoering in het werk te controleren.
Alle hout-, staal- & betonconstructies volgens constructeur.


Kozijntekeningen

project: Verduurzaming en verbouwing | Buzziburglaan 16 | 3972 EE Driebergen
fase: Definitief ontwerp schaal: 1:20 op A3
datum: 03-07-2026 | TtK wijziging:

25-03.DO.521

Kraal architecten BV | Vossegatselaan 32 | 3583 RT Utrecht | 030 223 96 77
www.kraalarchitecten.nl | info@kraalarchitecten.nl



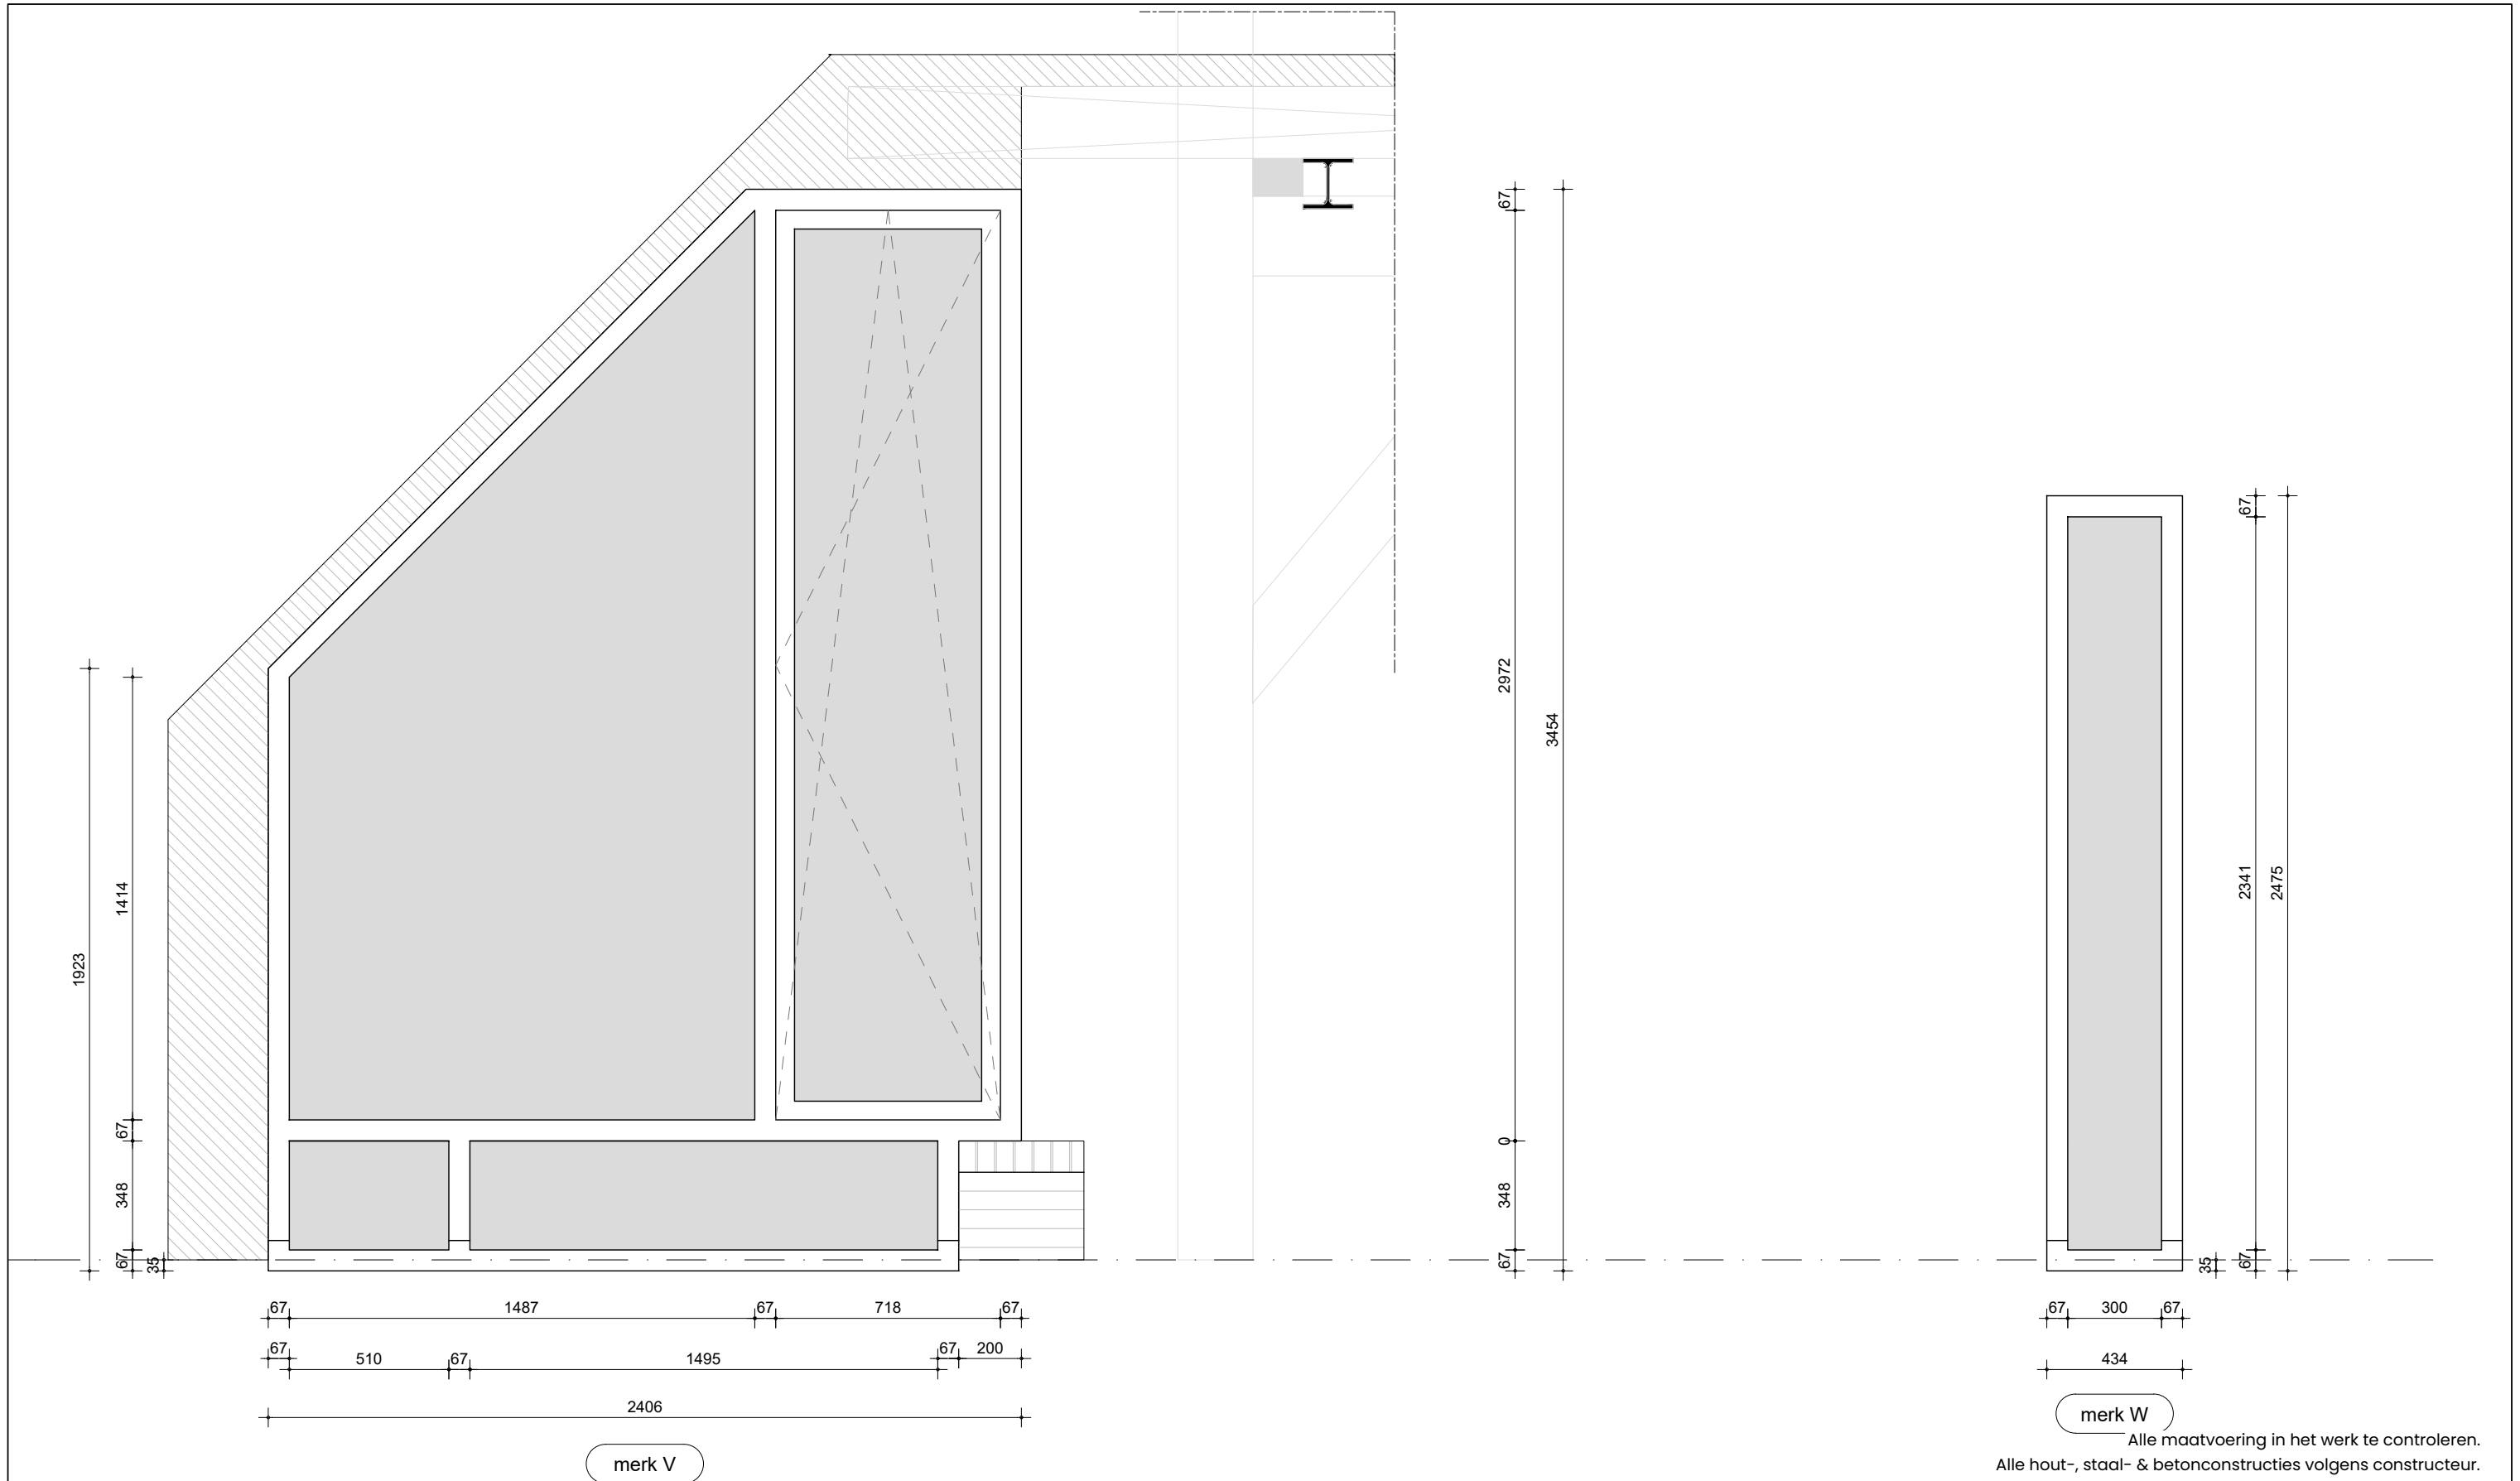

Kozijntekeningen

project: Verduurzaming en verbouwing | Buzziburglaan 16 | 3972 EE Driebergen
fase: Definitief ontwerp schaal: 1:20 op A3
datum: 03-07-2026 | TtK wijziging:

25-03.DO.521

Kraal architecten BV | Vossegatselaan 32 | 3583 RT Utrecht | 030 223 96 77
www.kraalarchitecten.nl | info@kraalarchitecten.nl

